


サンプル住宅 平面図 101号室

Rev.B 2026-05-01

縮尺: 1/100 単位: mm


作図: 設計室

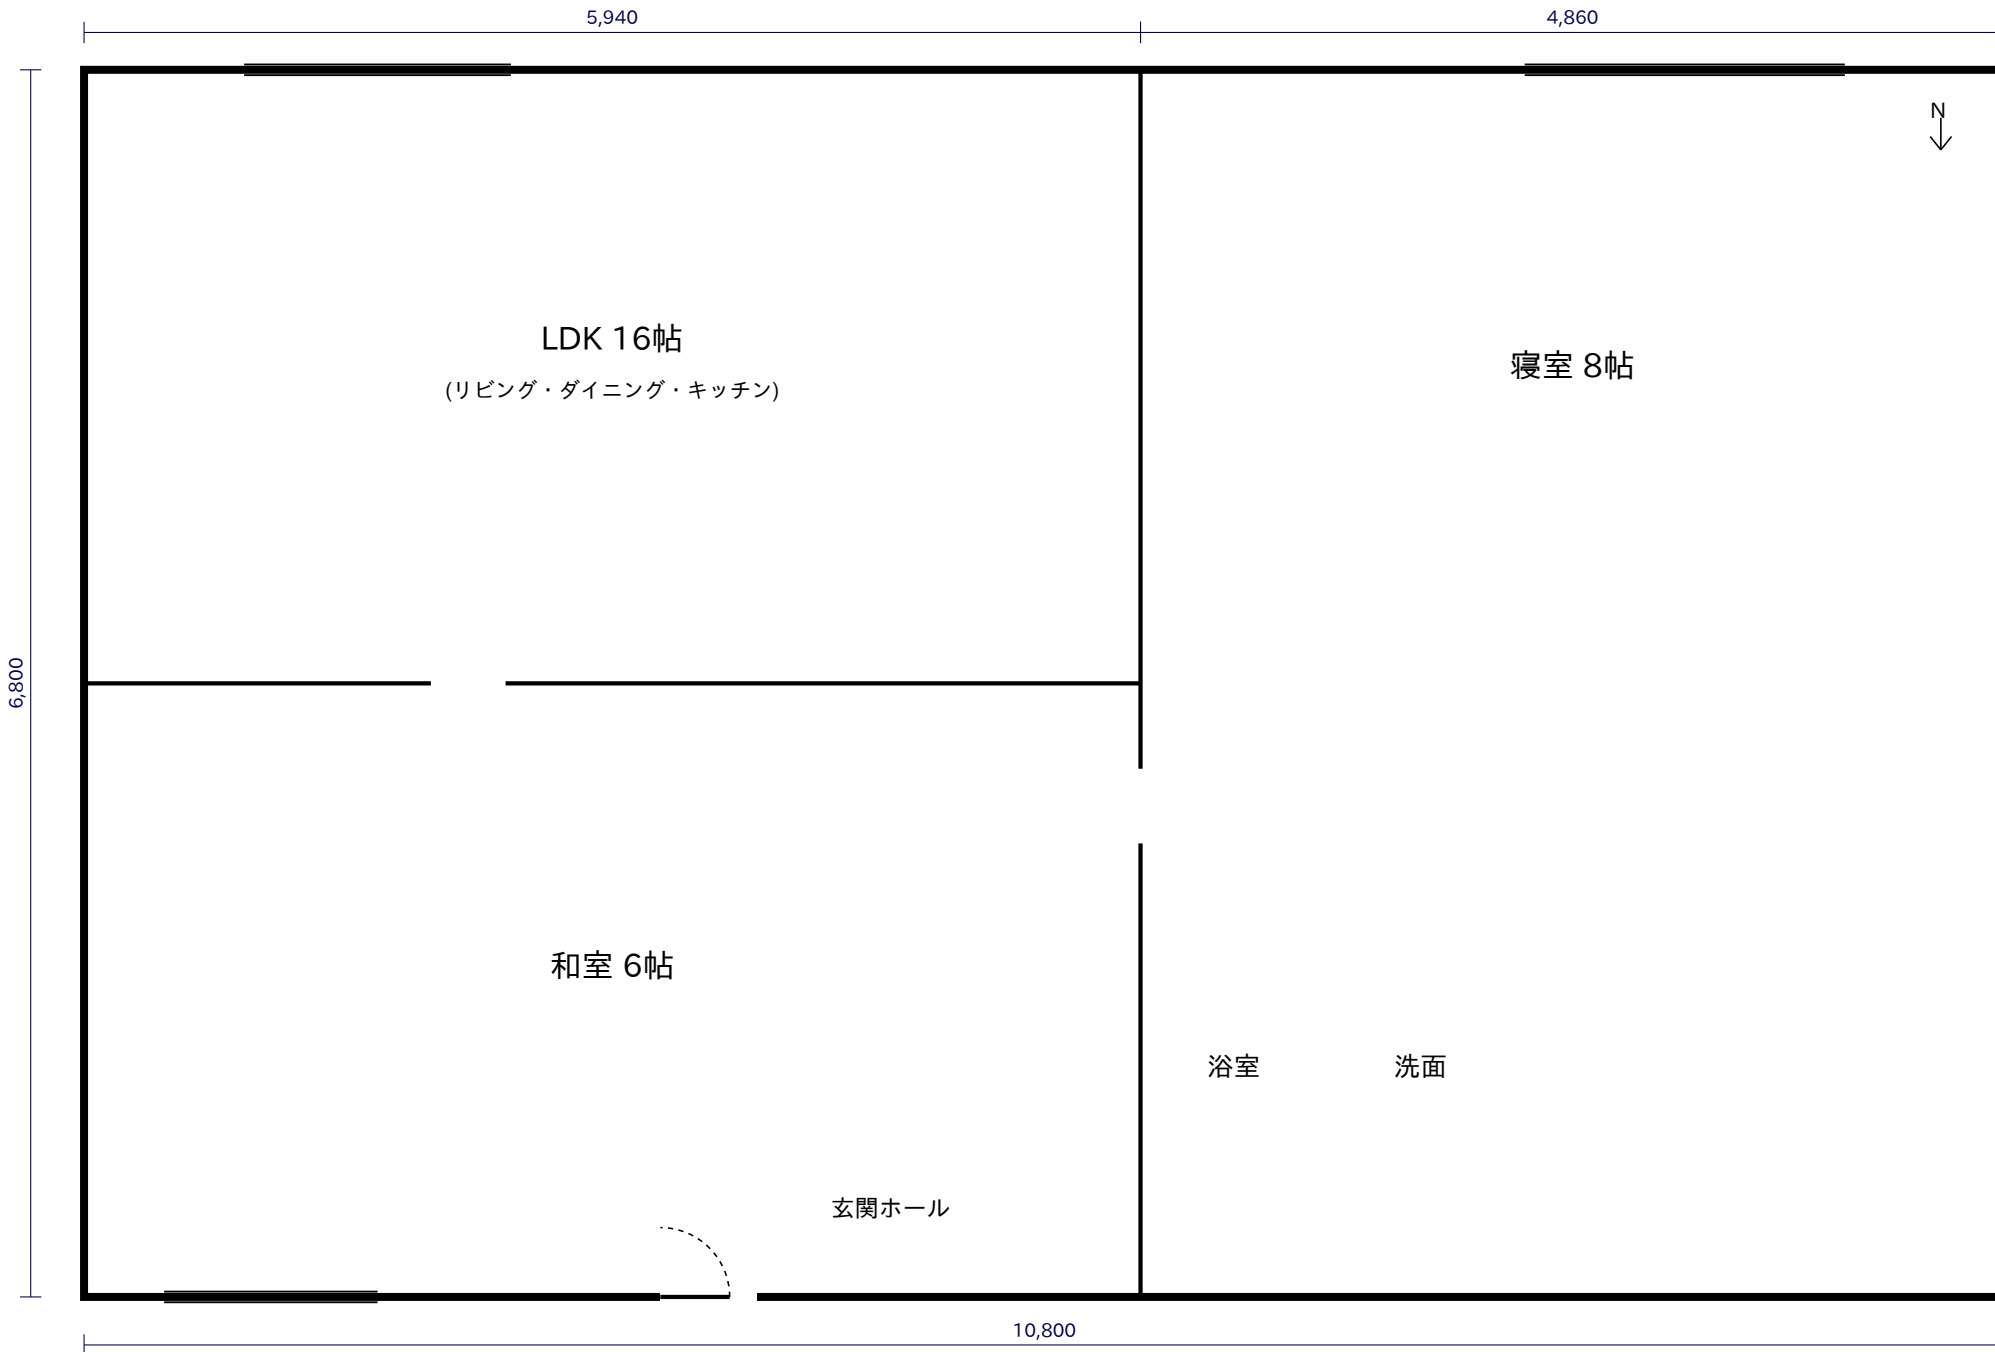

サンプル住宅 平面図 102号室

Rev.B 2026-05-01


縮尺: 1/100 単位: mm
作図: 設計室

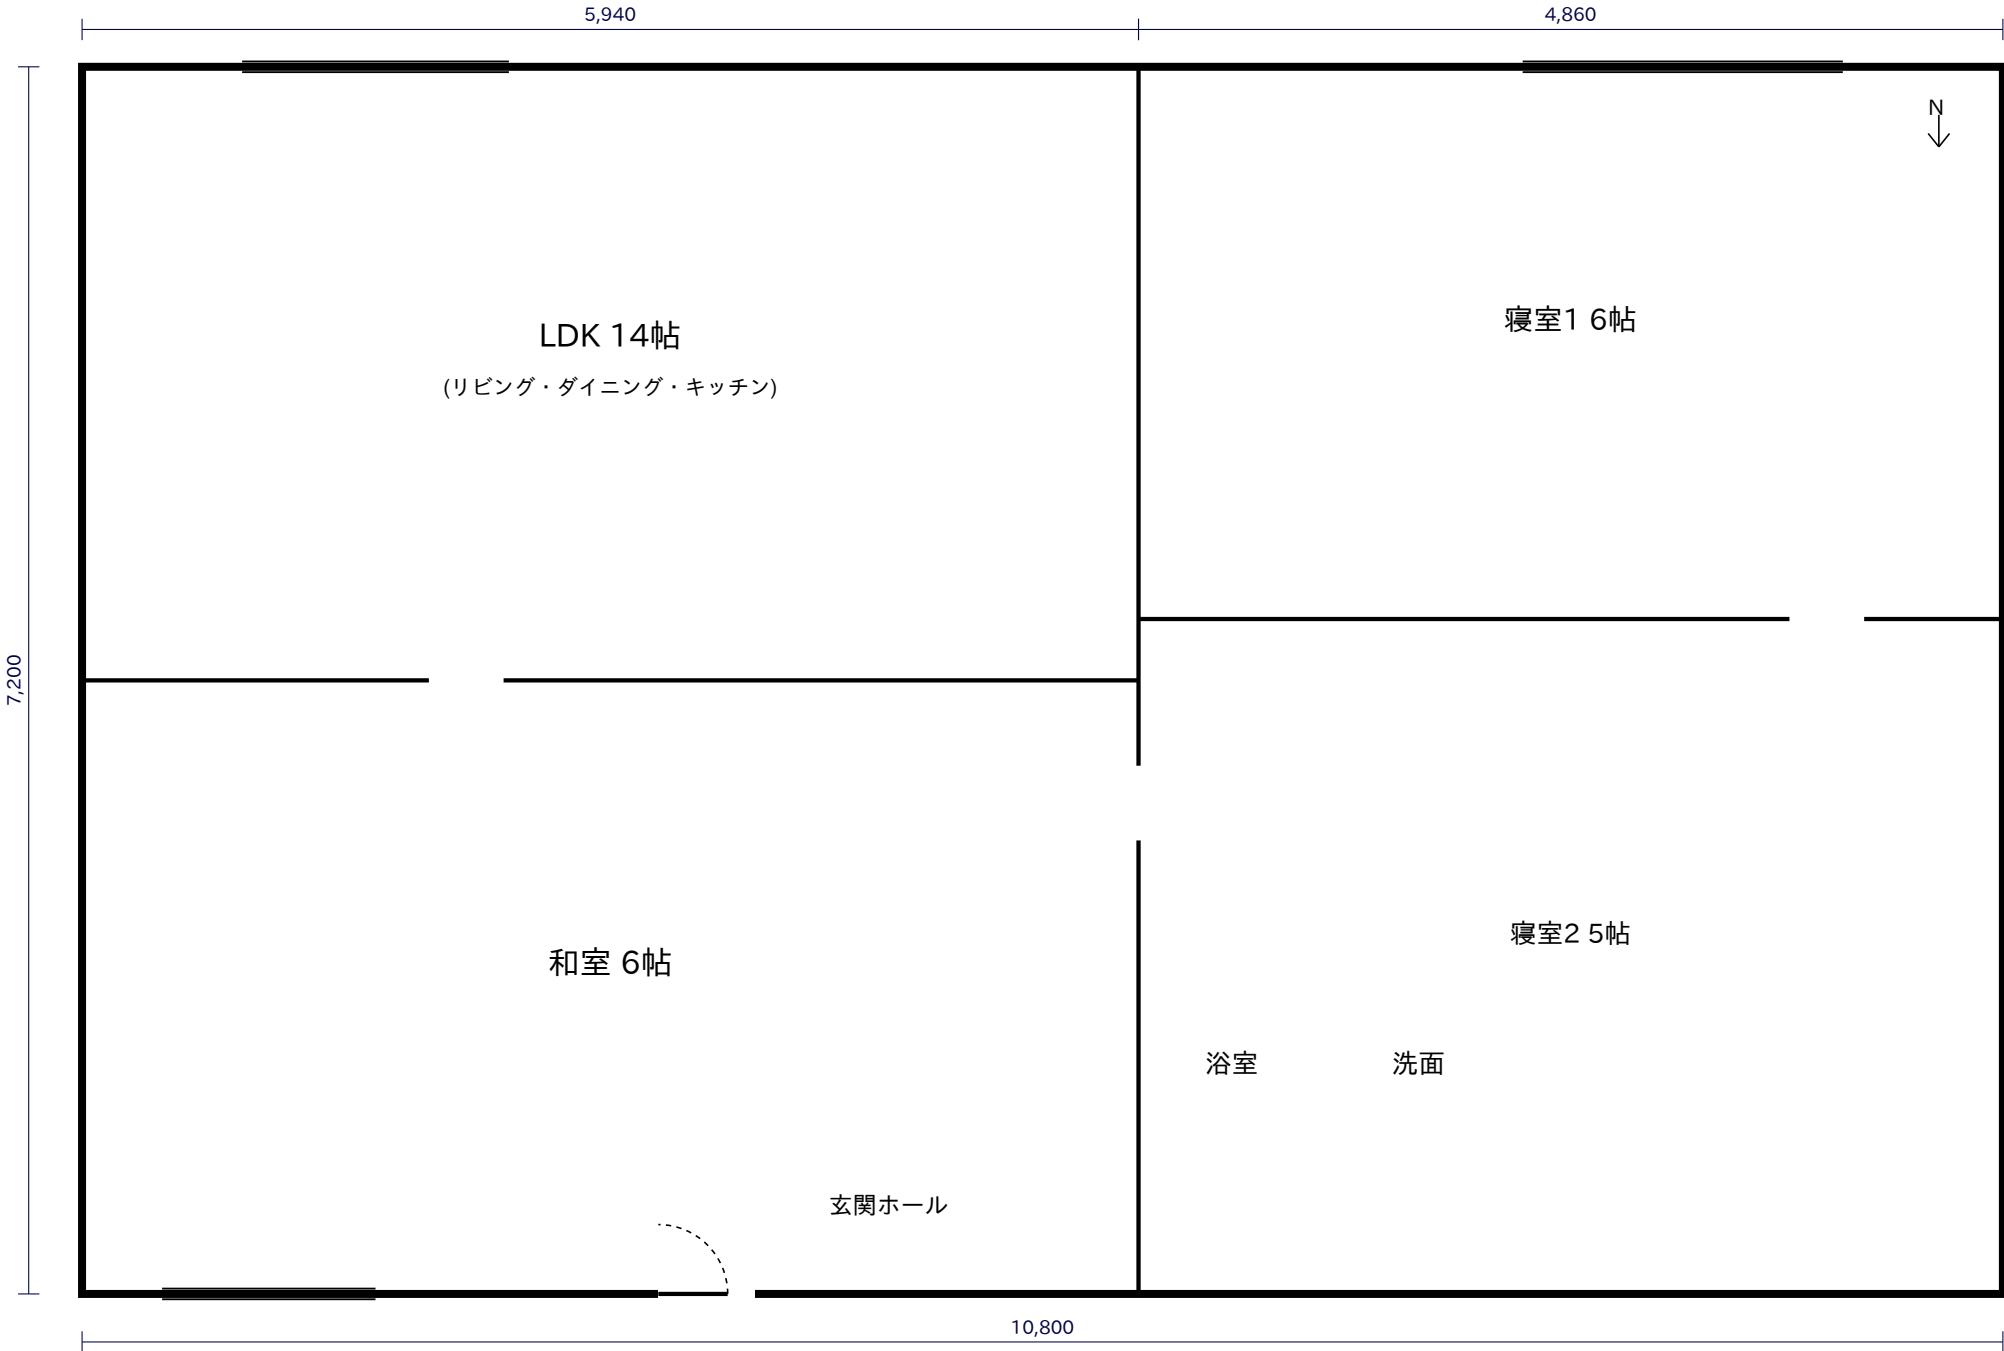

サンプル住宅 平面図 103号室

Rev.B 2026-05-01


縮尺: 1/100 単位: mm
作図: 設計室

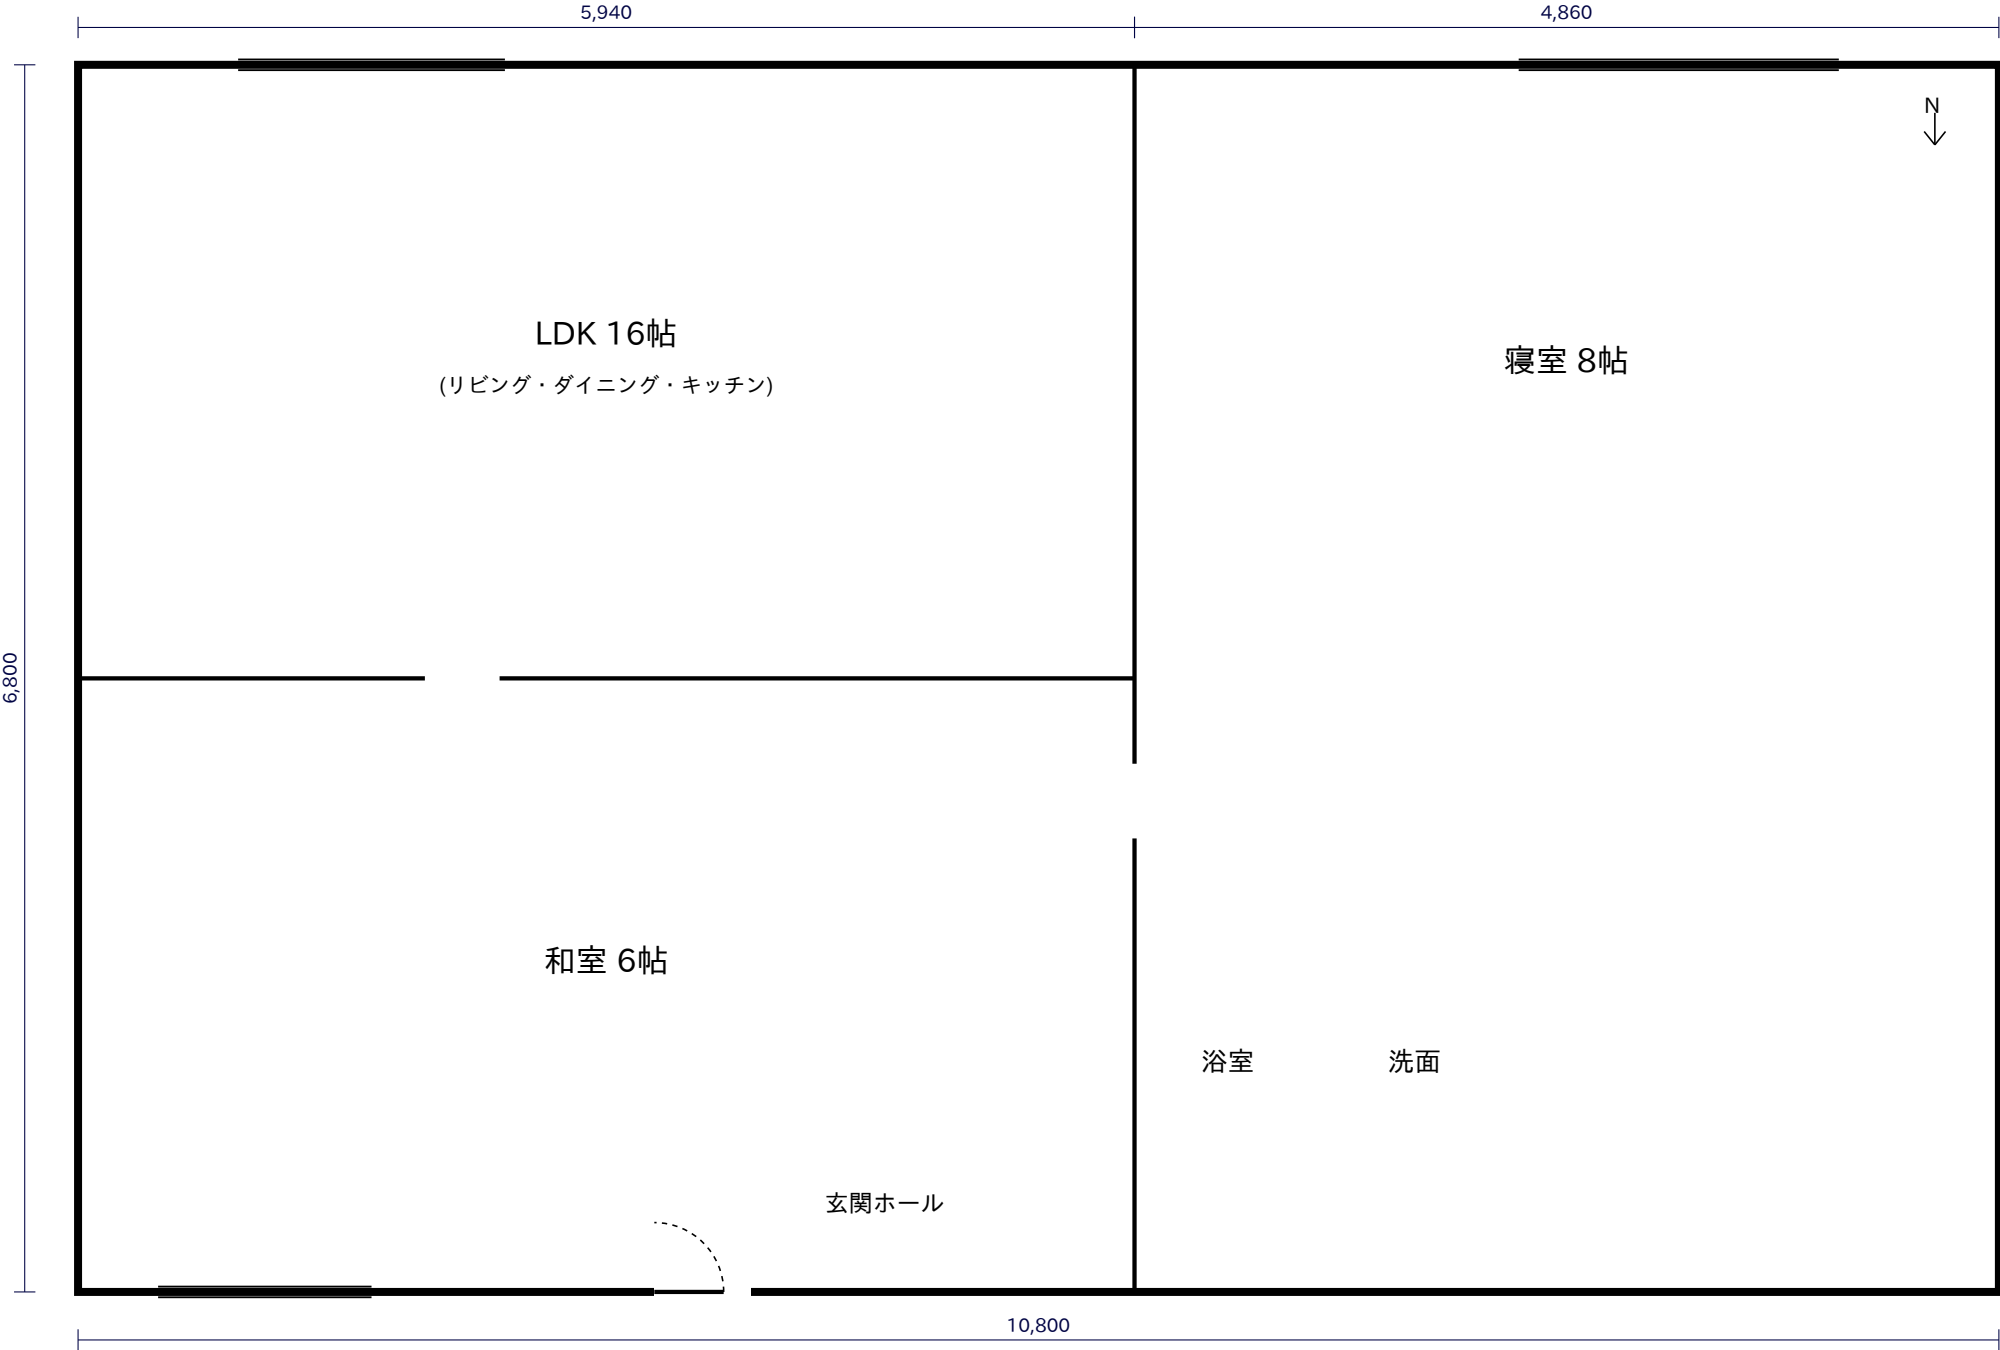

サンプル住宅 平面図 104号室

Rev.B 2026-05-01

縮尺: 1/100 単位: mm
作図: 設計室

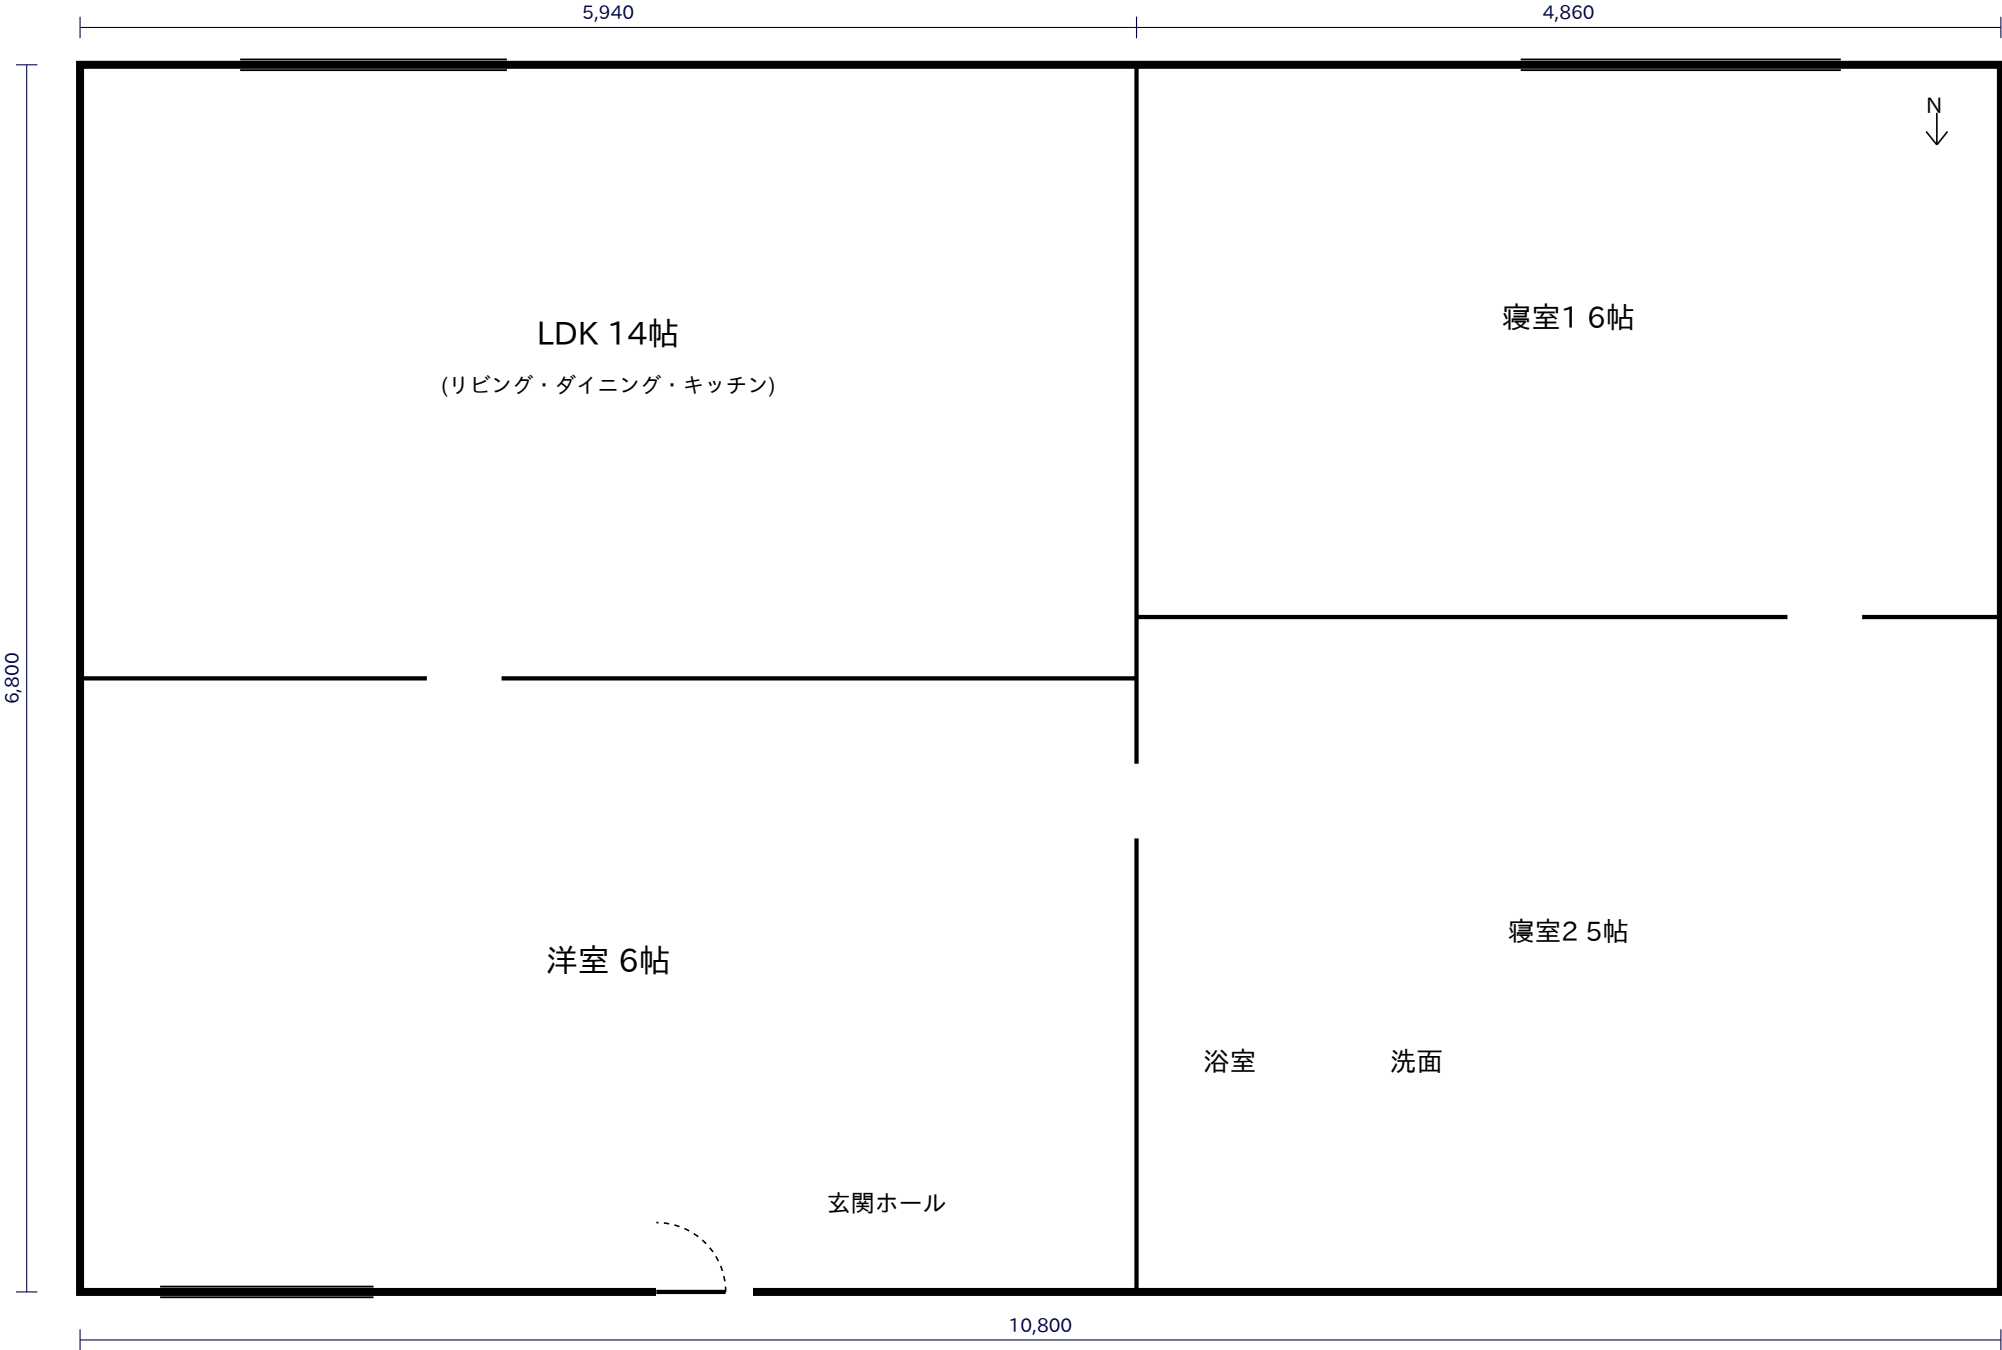


サンプル住宅 平面図 105号室

Rev.B 2026-05-01

縮尺: 1/100 単位: mm


作図: 設計室

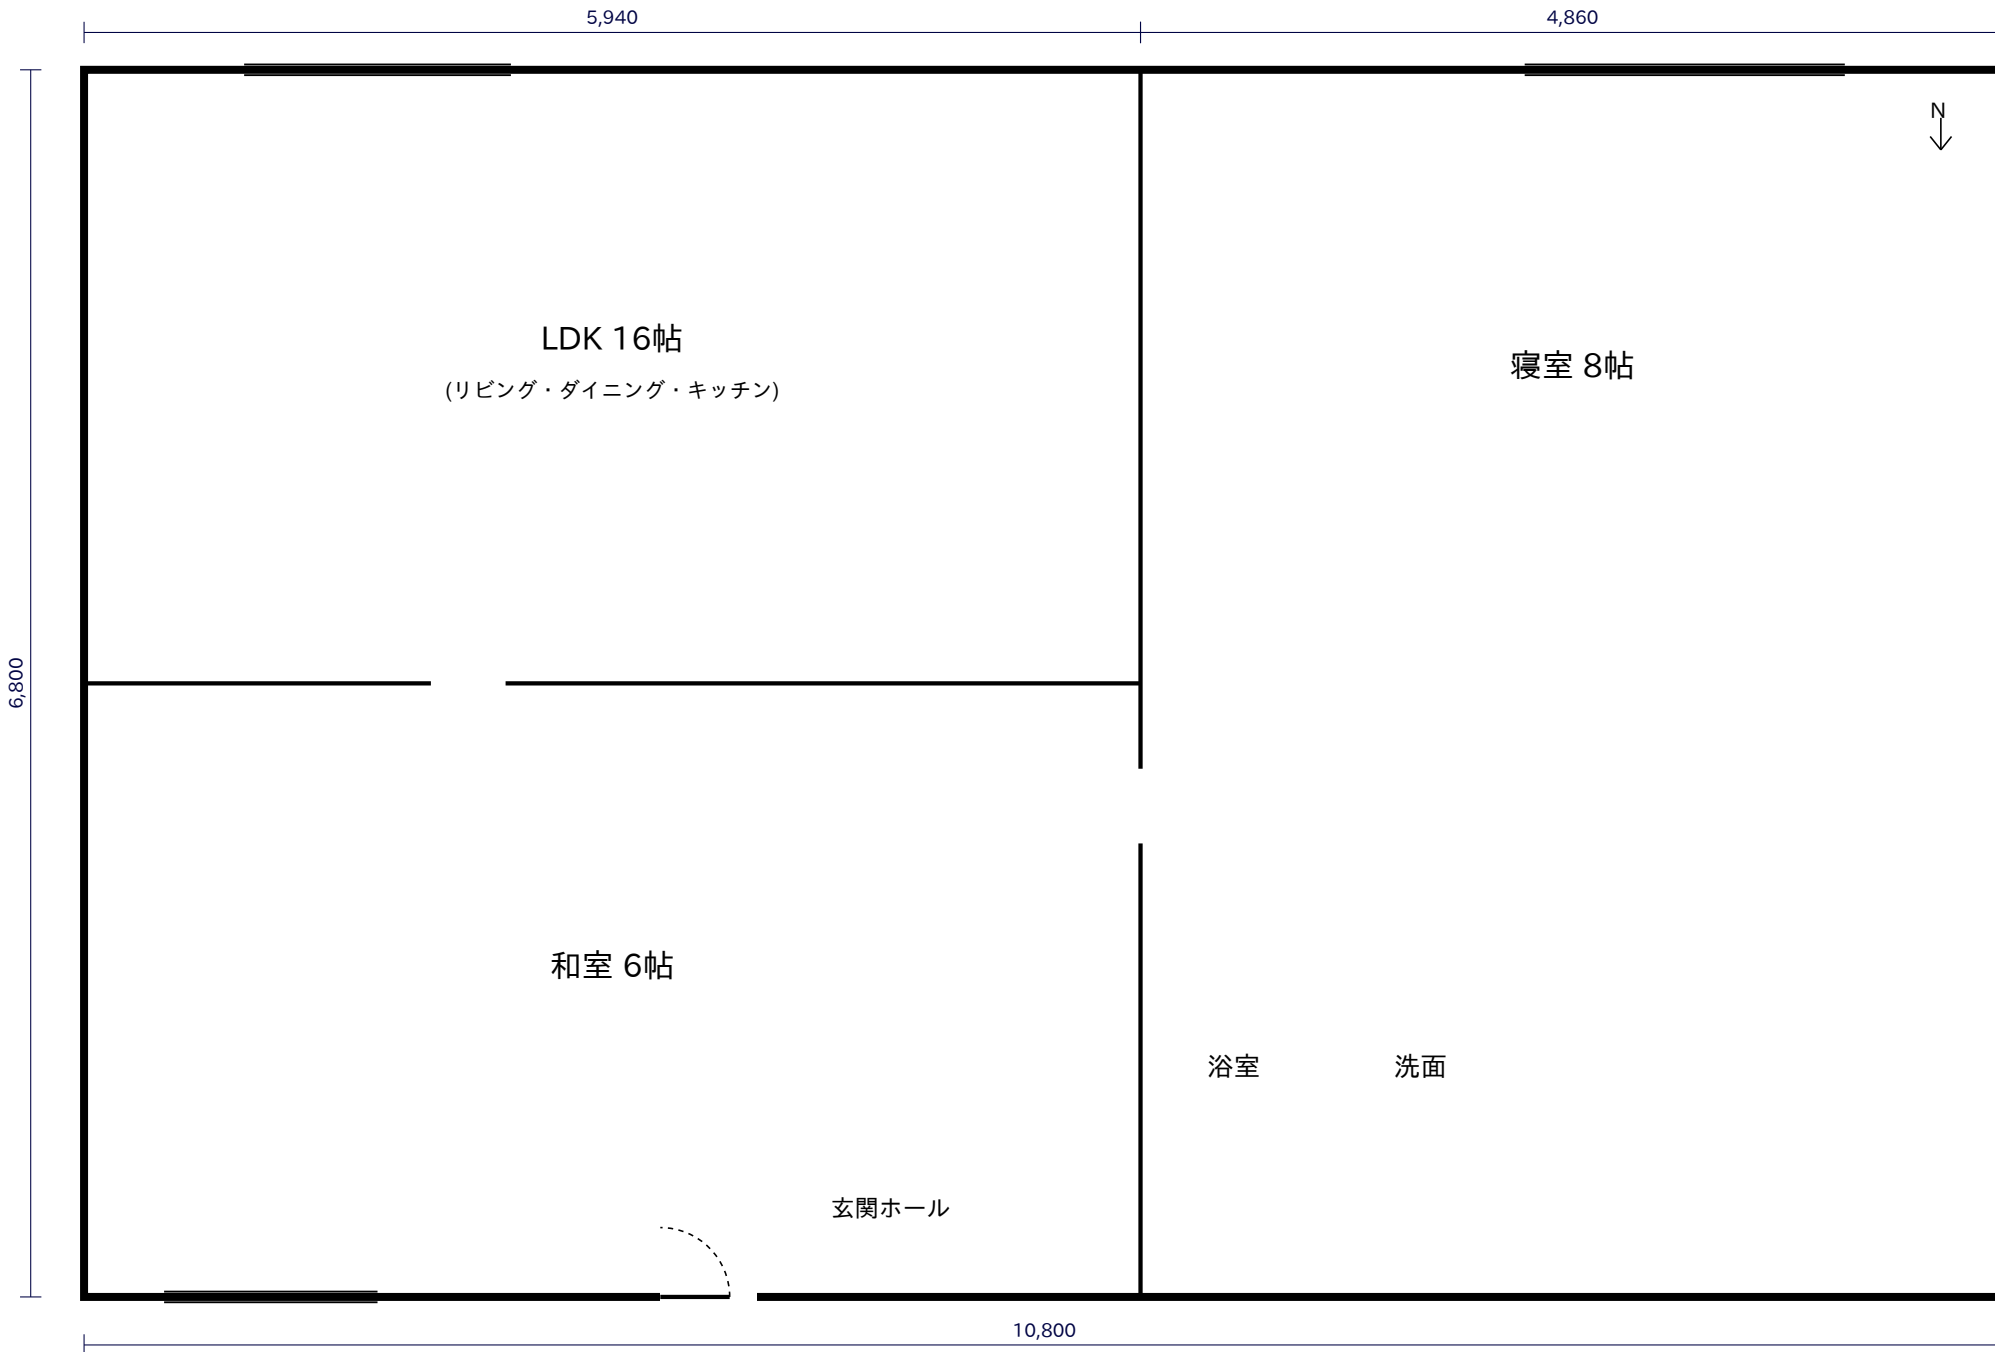

サンプル住宅 平面図 106号室

Rev.B 2026-05-01


縮尺: 1/100 単位: mm
作図: 設計室

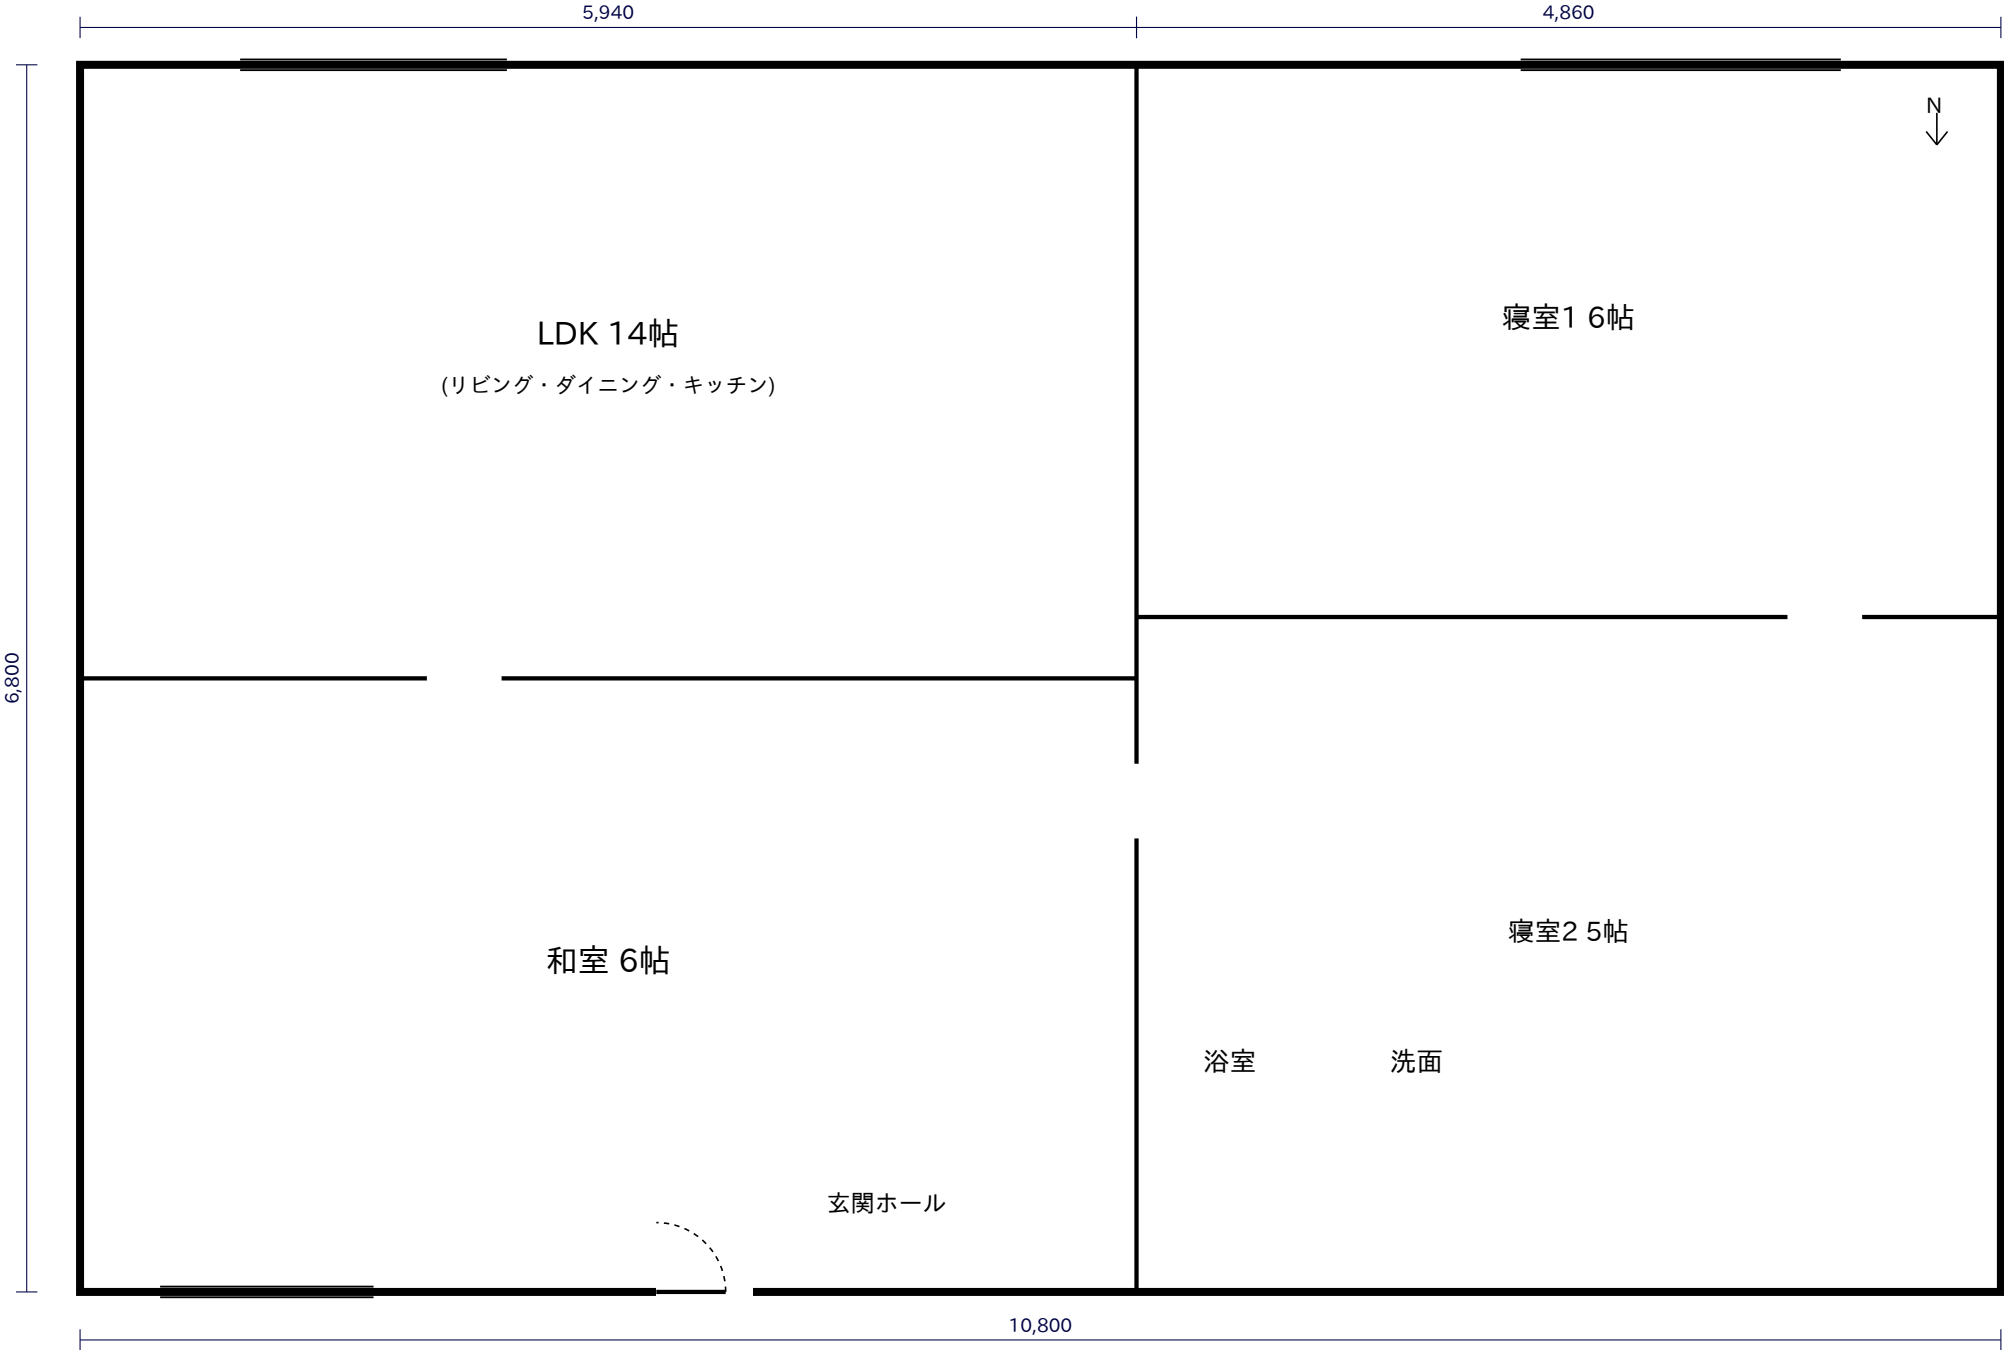

サンプル住宅 平面図 107号室

Rev.B 2026-05-01


縮尺: 1/100 単位: mm
作図: 設計室

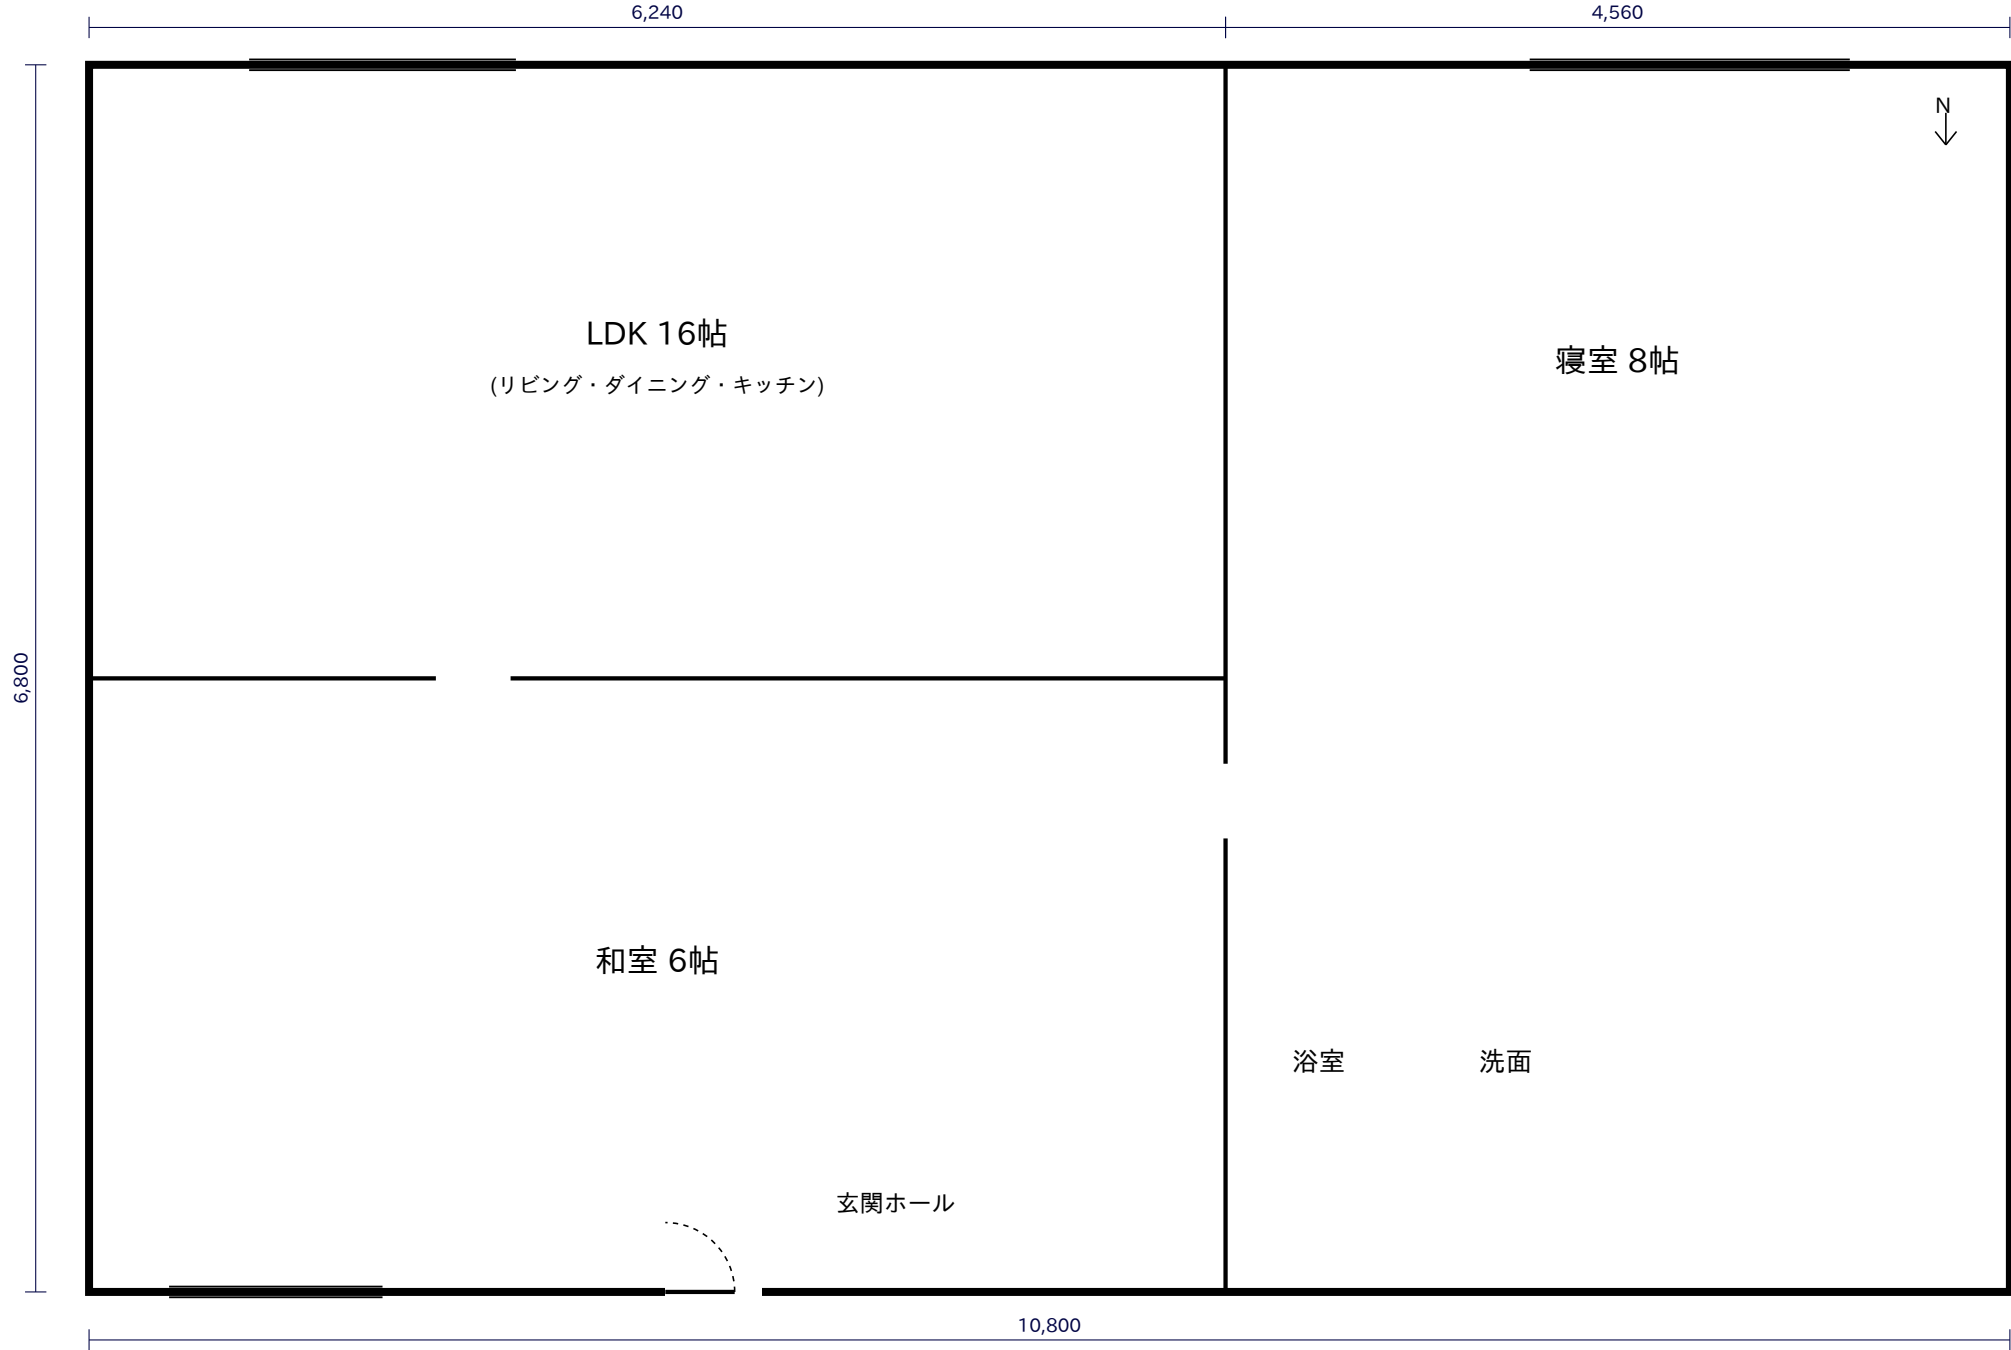

サンプル住宅 平面図 108号室

Rev.B 2026-05-01


縮尺: 1/100 単位: mm
作図: 設計室

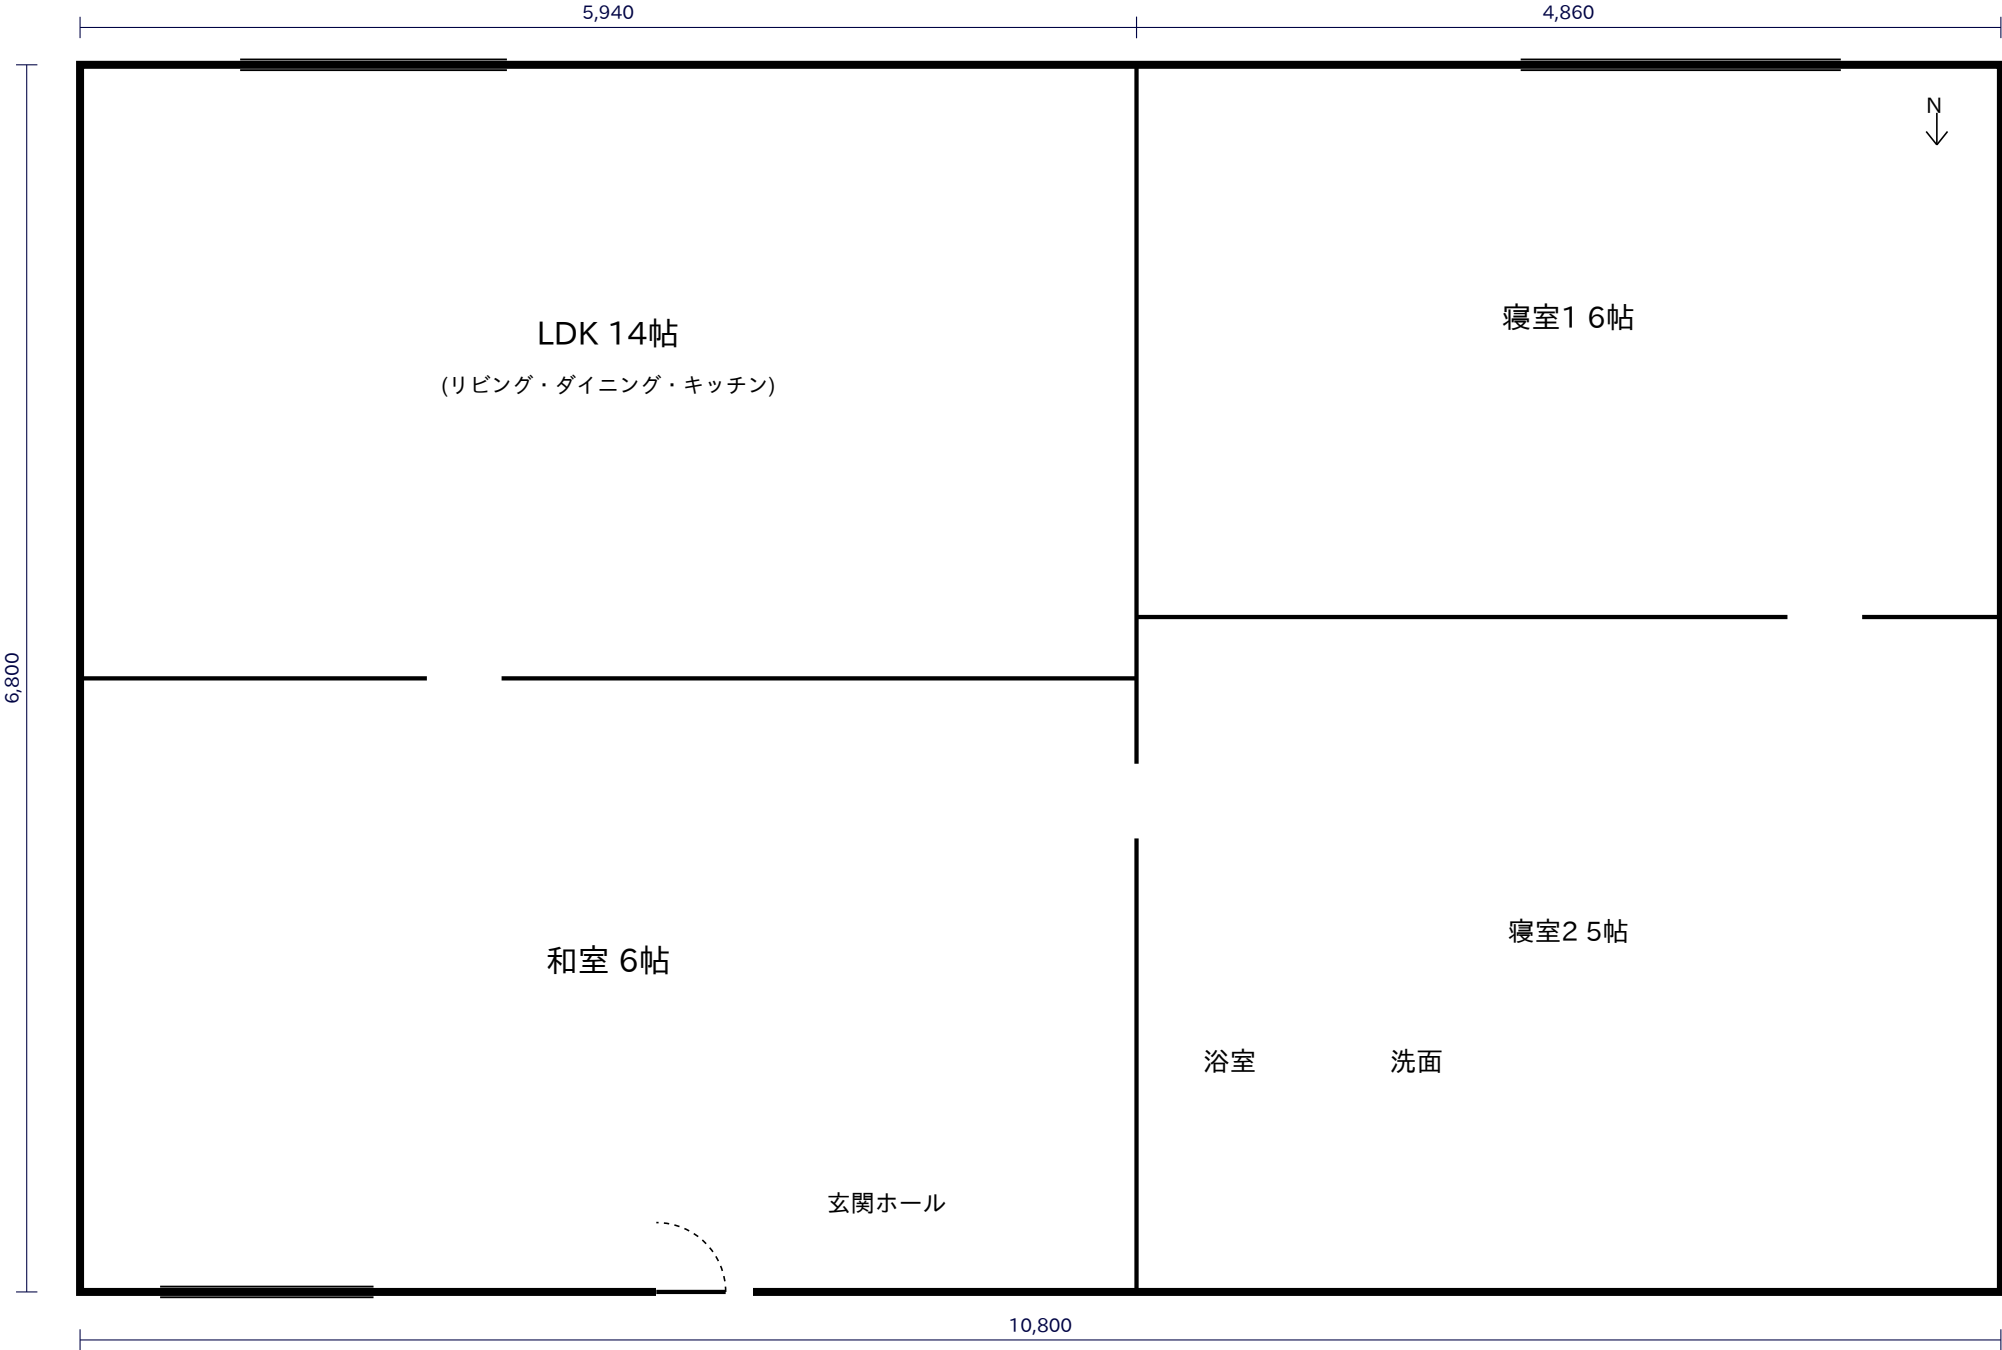

サンプル住宅 平面図 109号室

Rev.B 2026-05-01


縮尺: 1/100 単位: mm
作図: 設計室

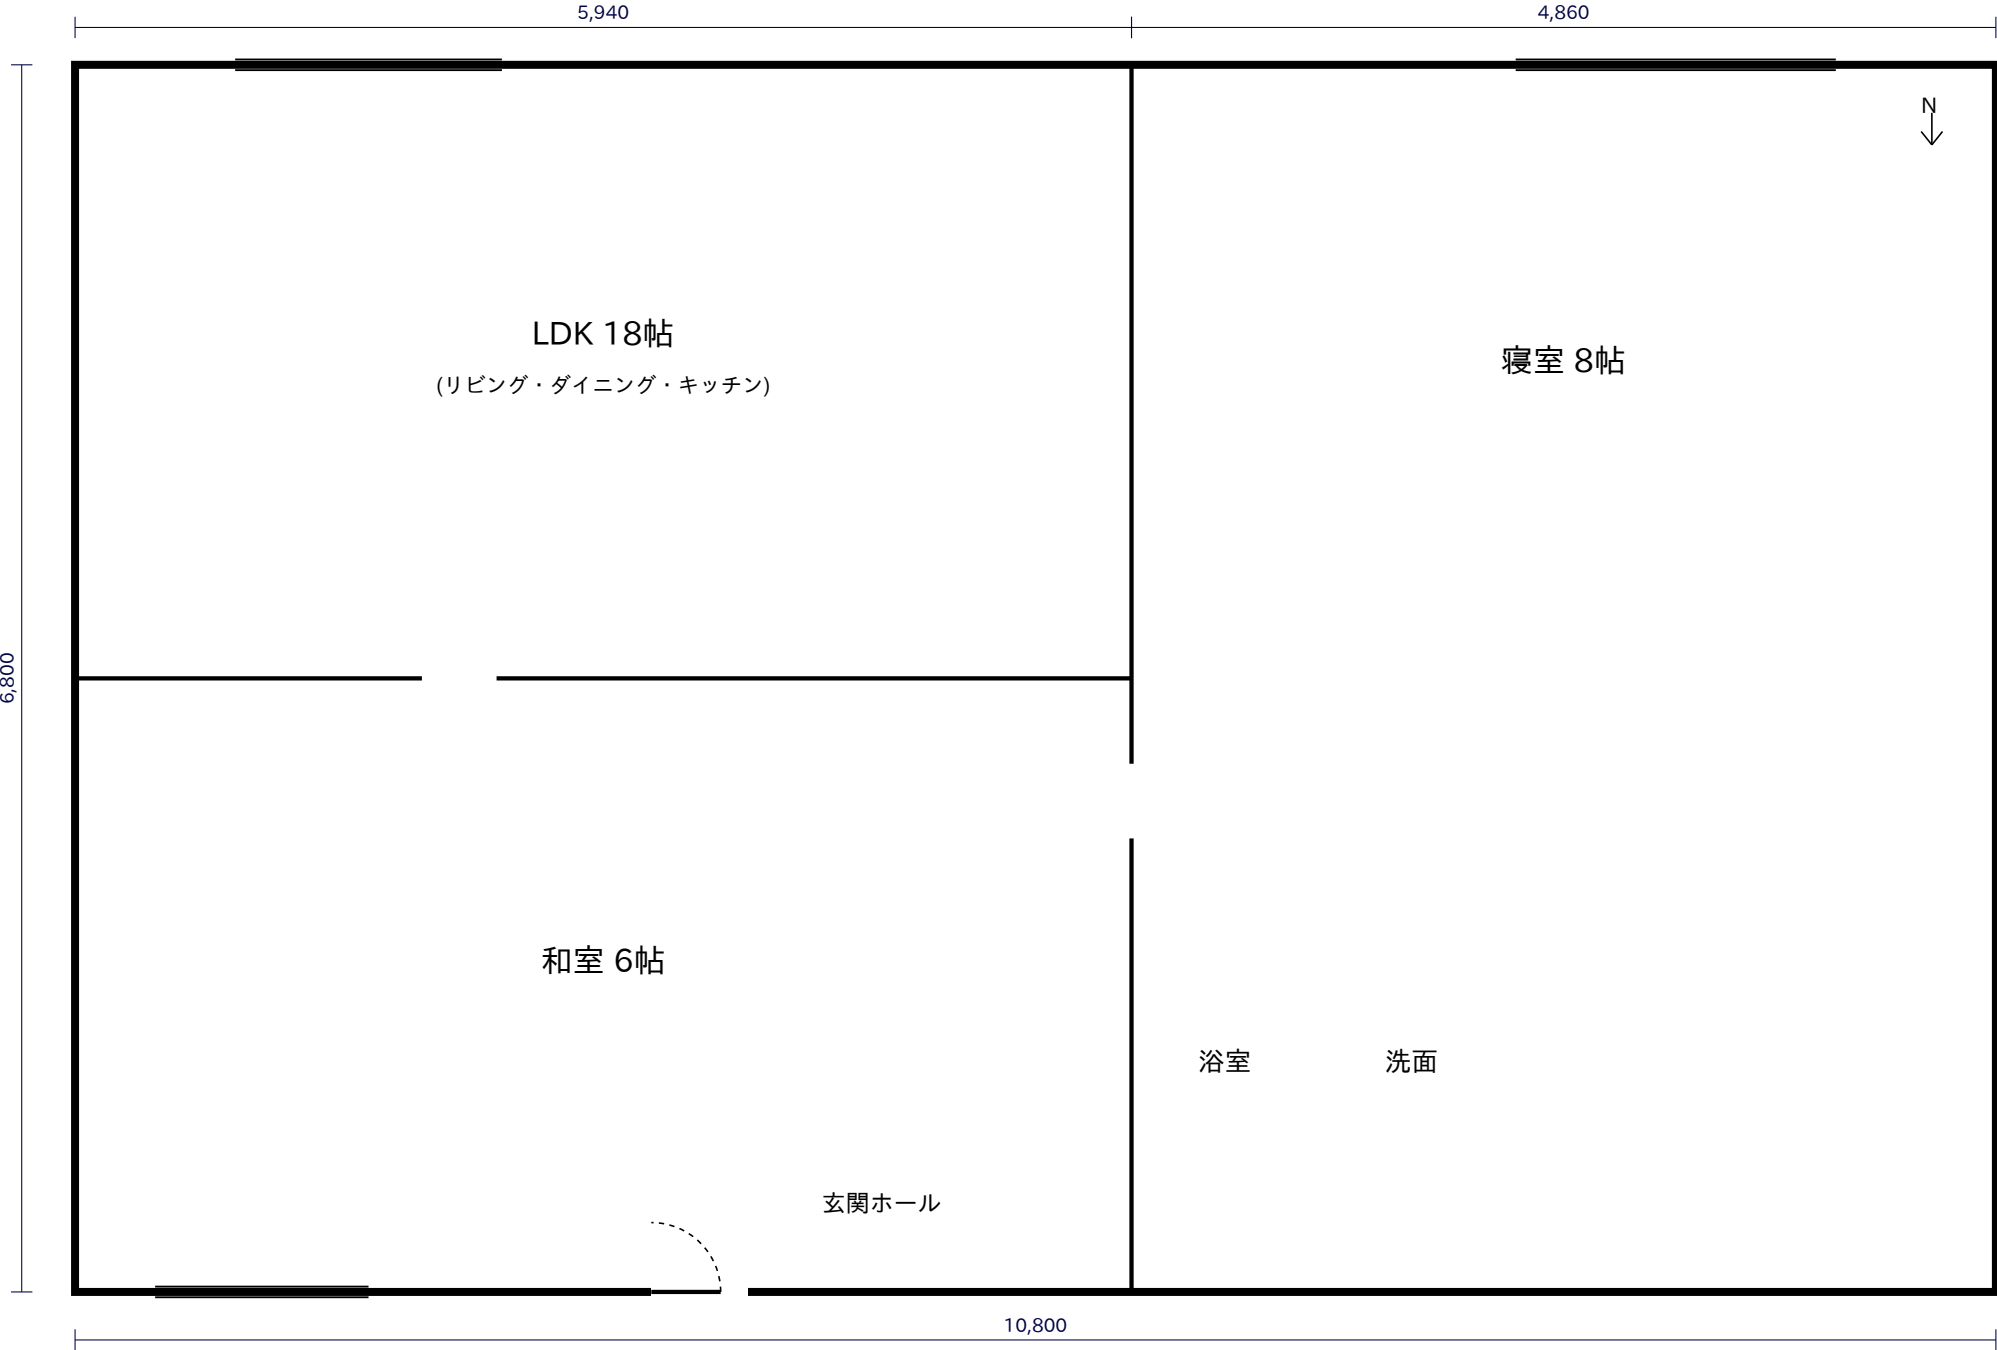

サンプル住宅 平面図 110号室

Rev.B 2026-05-01


縮尺: 1/100 単位: mm
作図: 設計室

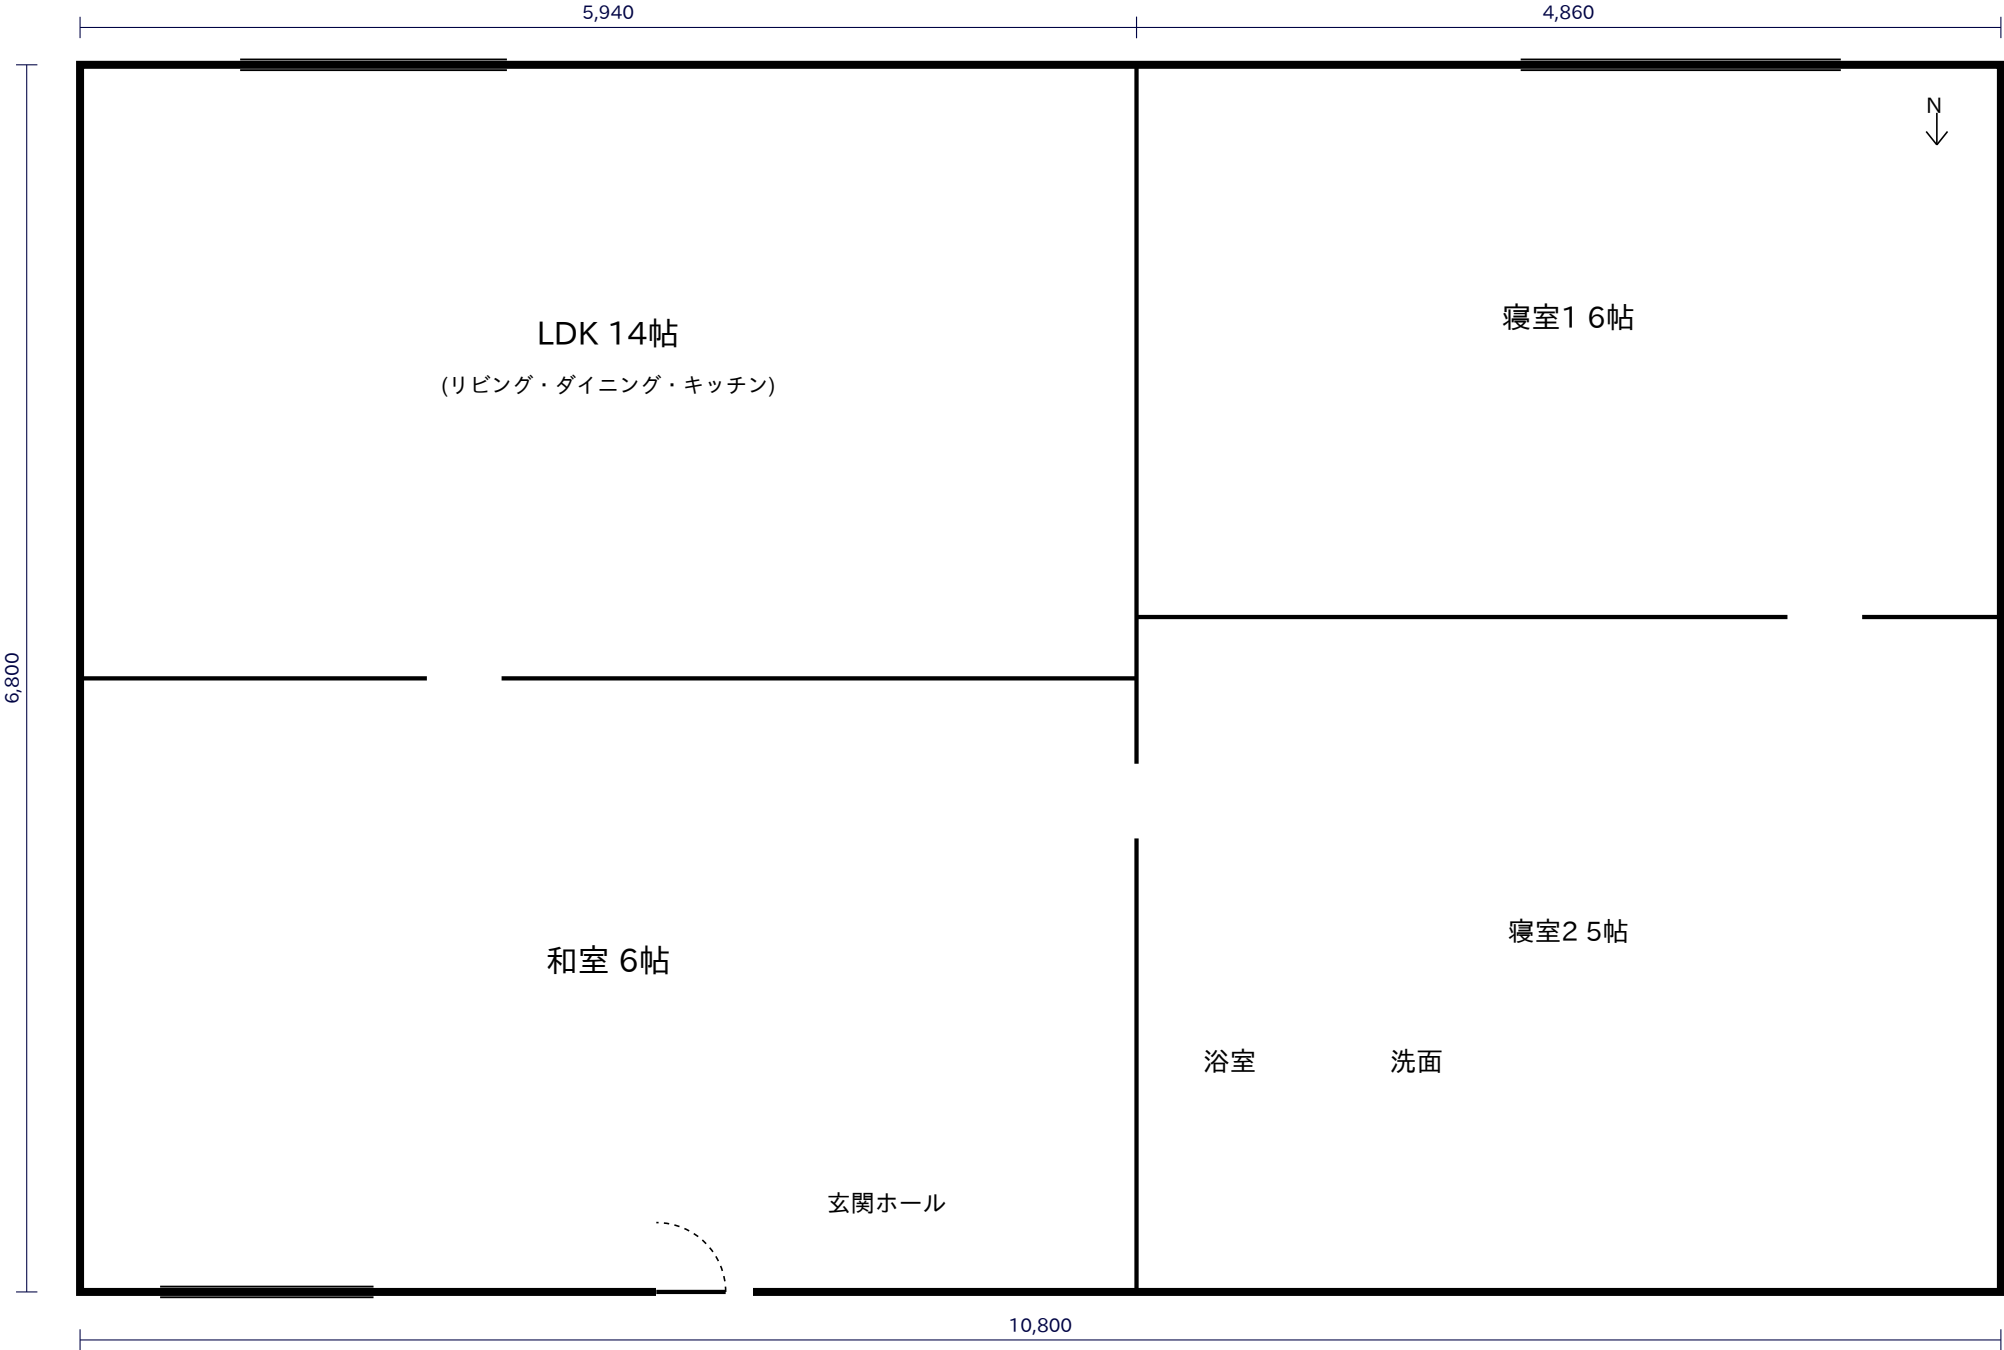

サンプル住宅 平面図 111号室

Rev.B 2026-05-01


縮尺: 1/100 単位: mm
作図: 設計室

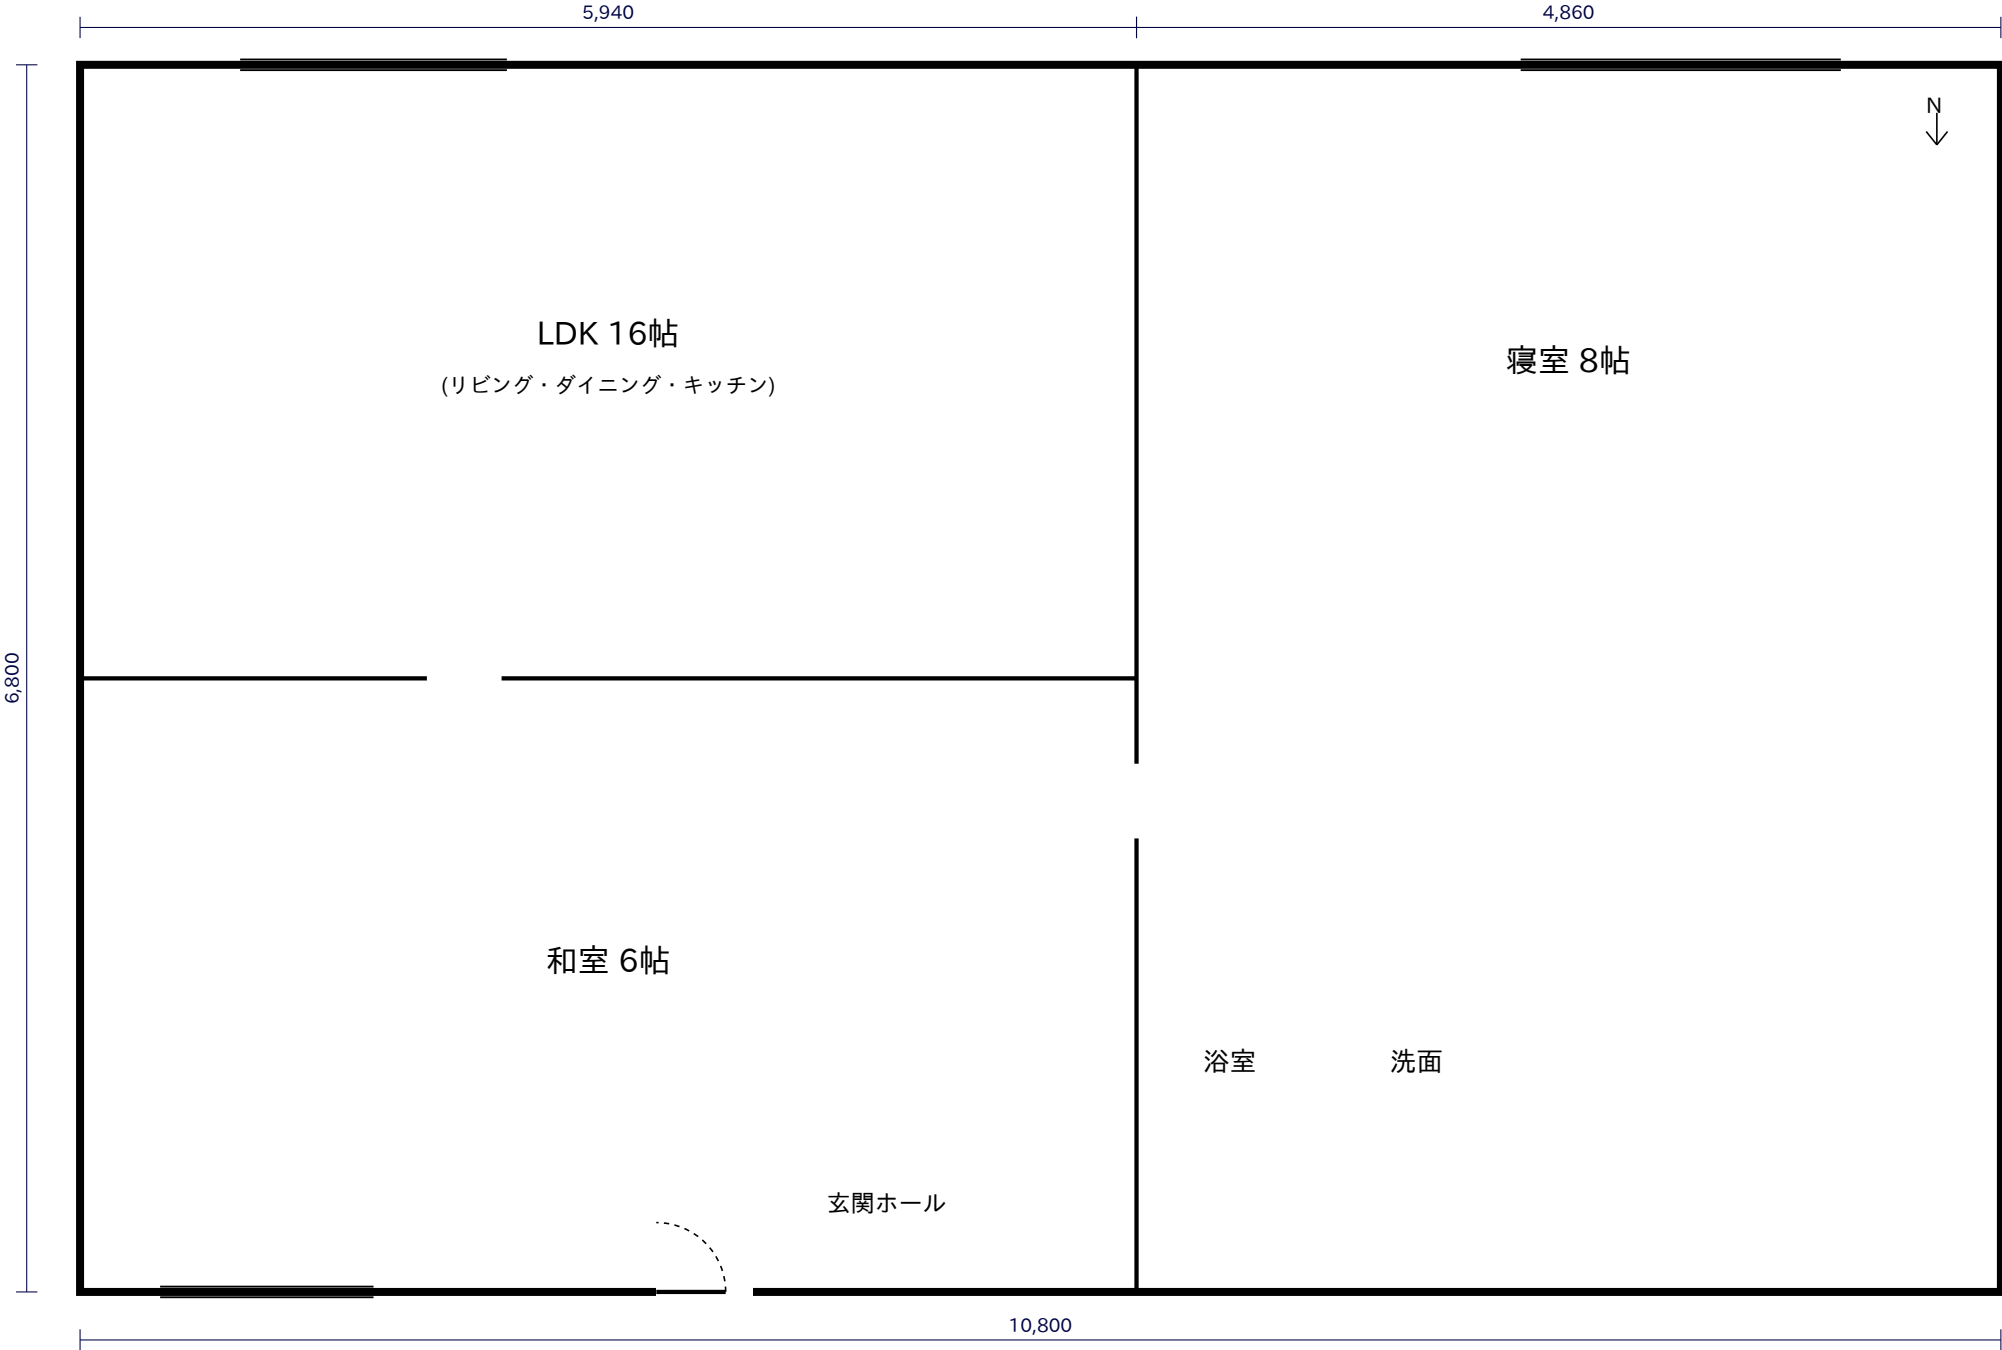

サンプル住宅 平面図 112号室

Rev.B 2026-05-01


縮尺: 1/100 単位: mm
作図: 設計室

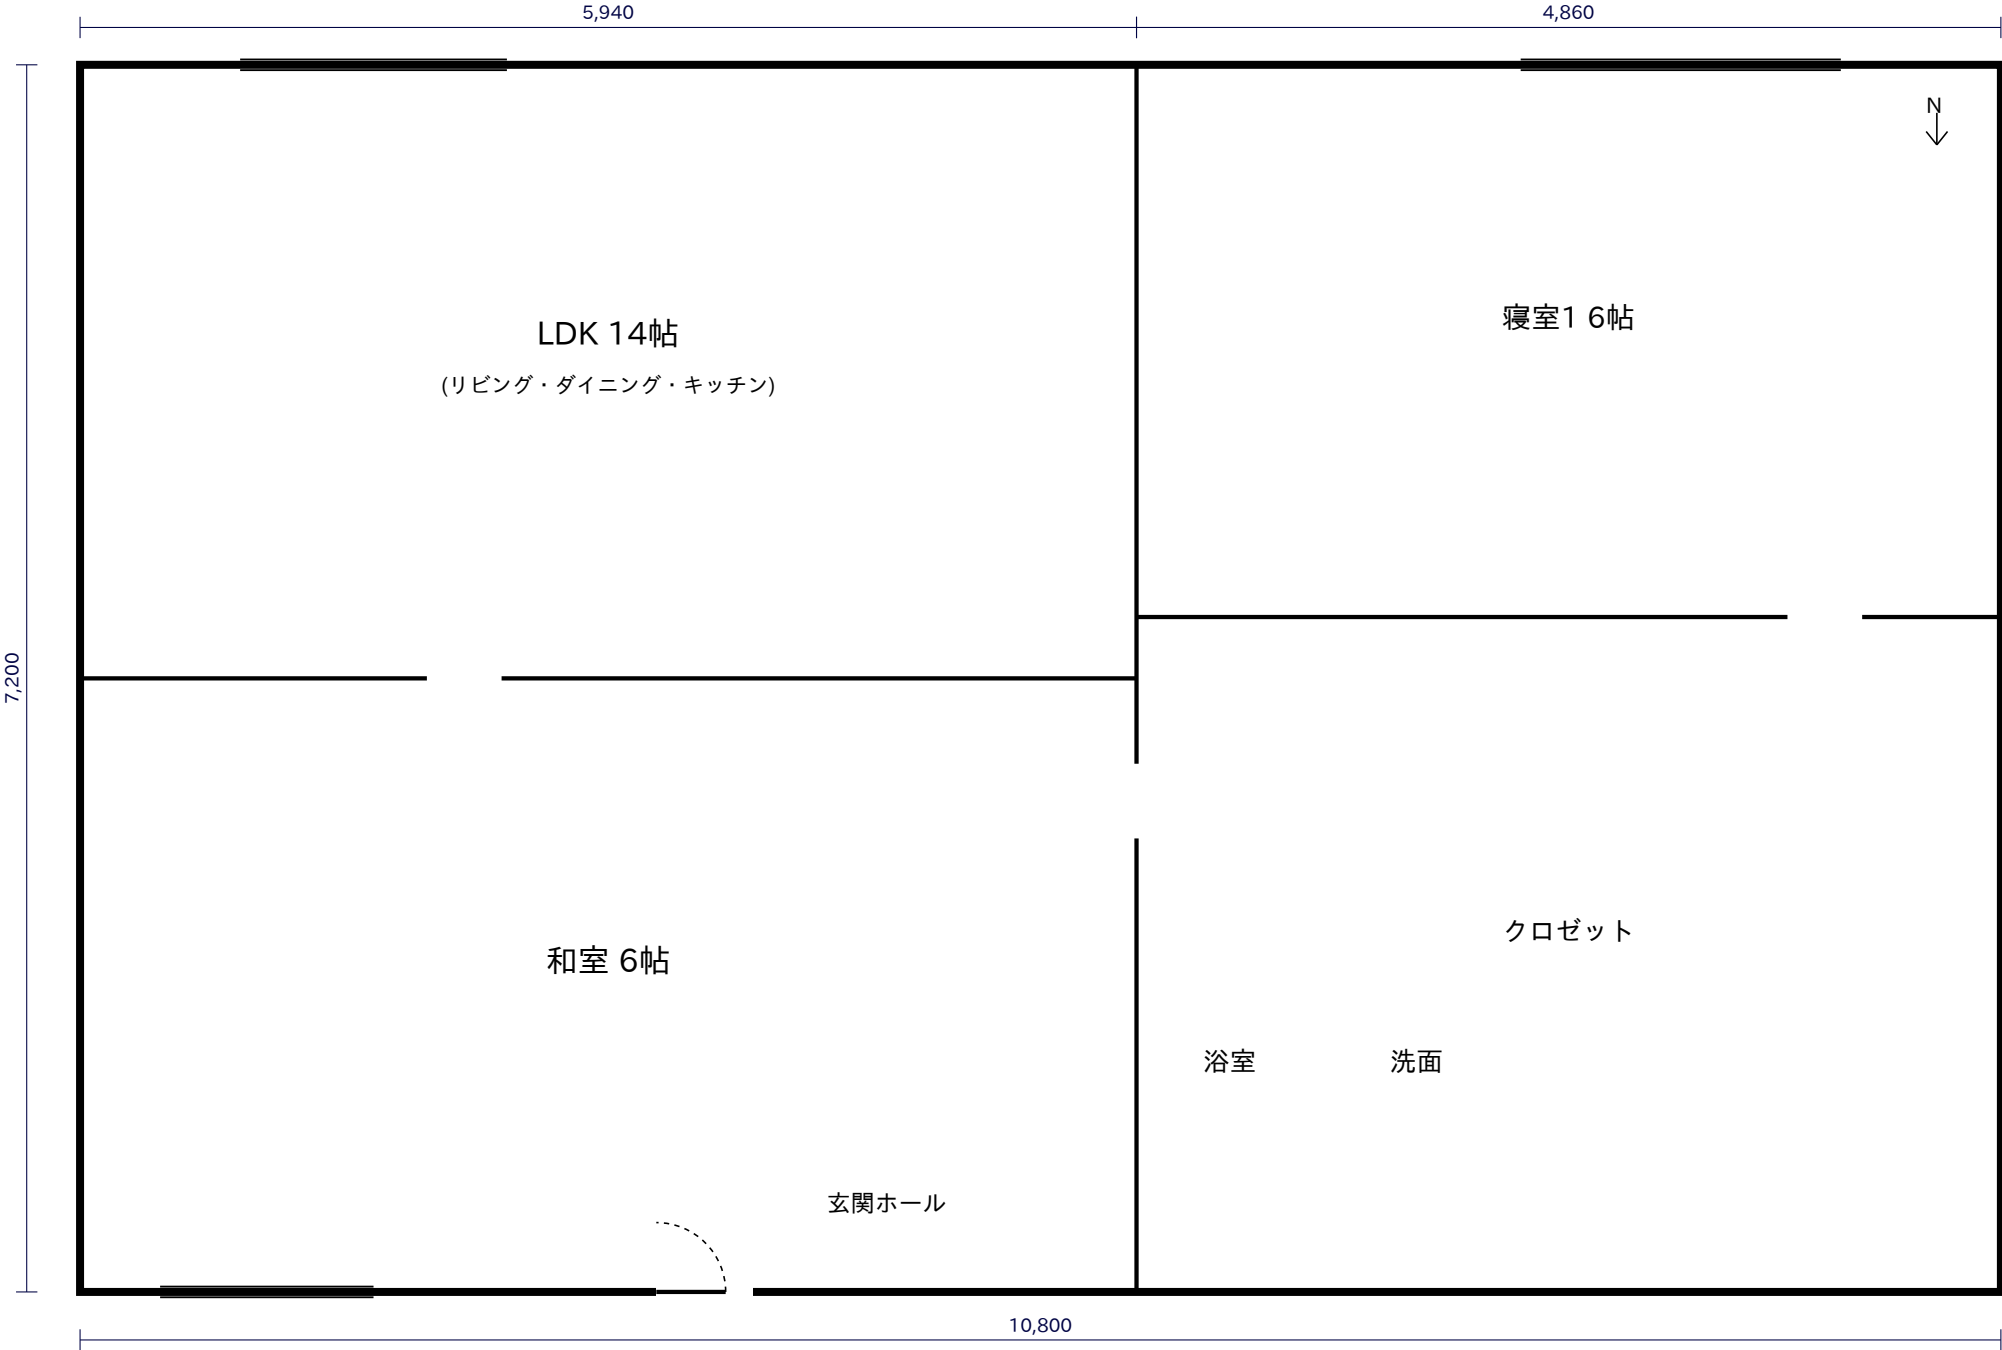

サンプル住宅 平面図 113号室

Rev.B 2026-05-01


縮尺: 1/100 単位: mm
作図: 設計室

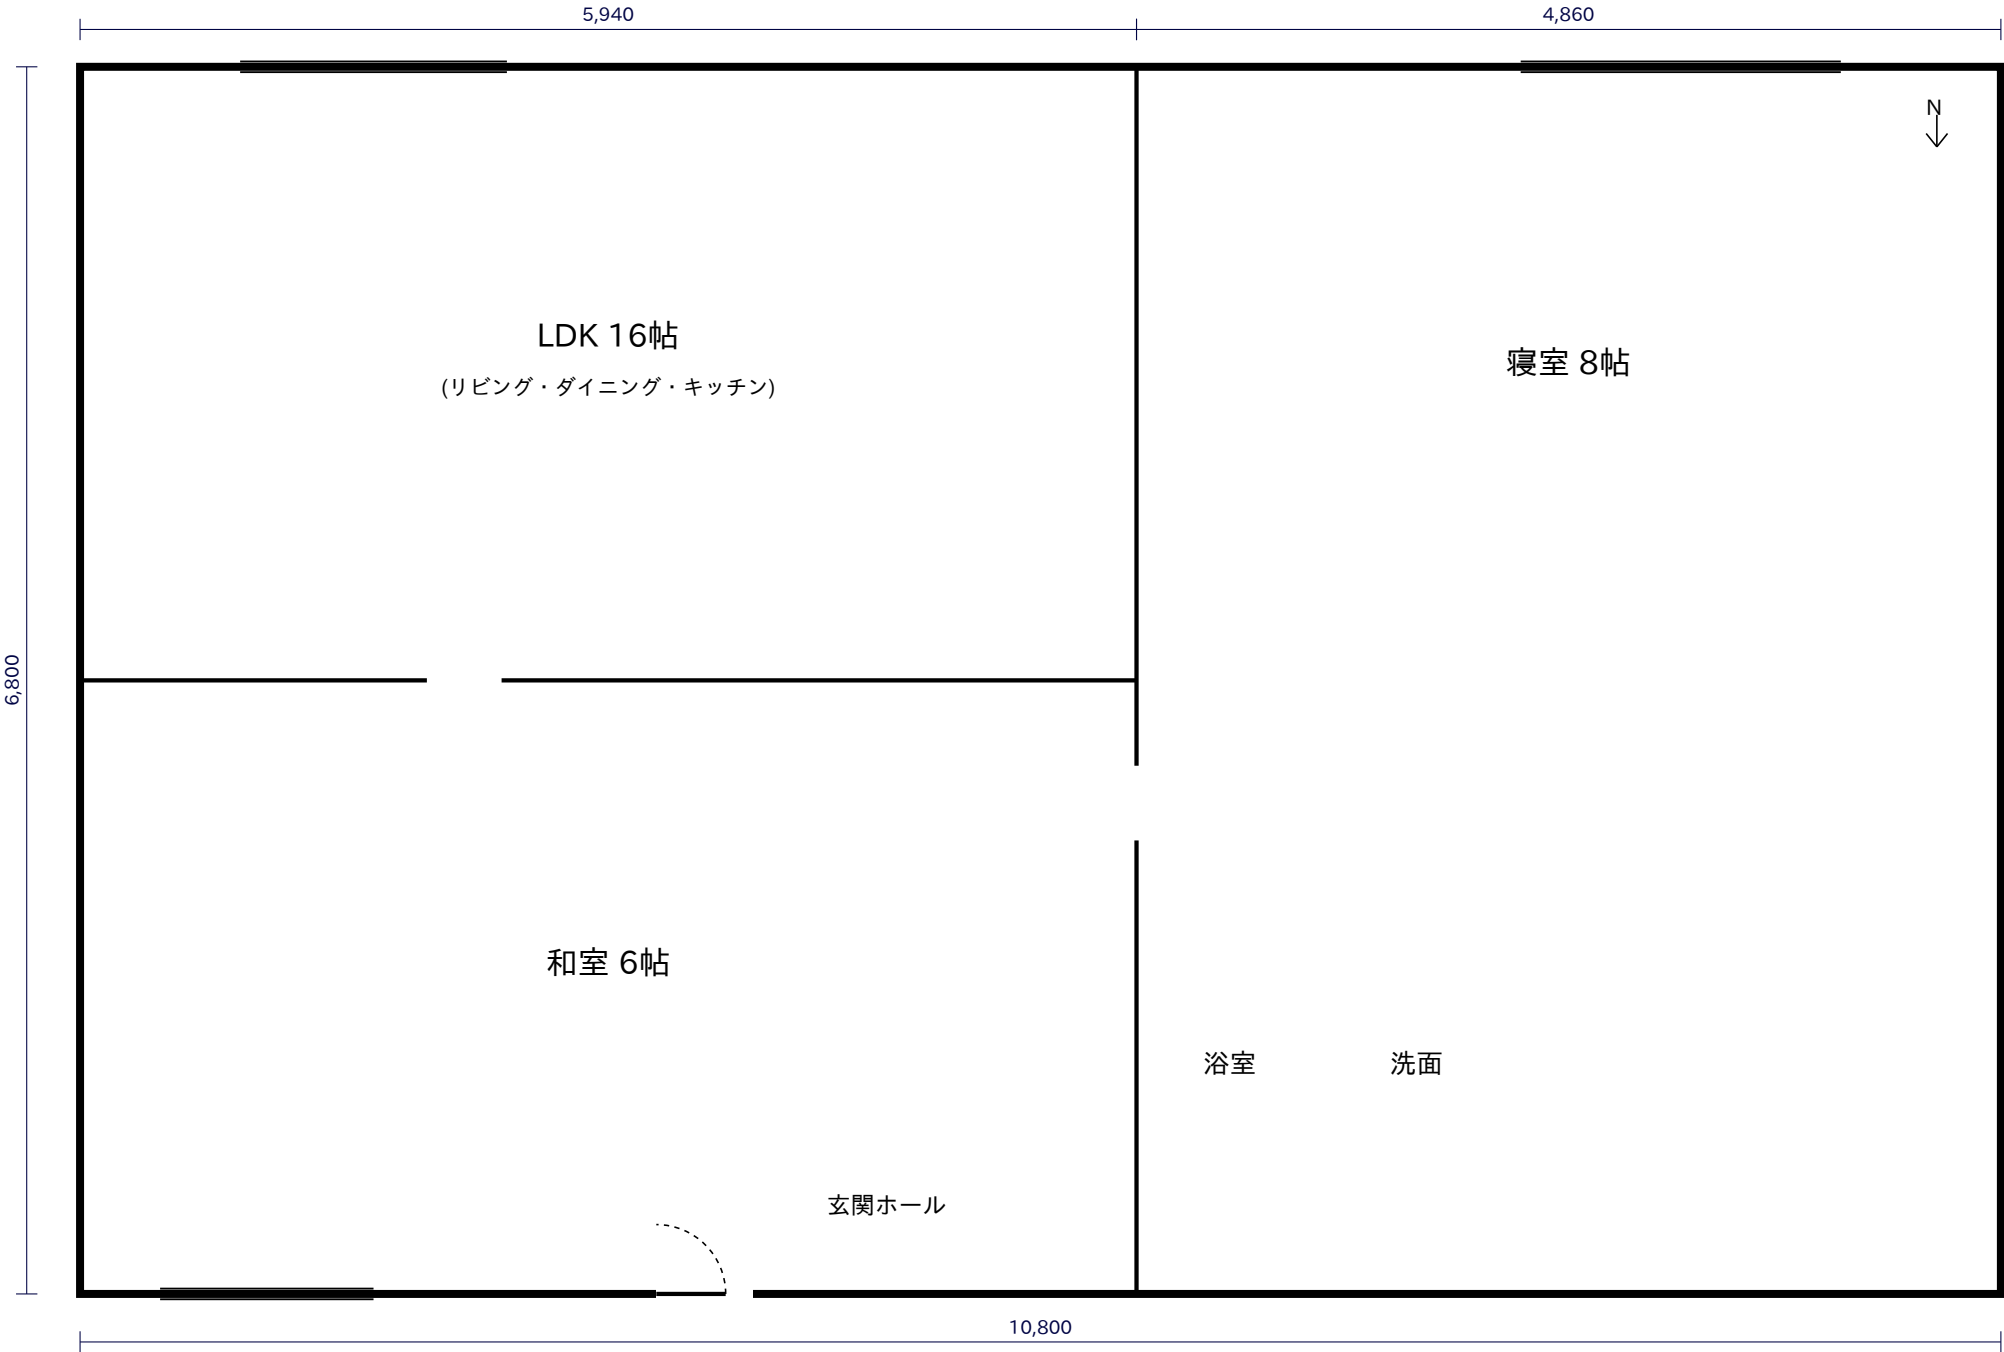

サンプル住宅 平面図 114号室

Rev.B 2026-05-01


縮尺: 1/100 単位: mm
作図: 設計室

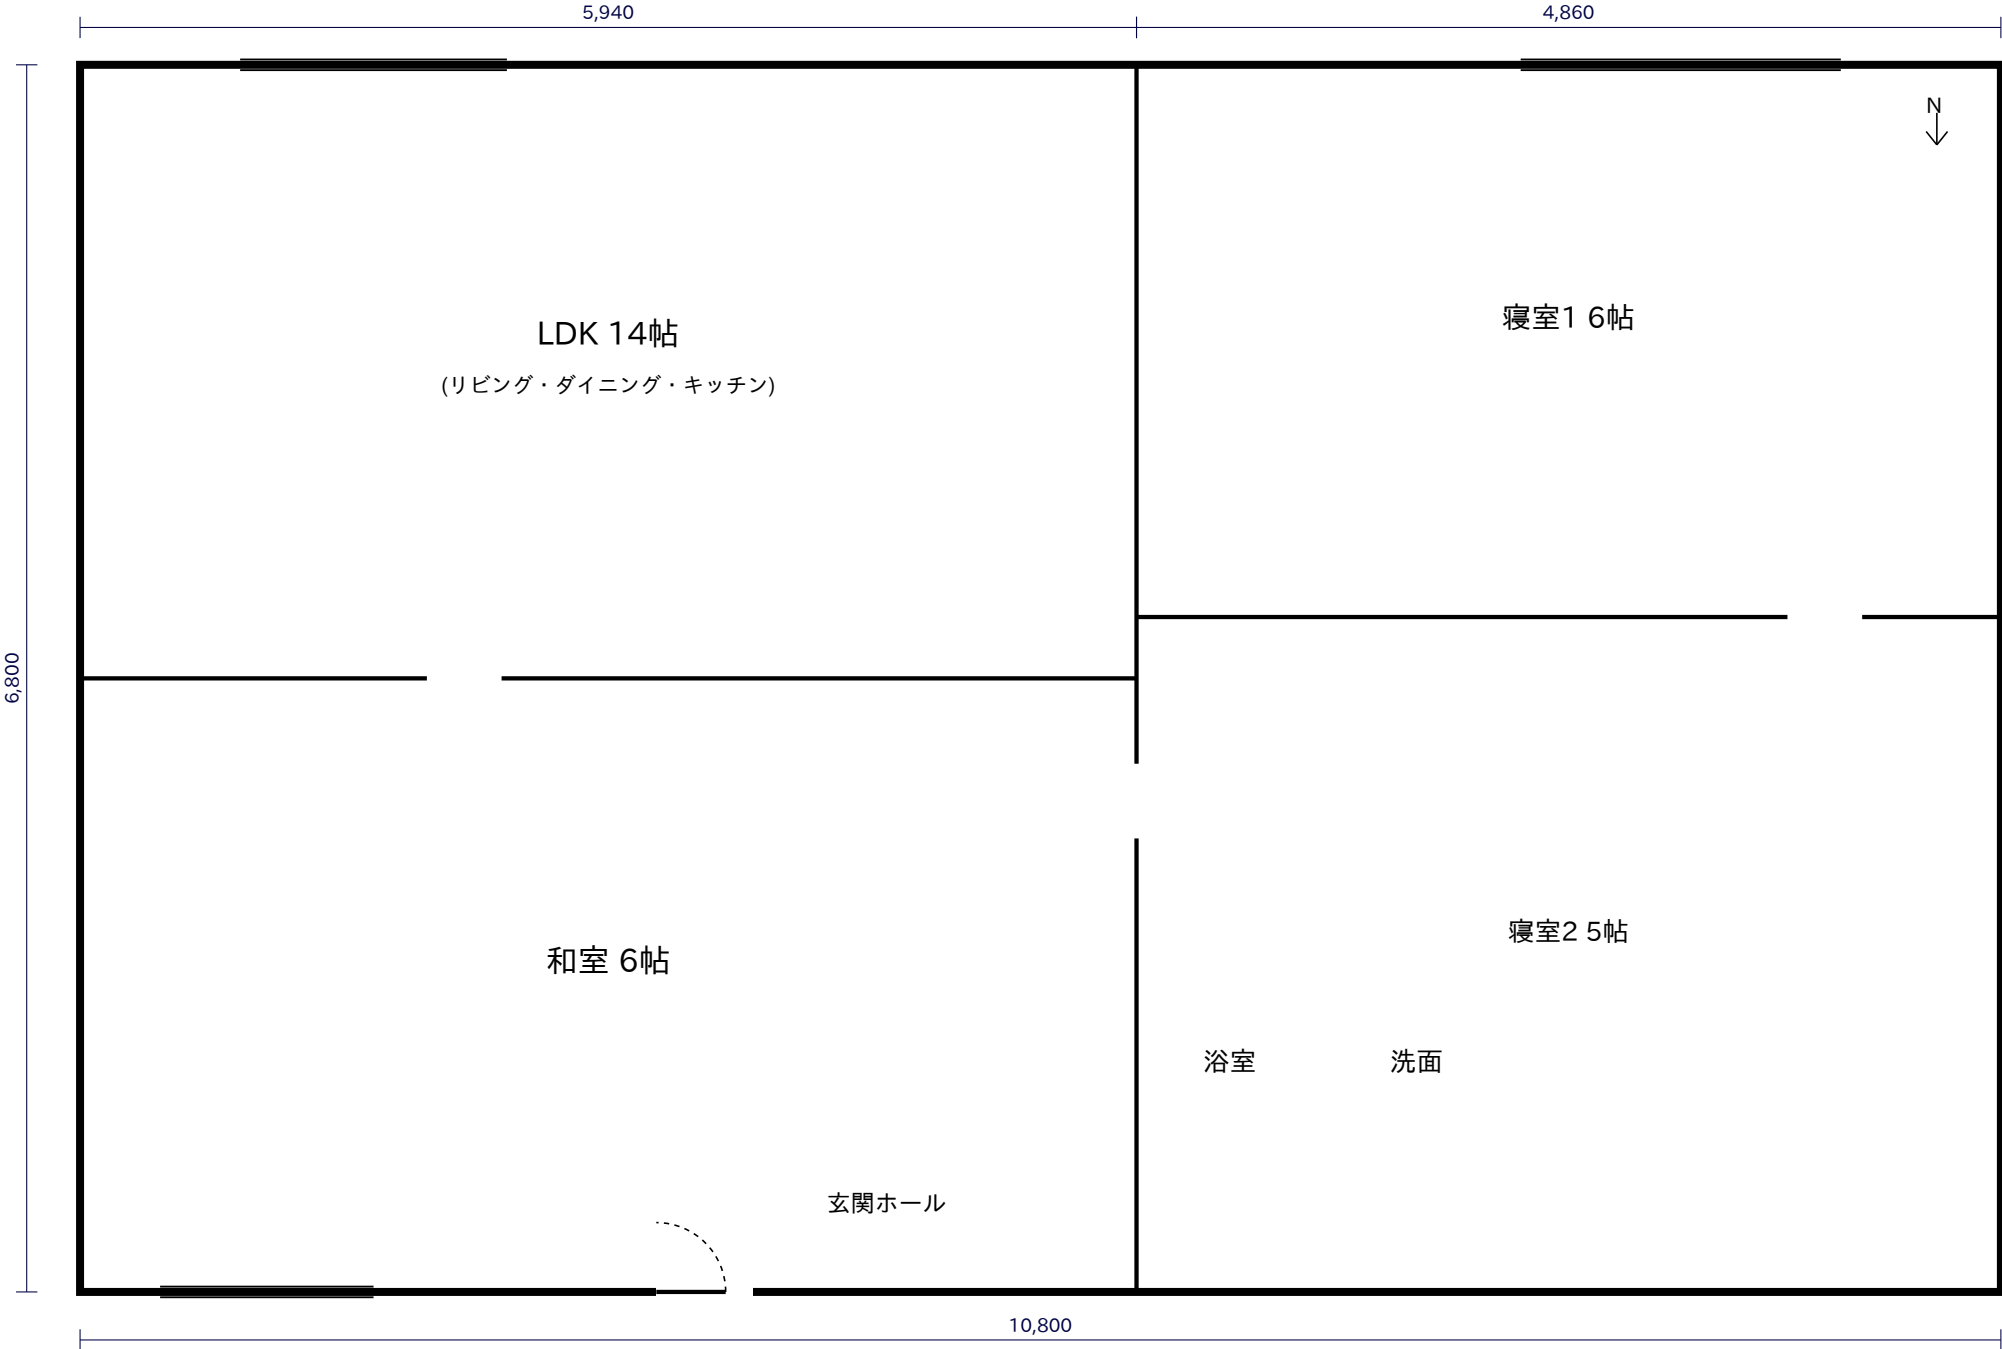

サンプル住宅 平面図 115号室

Rev.B 2026-05-01


縮尺: 1/100 単位: mm
作図: 設計室

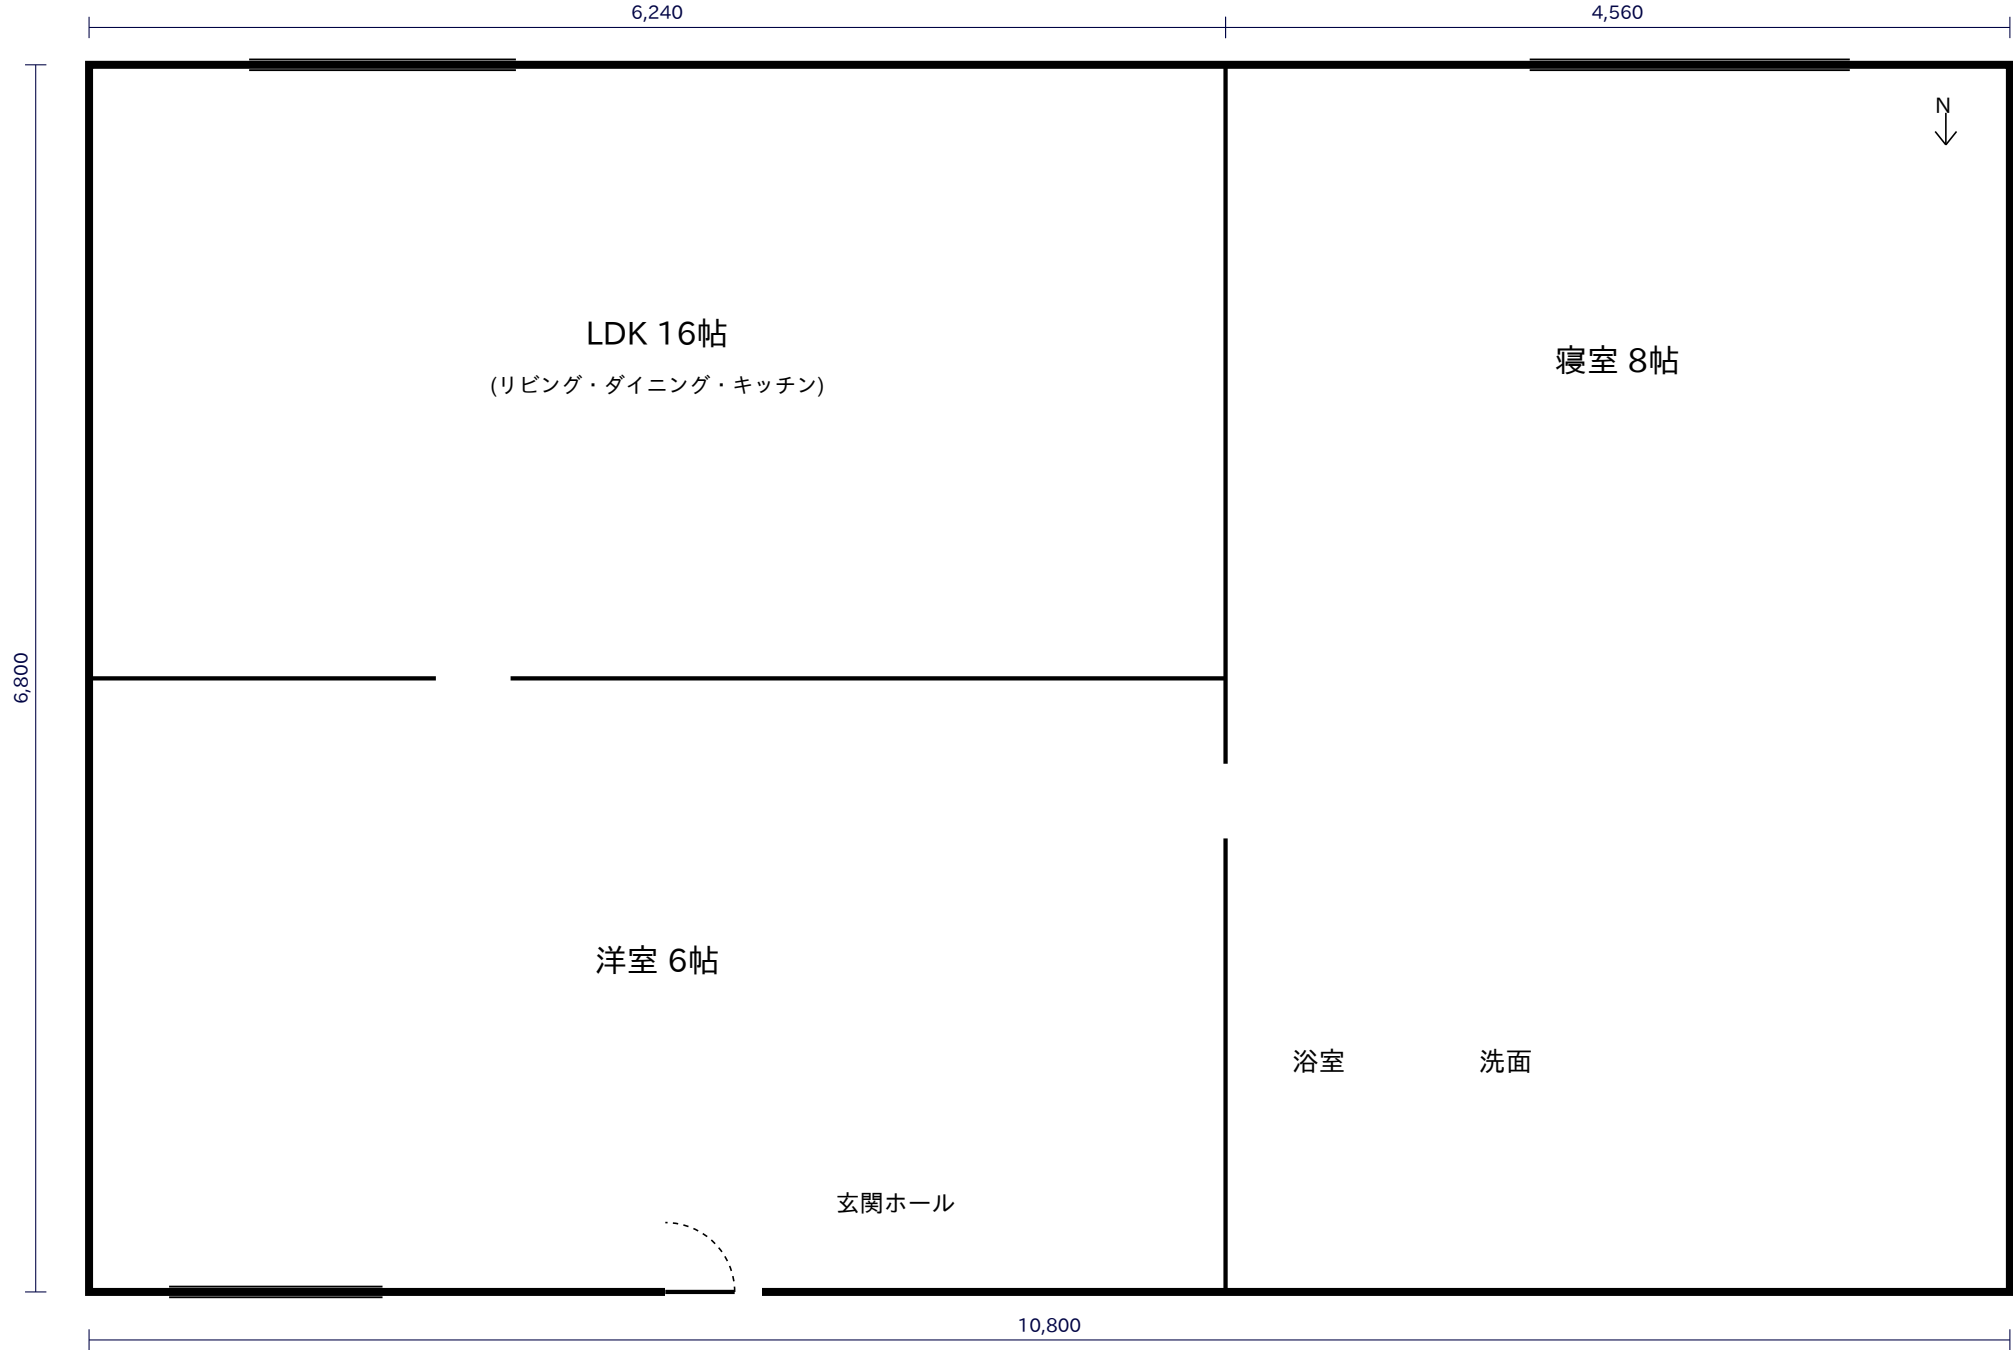

サンプル住宅 平面図 116号室

Rev.B 2026-05-01


縮尺: 1/100 単位: mm
作図: 設計室

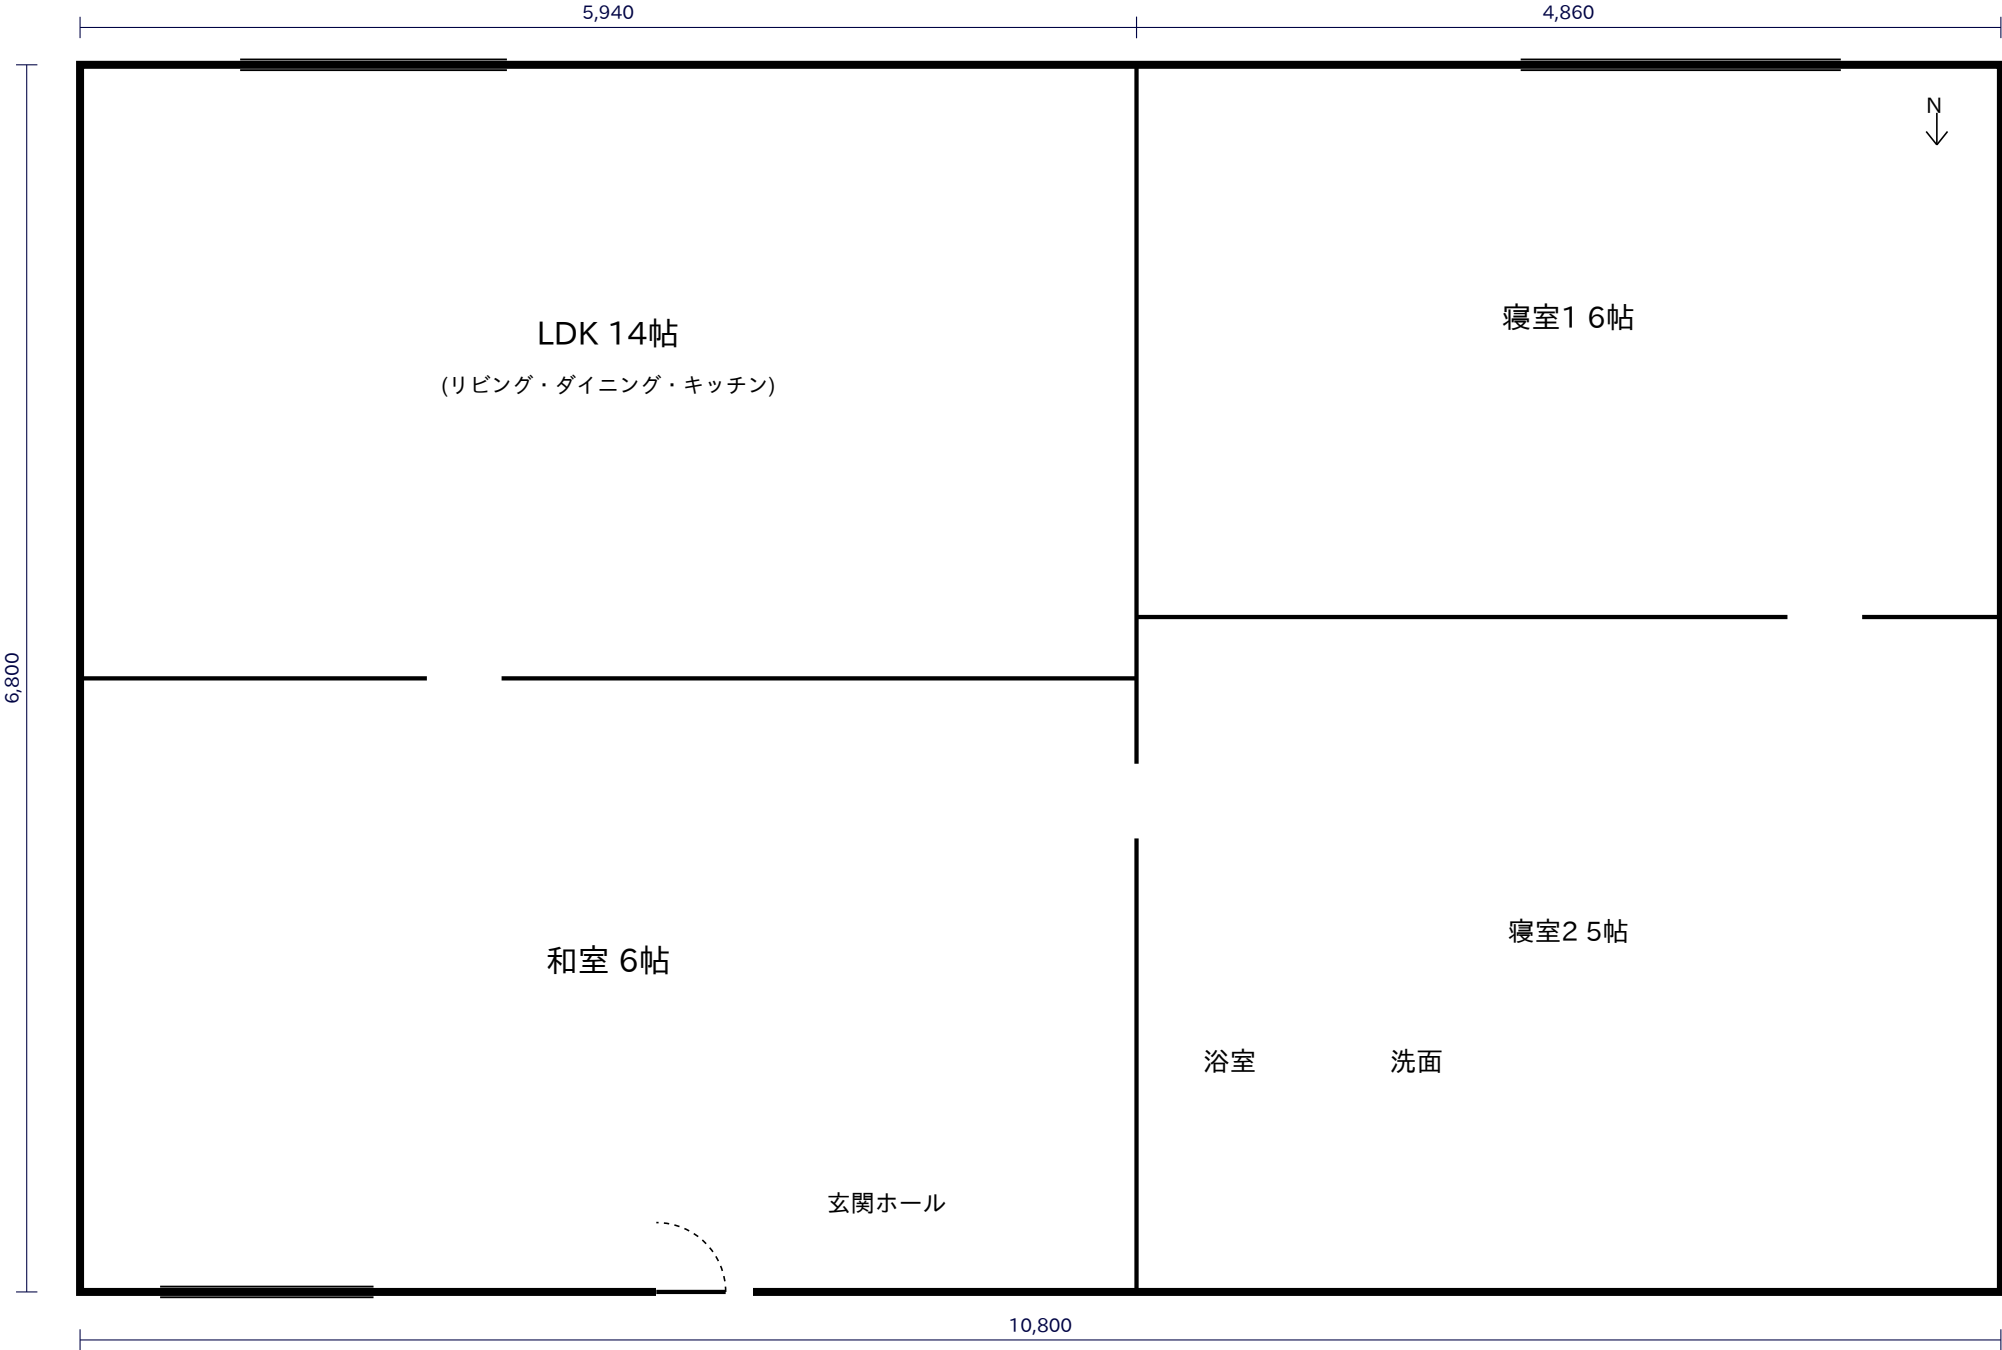

サンプル住宅 平面図 117号室

Rev.B 2026-05-01


縮尺: 1/100 単位: mm
作図: 設計室

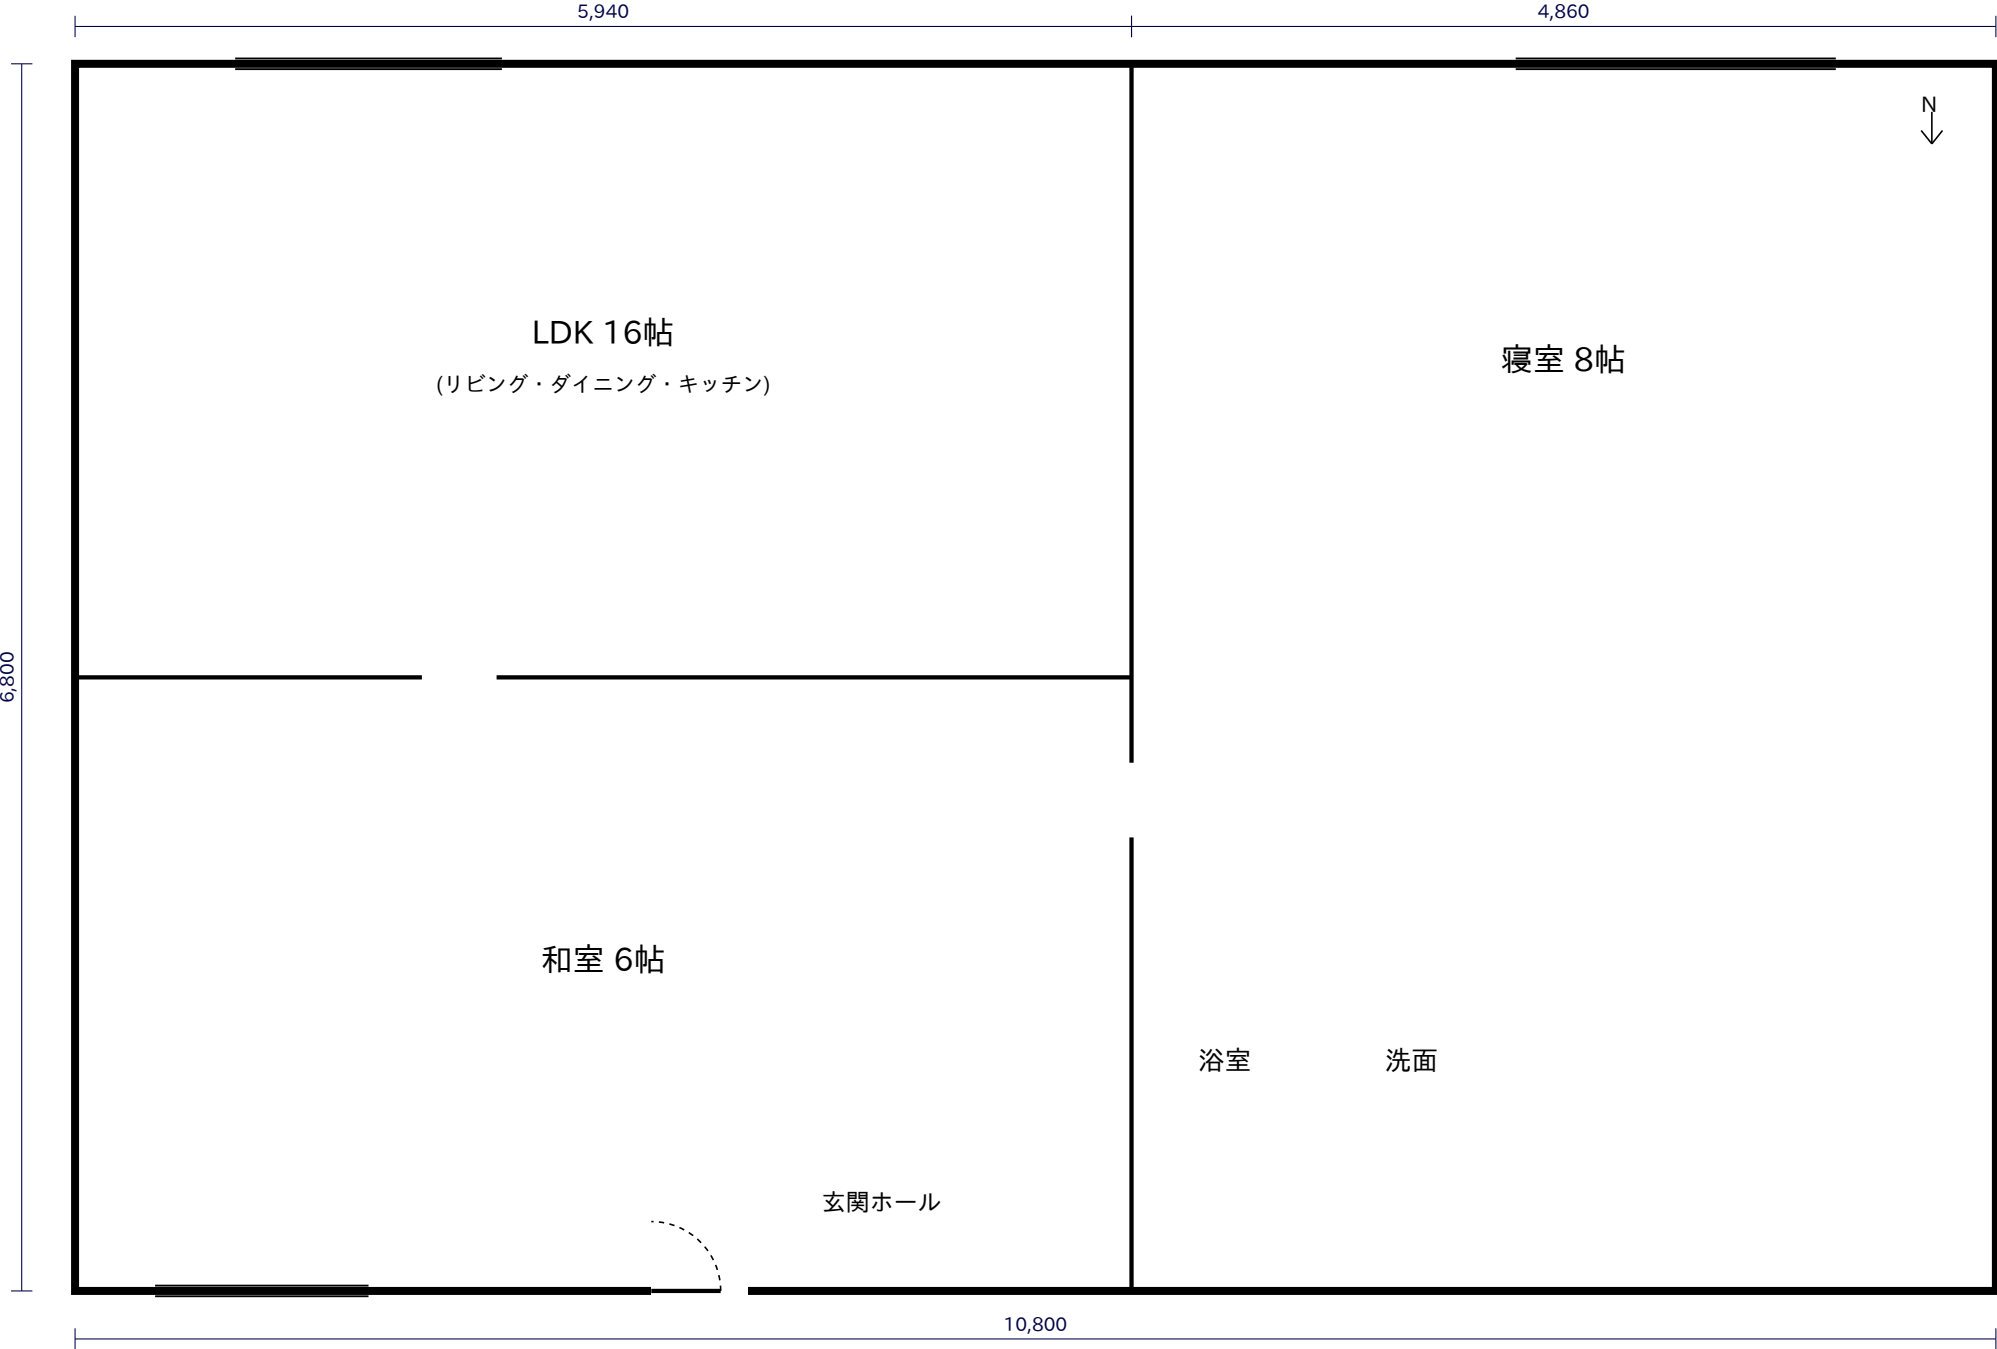

サンプル住宅 平面図 118号室

Rev.B 2026-05-01


縮尺: 1/100 単位: mm
作図: 設計室

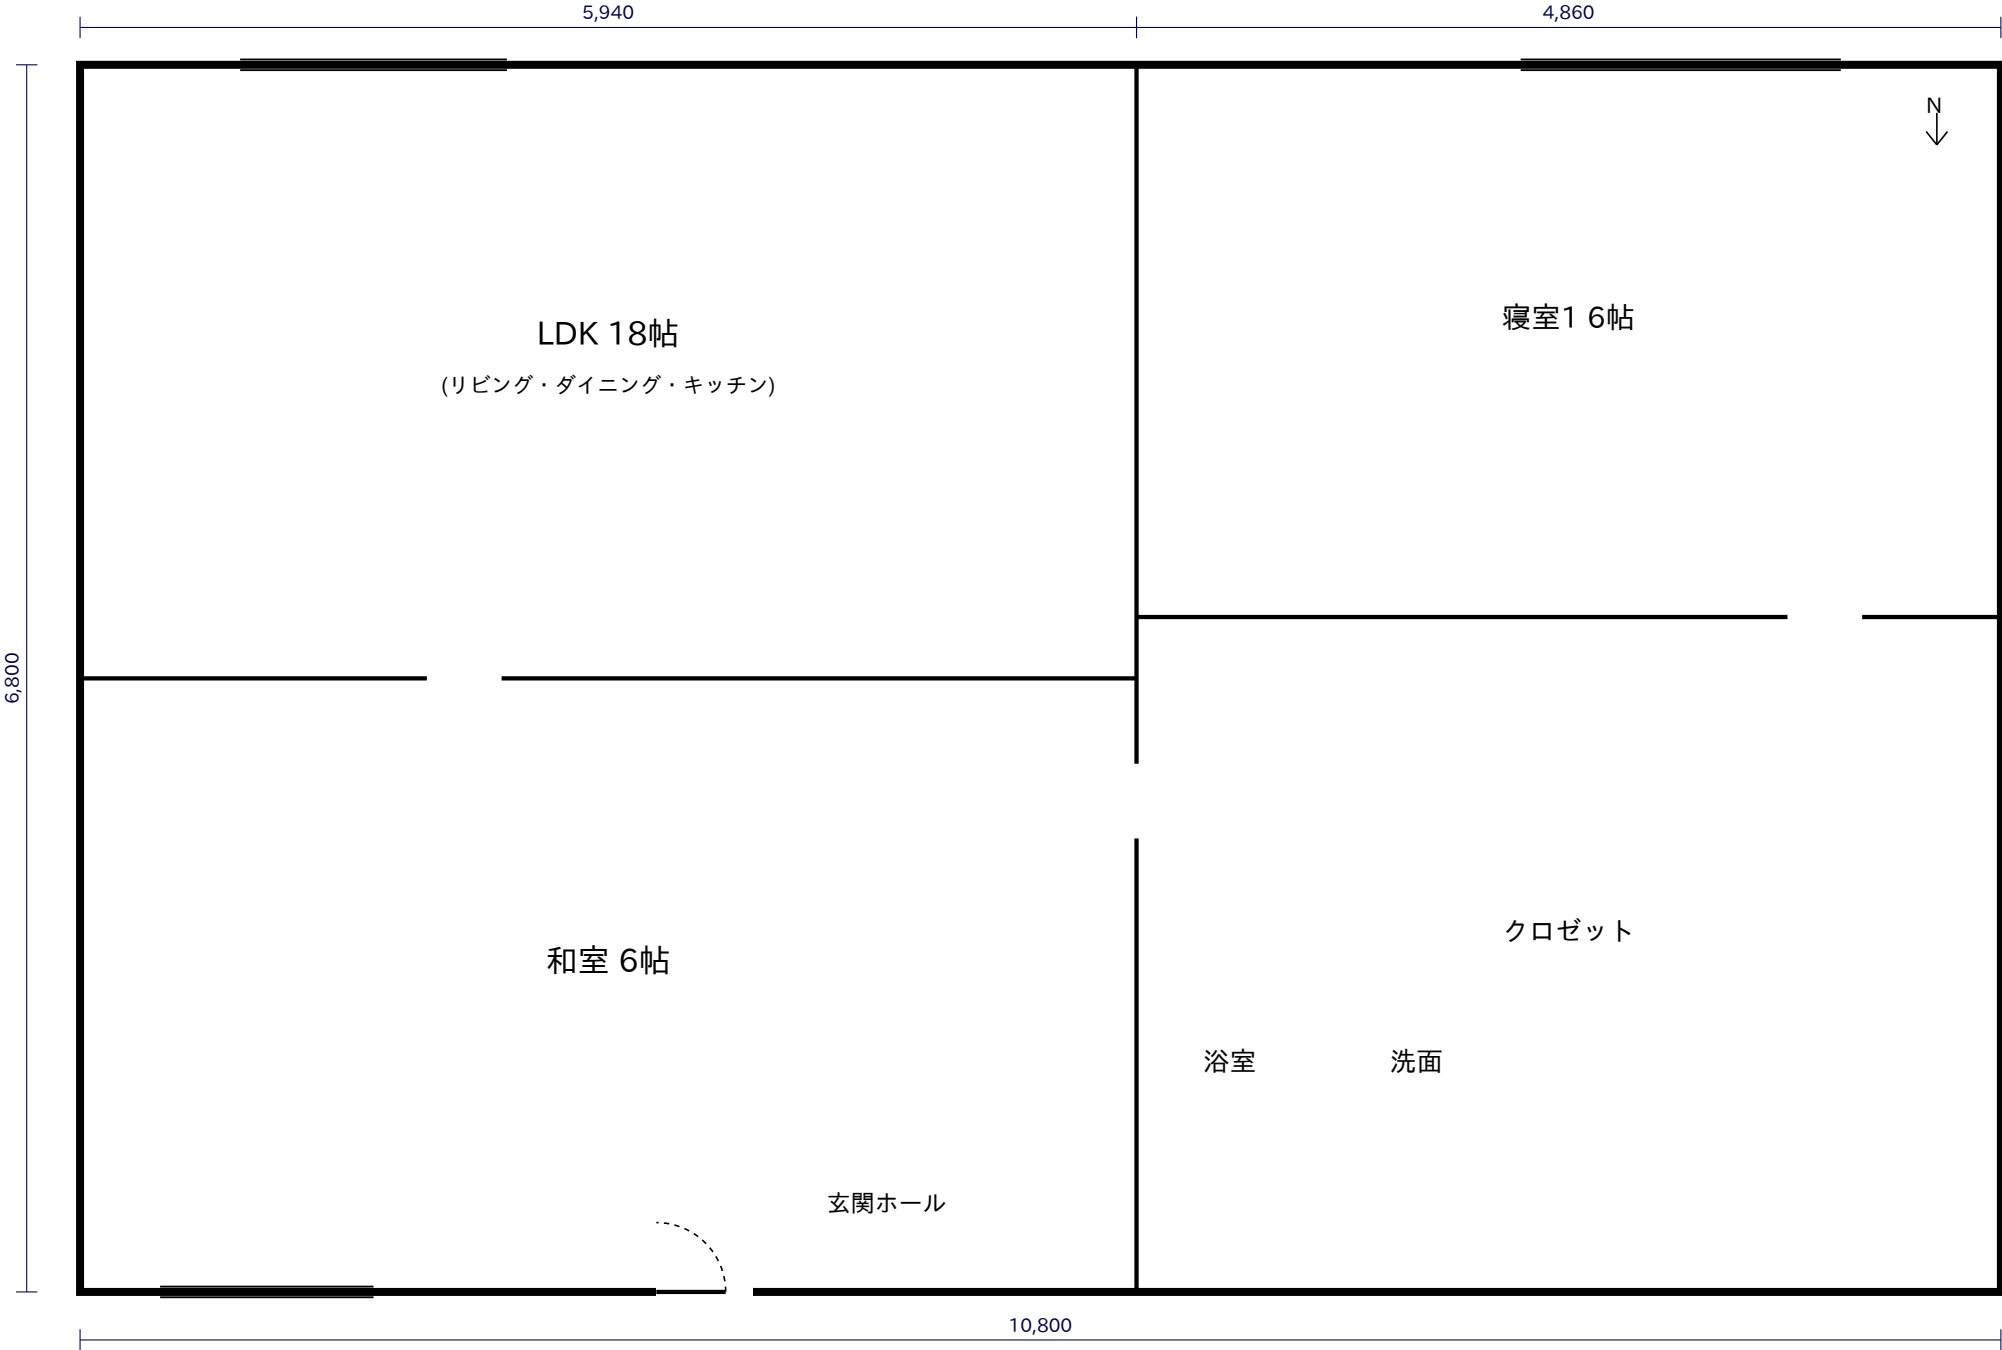

サンプル住宅 平面図 119号室

Rev.B 2026-05-01

縮尺: 1/100 単位: mm
作図: 設計室

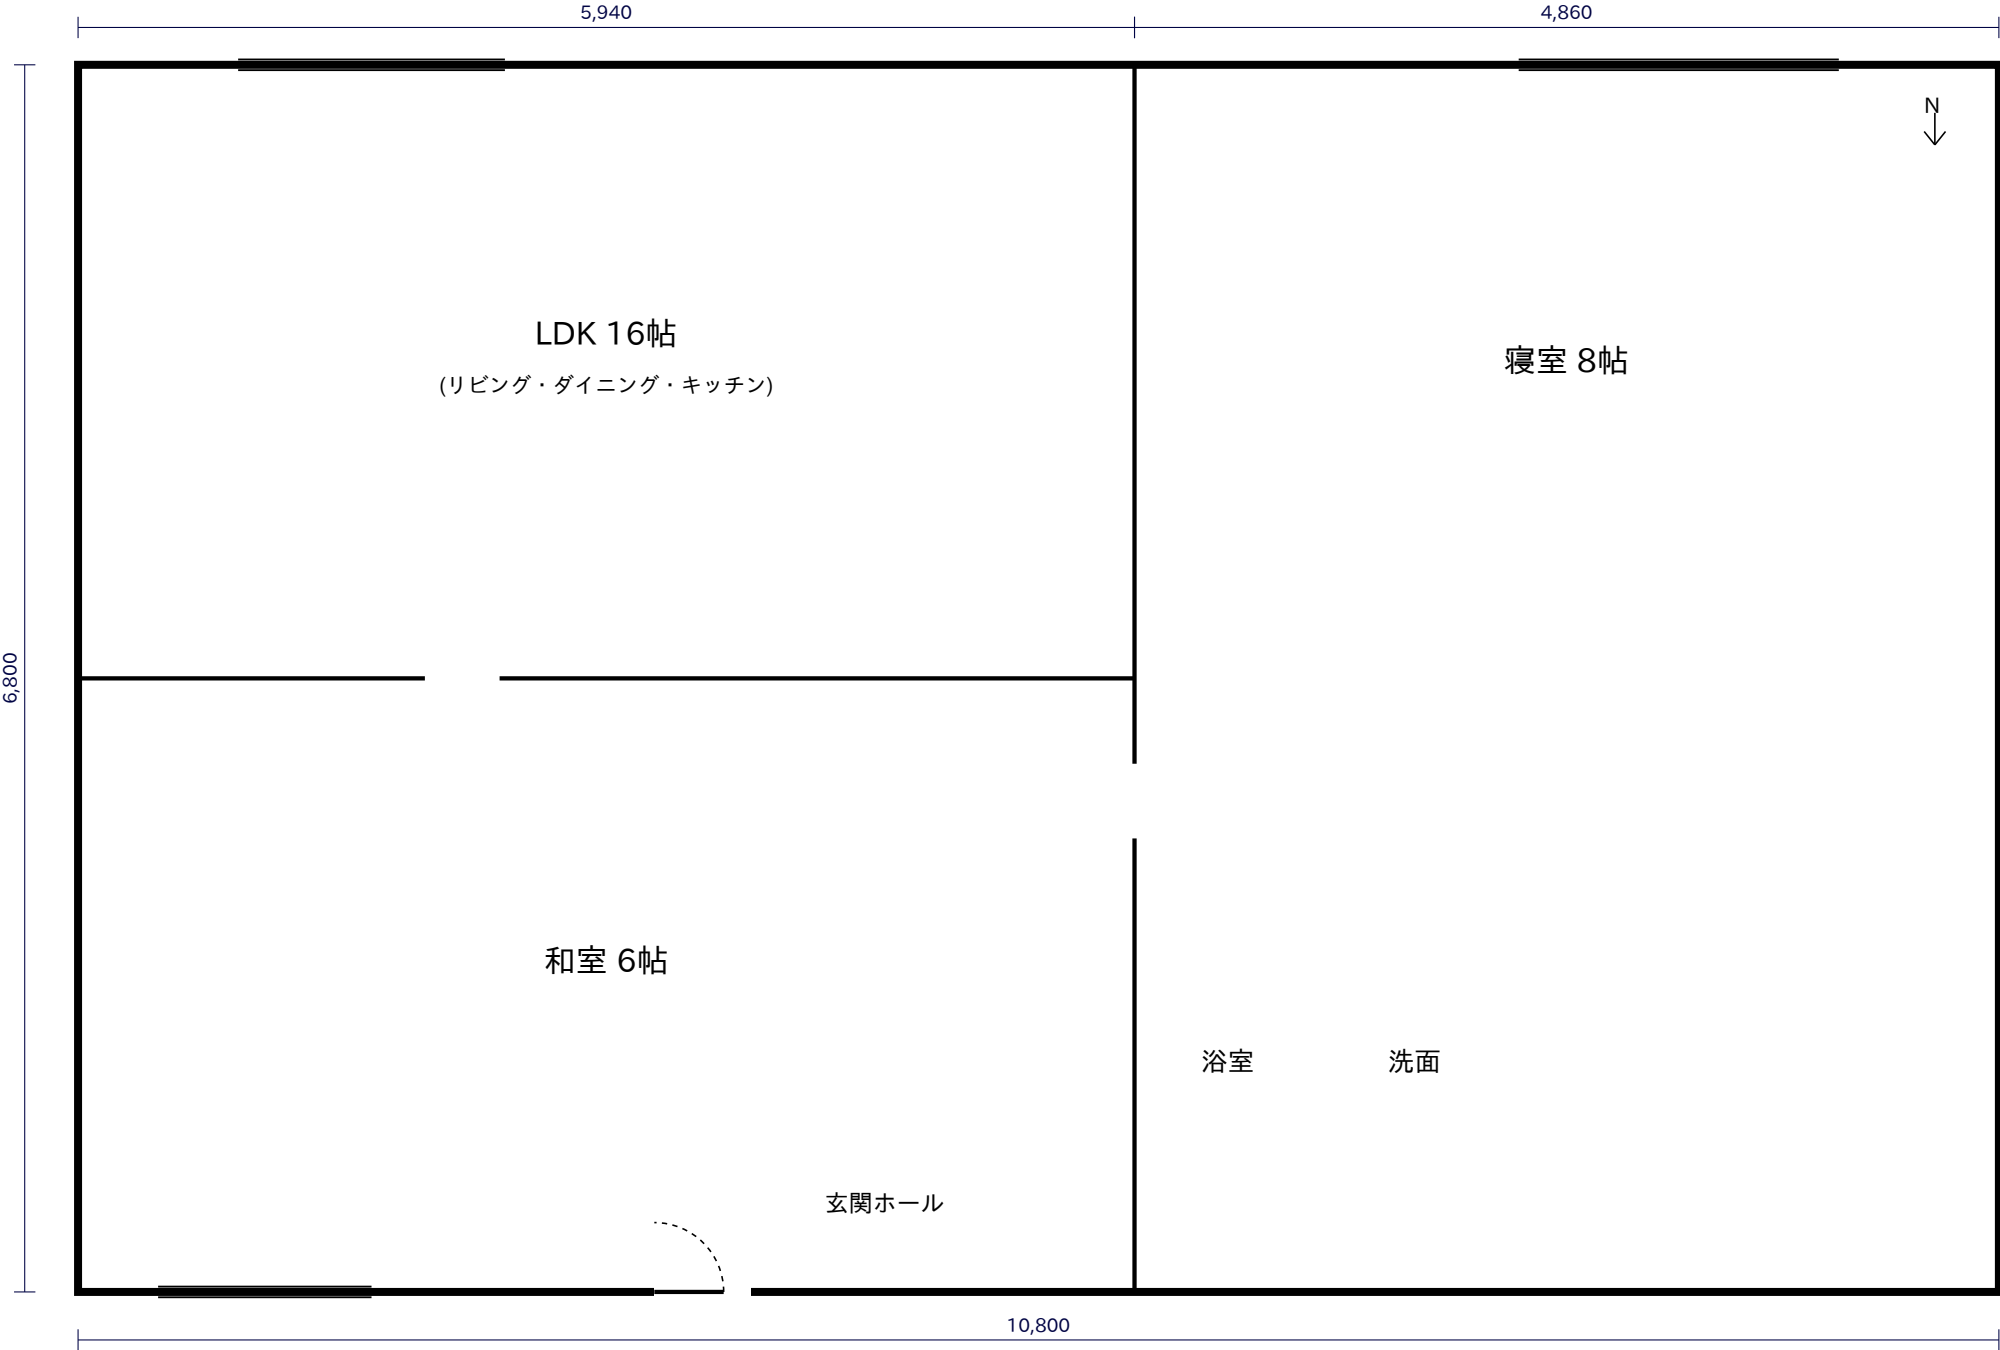

サンプル住宅 平面図 120号室

Rev.B 2026-05-01

縮尺: 1/100 単位: mm
作図: 設計室

