



■内装仕様										■内部造作部材・備品仕様														
部屋名									備 考		部位	メーカー	仕様・品番	色柄										
1階	床仕上げ		巾木・畳寄せ		壁仕上げ	天井仕上げ		廻縁	天井高さ	玄関三方枠:【ベリティス】しっくいホワイト														
玄関	【LIXIL】磁器質タイル パセオ 300□／厚9mm PSO-BR1 目地:外部ポーチに準ずる	【パナソニック】ベリティス スマート巾木(スカート無) H=30 しっくいホワイト	【サンゲツ】ビニールクロス SP-2508	【サンゲツ】ビニールクロス SP-2508	無	2565																		
土間収納	【LIXIL】磁器質タイル パセオ 300□／厚9mm PSO-BR1 目地:外部ポーチに準ずる	【パナソニック】ベリティス スマート巾木(スカート無) H=30 しっくいホワイト	【サンゲツ】ビニールクロス SP-2508	【サンゲツ】ビニールクロス SP-2508	無	2400																		
1階ホール	【パナソニック】トリプルコート/厚12mm シルバーオーク柄(ラステック)	【パナソニック】ベリティス スマート巾木(スカート無) H=30 しっくいホワイト	【サンゲツ】ビニールクロス SP-2508	【サンゲツ】ビニールクロス SP-2508	無	2400																		
LDK	【パナソニック】トリプルコート/厚12mm シルバーオーク柄(ラステック)	【パナソニック】ベリティス スマート巾木(スカート無) H=30 しっくいホワイト	【サンゲツ】ビニールクロス SP-2508	【サンゲツ】ビニールクロス SP-2508	無	2400	間接照明																	
洗面 コーナー	【パナソニック】トリプルコート/厚12mm シルバーオーク柄(ラステック)	【パナソニック】ベリティス スマート巾木(スカート無) H=30 しっくいホワイト	【サンゲツ】ビニールクロス SP-2508	【サンゲツ】ビニールクロス SP-2508	無	2400																		
1階トイレ	【サンゲツ】クッションフロア厚1.8mm HM12041	【パナソニック】ベリティス スマート巾木(スカート無) H=30 しっくいホワイト	【サンゲツ】ビニールクロス SP-2508	【サンゲツ】ビニールクロス SP-2508	無	2400	間接照明																	
階段室	【朝日ウッドテック】エアリス-α 2Pタイプ/厚12mm 踏み板 ミストグレー 蹴込み板・側板 クロ、側板ホワイト		【サンゲツ】ビニールクロス SP-2508	【サンゲツ】ビニールクロス SP-2508	無	—																		
脱衣所 ランドリールーム	【サンゲツ】フロア-タイル張り IS-2009	【パナソニック】ベリティス スマート巾木(スカート無) H=30 しっくいホワイト	【サンゲツ】ビニールクロス SP-2508	【サンゲツ】ビニールクロス SP-2508	無	2400	浴室三方枠:ホワイト JOTO 開戸SP-8003																	
WIC	【パナソニック】トリプルコート/厚12mm シルバーオーク柄(ラステック)	【パナソニック】ベリティス スマート巾木(スカート無) H=30 しっくいホワイト	【サンゲツ】ビニールクロス SP-2508	【サンゲツ】ビニールクロス SP-2508	無	2400	下部全館空調																	
階段下 収納	【朝日ウッドテック】エアリス-α 2Pタイプ/厚12mm ミストグレー	【パナソニック】ベリティス スマート巾木(スカート無) H=30 しっくいホワイト	【サンゲツ】ビニールクロス SP-2508	【サンゲツ】ビニールクロス SP-2508	無	2400																		
2階	床仕上げ		巾木・畳寄せ		壁仕上げ	天井仕上げ		廻縁	天井高さ	玄関三方枠:【ベリティス】しっくいホワイト														
2階ホール	【朝日ウッドテック】エアリス-α 2Pタイプ/厚12mm ミストグレー	【パナソニック】ベリティス スマート巾木(スカート無) H=30 しっくいホワイト	【サンゲツ】ビニールクロス SP-2508	【サンゲツ】ビニールクロス SP-2508	無	2400																		
主寝室	【朝日ウッドテック】LiveNaturaMRX1本溝/厚12mm ブラックウォルナット	【パナソニック】ベリティス スマート巾木(スカート無) H=30 しっくいホワイト	【サンゲツ】ビニールクロス SP-2508	【サンゲツ】ビニールクロス SP-2508	無	2400	【アクセント】RE55761																	
WIC	【朝日ウッドテック】LiveNaturaMRX1本溝/厚12mm ブラックウォルナット	【パナソニック】ベリティス スマート巾木(スカート無) H=30 しっくいホワイト	【サンゲツ】ビニールクロス SP-2508	【サンゲツ】ビニールクロス SP-2508	無	2400																		
物置1	【朝日ウッドテック】LiveNaturaMRX1本溝/厚12mm ブラックウォルナット	【パナソニック】ベリティス スマート巾木(スカート無) H=30 しっくいホワイト	【サンゲツ】ビニールクロス SP-2508	【サンゲツ】ビニールクロス SP-2508	無	2400																		
物置2	【朝日ウッドテック】LiveNaturaMRX1本溝/厚12mm ブラックウォルナット	【パナソニック】ベリティス スマート巾木(スカート無) H=30 しっくいホワイト	【サンゲツ】ビニールクロス SP-2502	【サンゲツ】ビニールクロス SP-2502	無	2400	【アクセント】RE55621																	
洋室	【朝日ウッドテック】LiveNaturaMRX1本溝/厚12mm ブラックウォルナット	【パナソニック】ベリティス スマート巾木(スカート無) H=30 しっくいホワイト	【サンゲツ】ビニールクロス SP-2508	【サンゲツ】ビニールクロス SP-2508	無	2400																		
同上 クローゼット	【朝日ウッドテック】LiveNaturaMRX1本溝/厚12mm ブラックウォルナット	【パナソニック】ベリティス スマート巾木(スカート無) H=30 しっくいホワイト	【サンゲツ】ビニールクロス SP-2508	【サンゲツ】ビニールクロス SP-2508	無	2400																		
廊下収納	【朝日ウッドテック】エアリス-α 2Pタイプ/厚12mm ミストグレー	【パナソニック】ベリティス スマート巾木(スカート無) H=30 しっくいホワイト	【サンゲツ】ビニールクロス SP-2508	【サンゲツ】ビニールクロス SP-2508	無	2400																		
2階トイレ	【サンゲツ】クッションフロア厚1.8mm HM12091	【パナソニック】ベリティス スマート巾木(スカート無) H=30 しっくいホワイト	【サンゲツ】ビニールクロス SP-2508	【サンゲツ】ビニールクロス SP-2508	無	2400	面台:PY																	
※特記無き限り、収納・クローゼットの壁・天井仕上げは前室に準ずる。					施主様	営業	工事	設計部長	設計		PROJ. NO	PROJ. TITLE 犬丸和也様・犬丸梨香 様邸新築工事												
※ビニクロスは経年劣化により壁紙が縮んだり下地の本木が湿気や乾燥で継ぎ目が空き隙間が生じることがあります																								
※1階ハイドアは設定天井高さより天井になる場合などについては、H2400未満へサイズ変更となります。																								
															DATE 2026.04.25	DWG. TITLE 仕様書-2		SCALE —	DWG. NO. A-02					
										超暖Q3 全館空調 長期優良住宅														

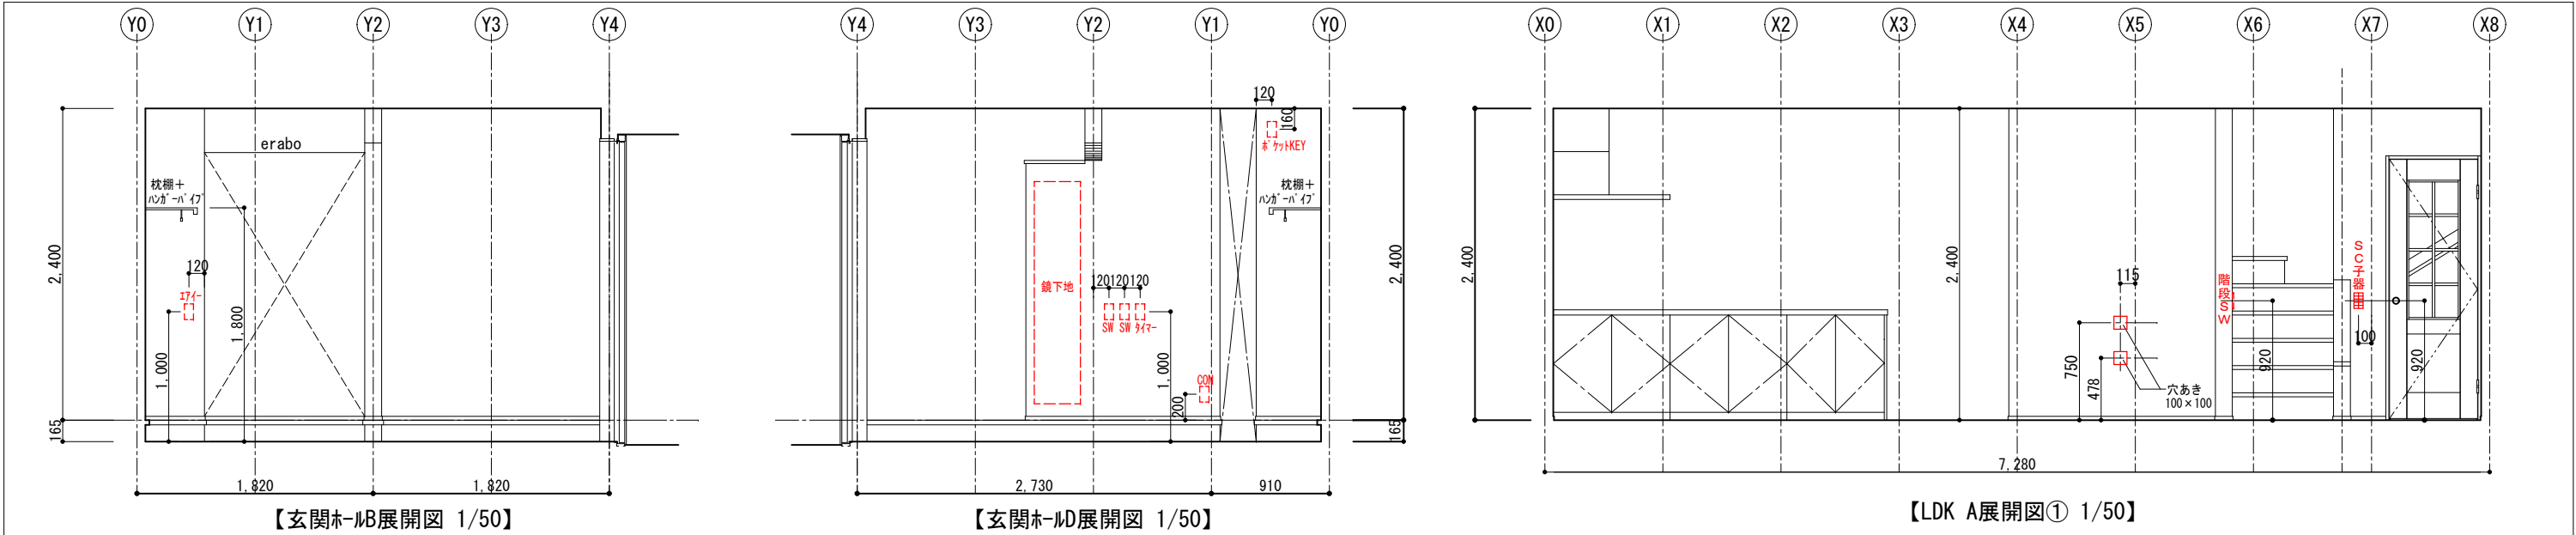

【玄関-ルB展開図 1/50】

【玄関-ルD展開図 1/50】


【LDK A展開図① 1/50】

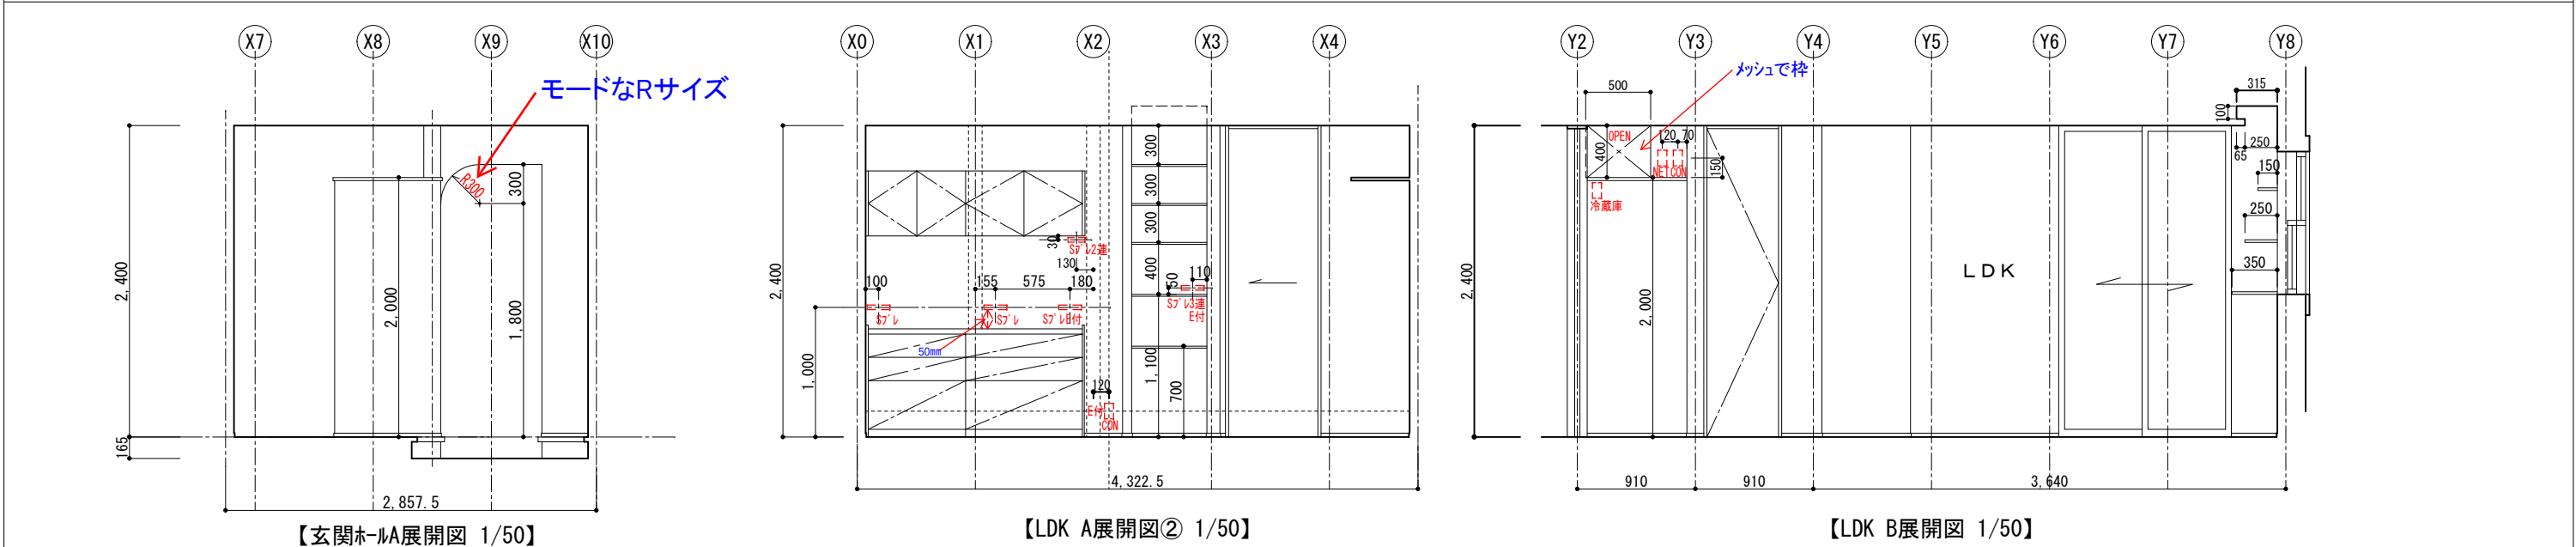

【玄関-ルA展開図 1/50】

【LDK A展開図② 1/50】


【LDK B展開図 1/50】

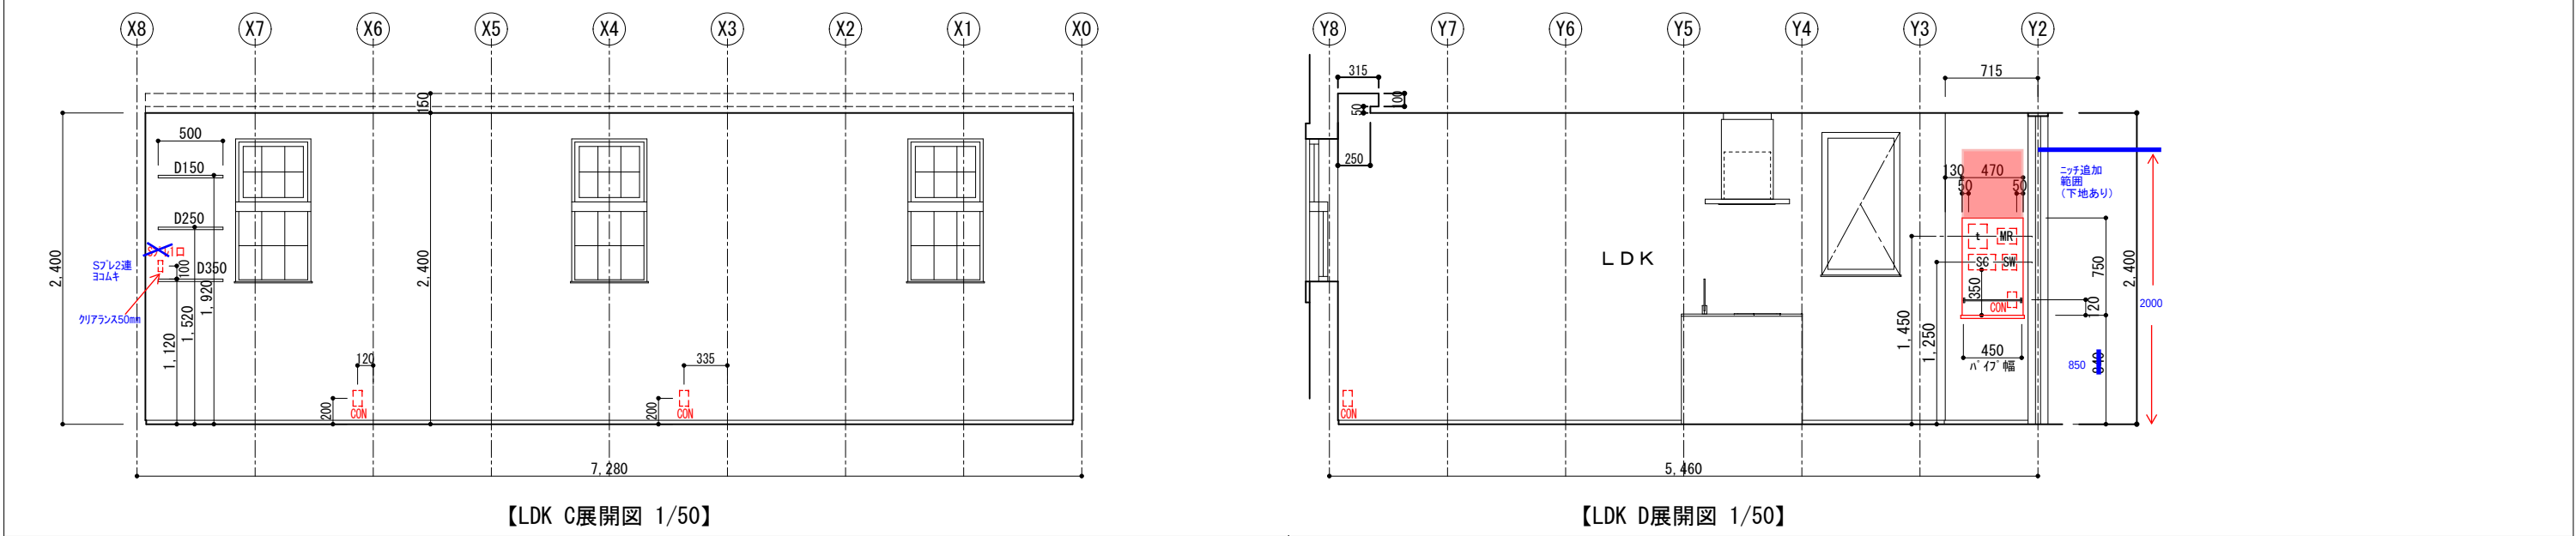


【LDK C展開図 1/50】

【LDK D展開図 1/50】


						▲■● ARCHI HL.	PROJ. NO	PROJ. TITLE 犬丸 和也様・犬丸 梨香様邸新築工事		超暖G3 長期優良住宅
							DATE 2026/04/26	DWG. TITLE 展開図①	SCALE A3:1/50	DWG. NO. A-11

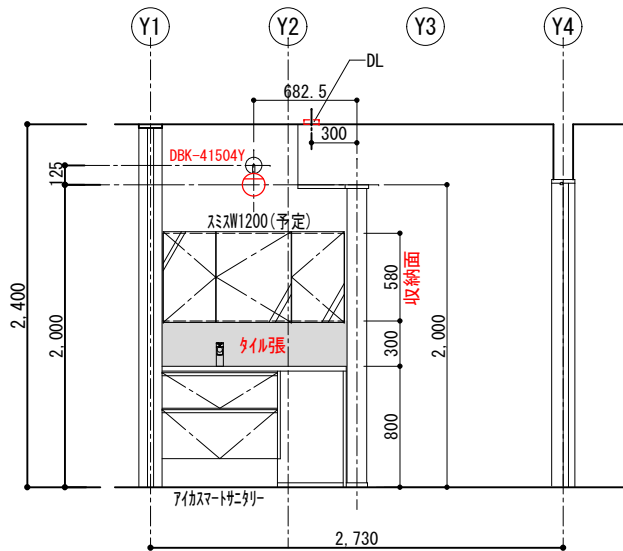


【洗面コーナーB展開図 1/50】

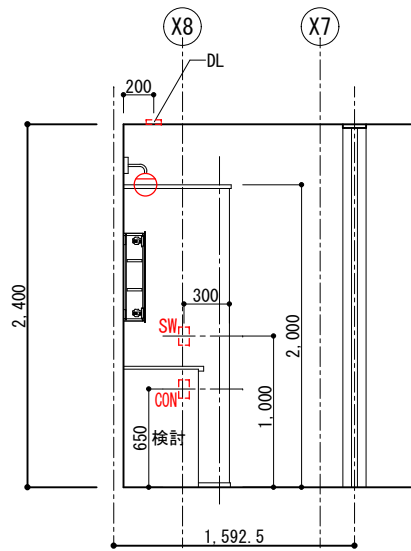


【洗面コーナーC展開図 1/50】

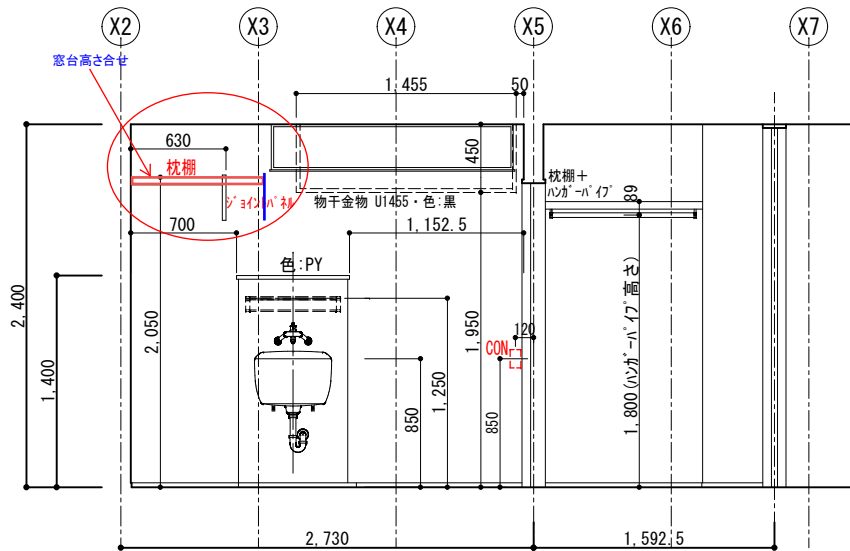


【脱衣所・ランドリールーム A展開図 1/50】

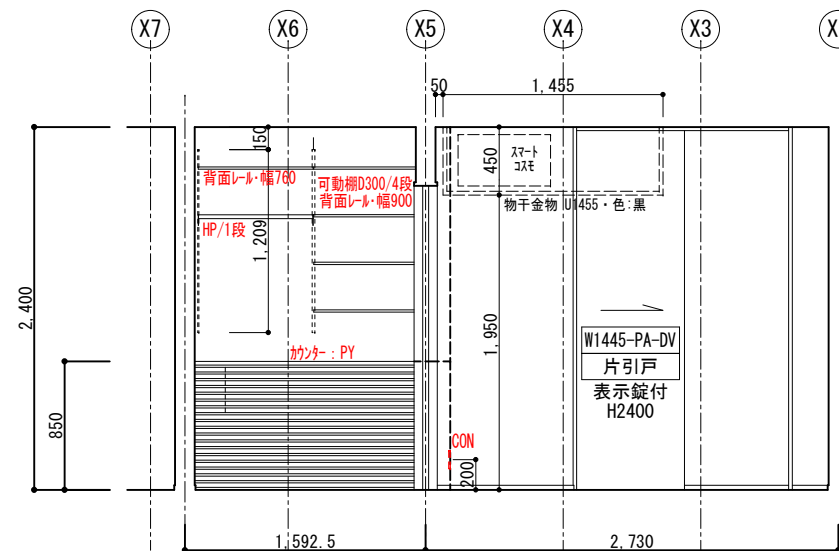


【脱衣所・ランドリールーム C展開図 1/50】

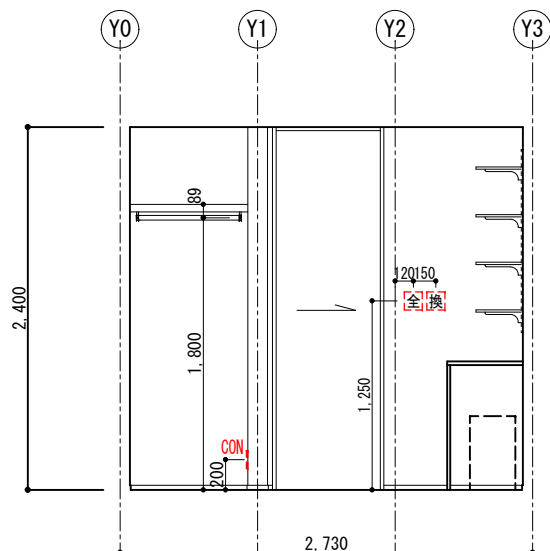


【脱衣所・ランドリールーム D展開図 1/50】

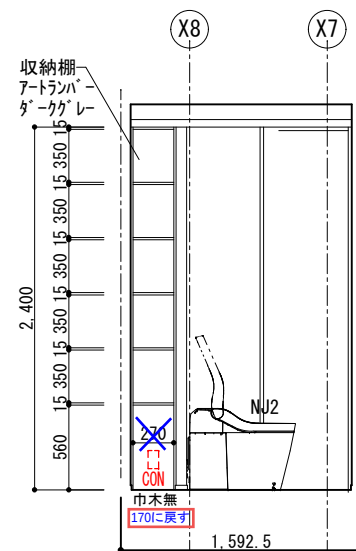


【トイレ D展開図 1/50】

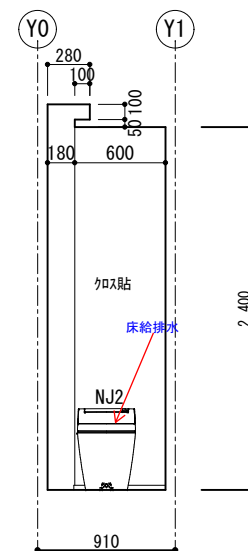


【トイレ B展開図 1/50】

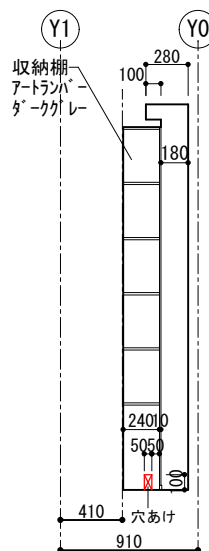


【トイレ C展開図 1/50】

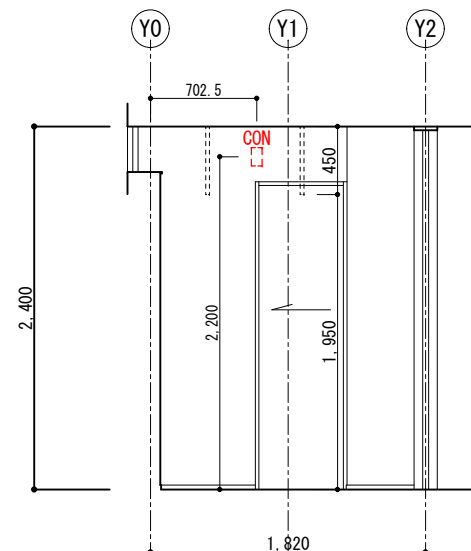


【LDK D展開図 1/50】

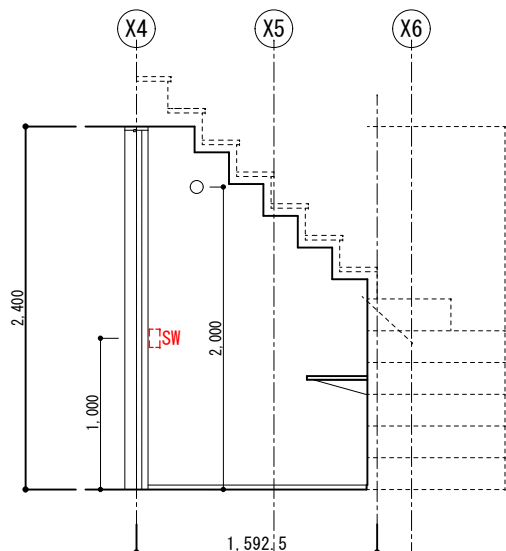

【階段下収納 A展開図 1/50】

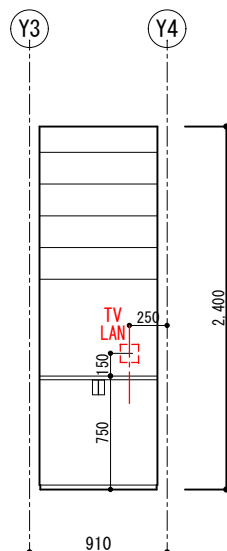

【階段下収納 B展開図 1/50】






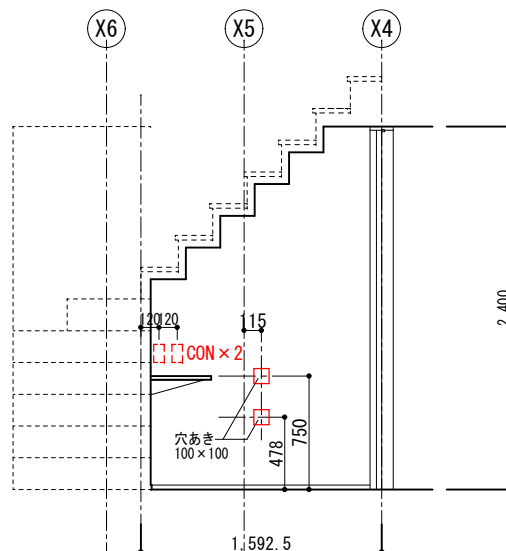


【階段下収納 A展開図 1/50】




施工主様	営業	工事	設計部長	設計
	棚原	下山	石原	小林



PROJ. NO	PROJ. TITLE	超暖G3 長期優良住宅
DATE	DWG. TITLE	DWG. NO.
2026/04/25	展開図②	A-12

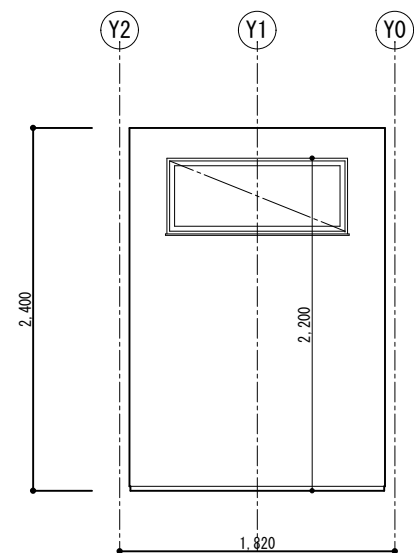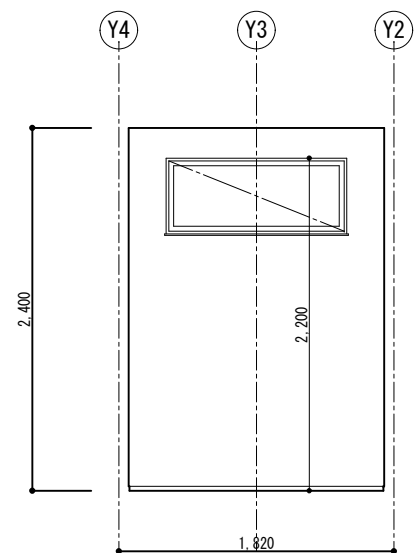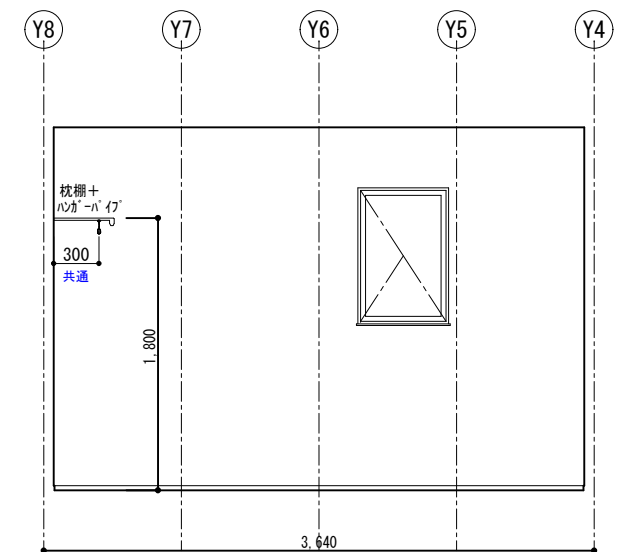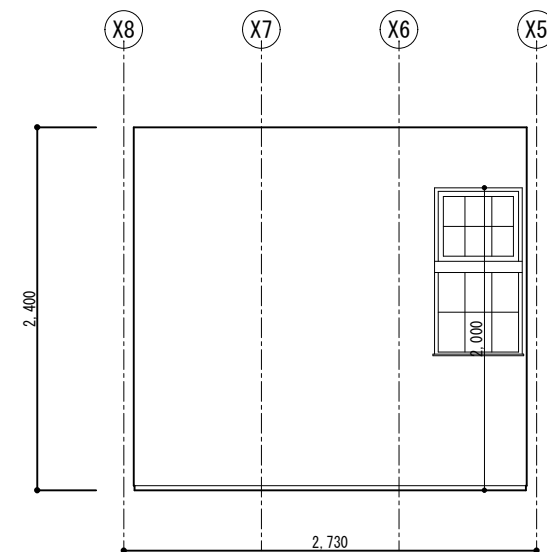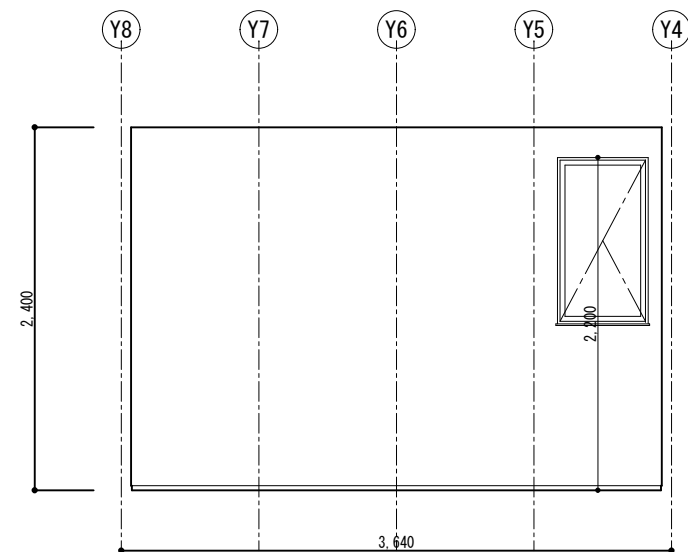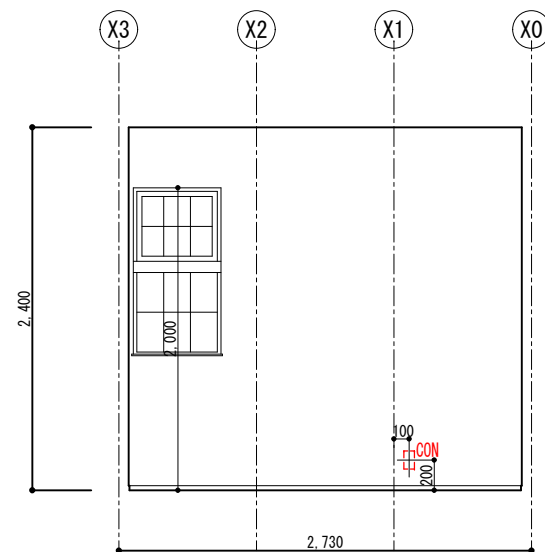

	施主様	営業	工事	設計部長	設計		PROJ. NO	PROJ. TITLE 犬丸 和也様・犬丸 梨香様邸新築工事		超暖63 長期優良住宅	
		棚原	下山	石原	小林		DATE	DWG. TITLE 展開図③		SCALE	DWG. NO.
							2026/04/15		A3:1/50		A-13

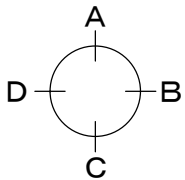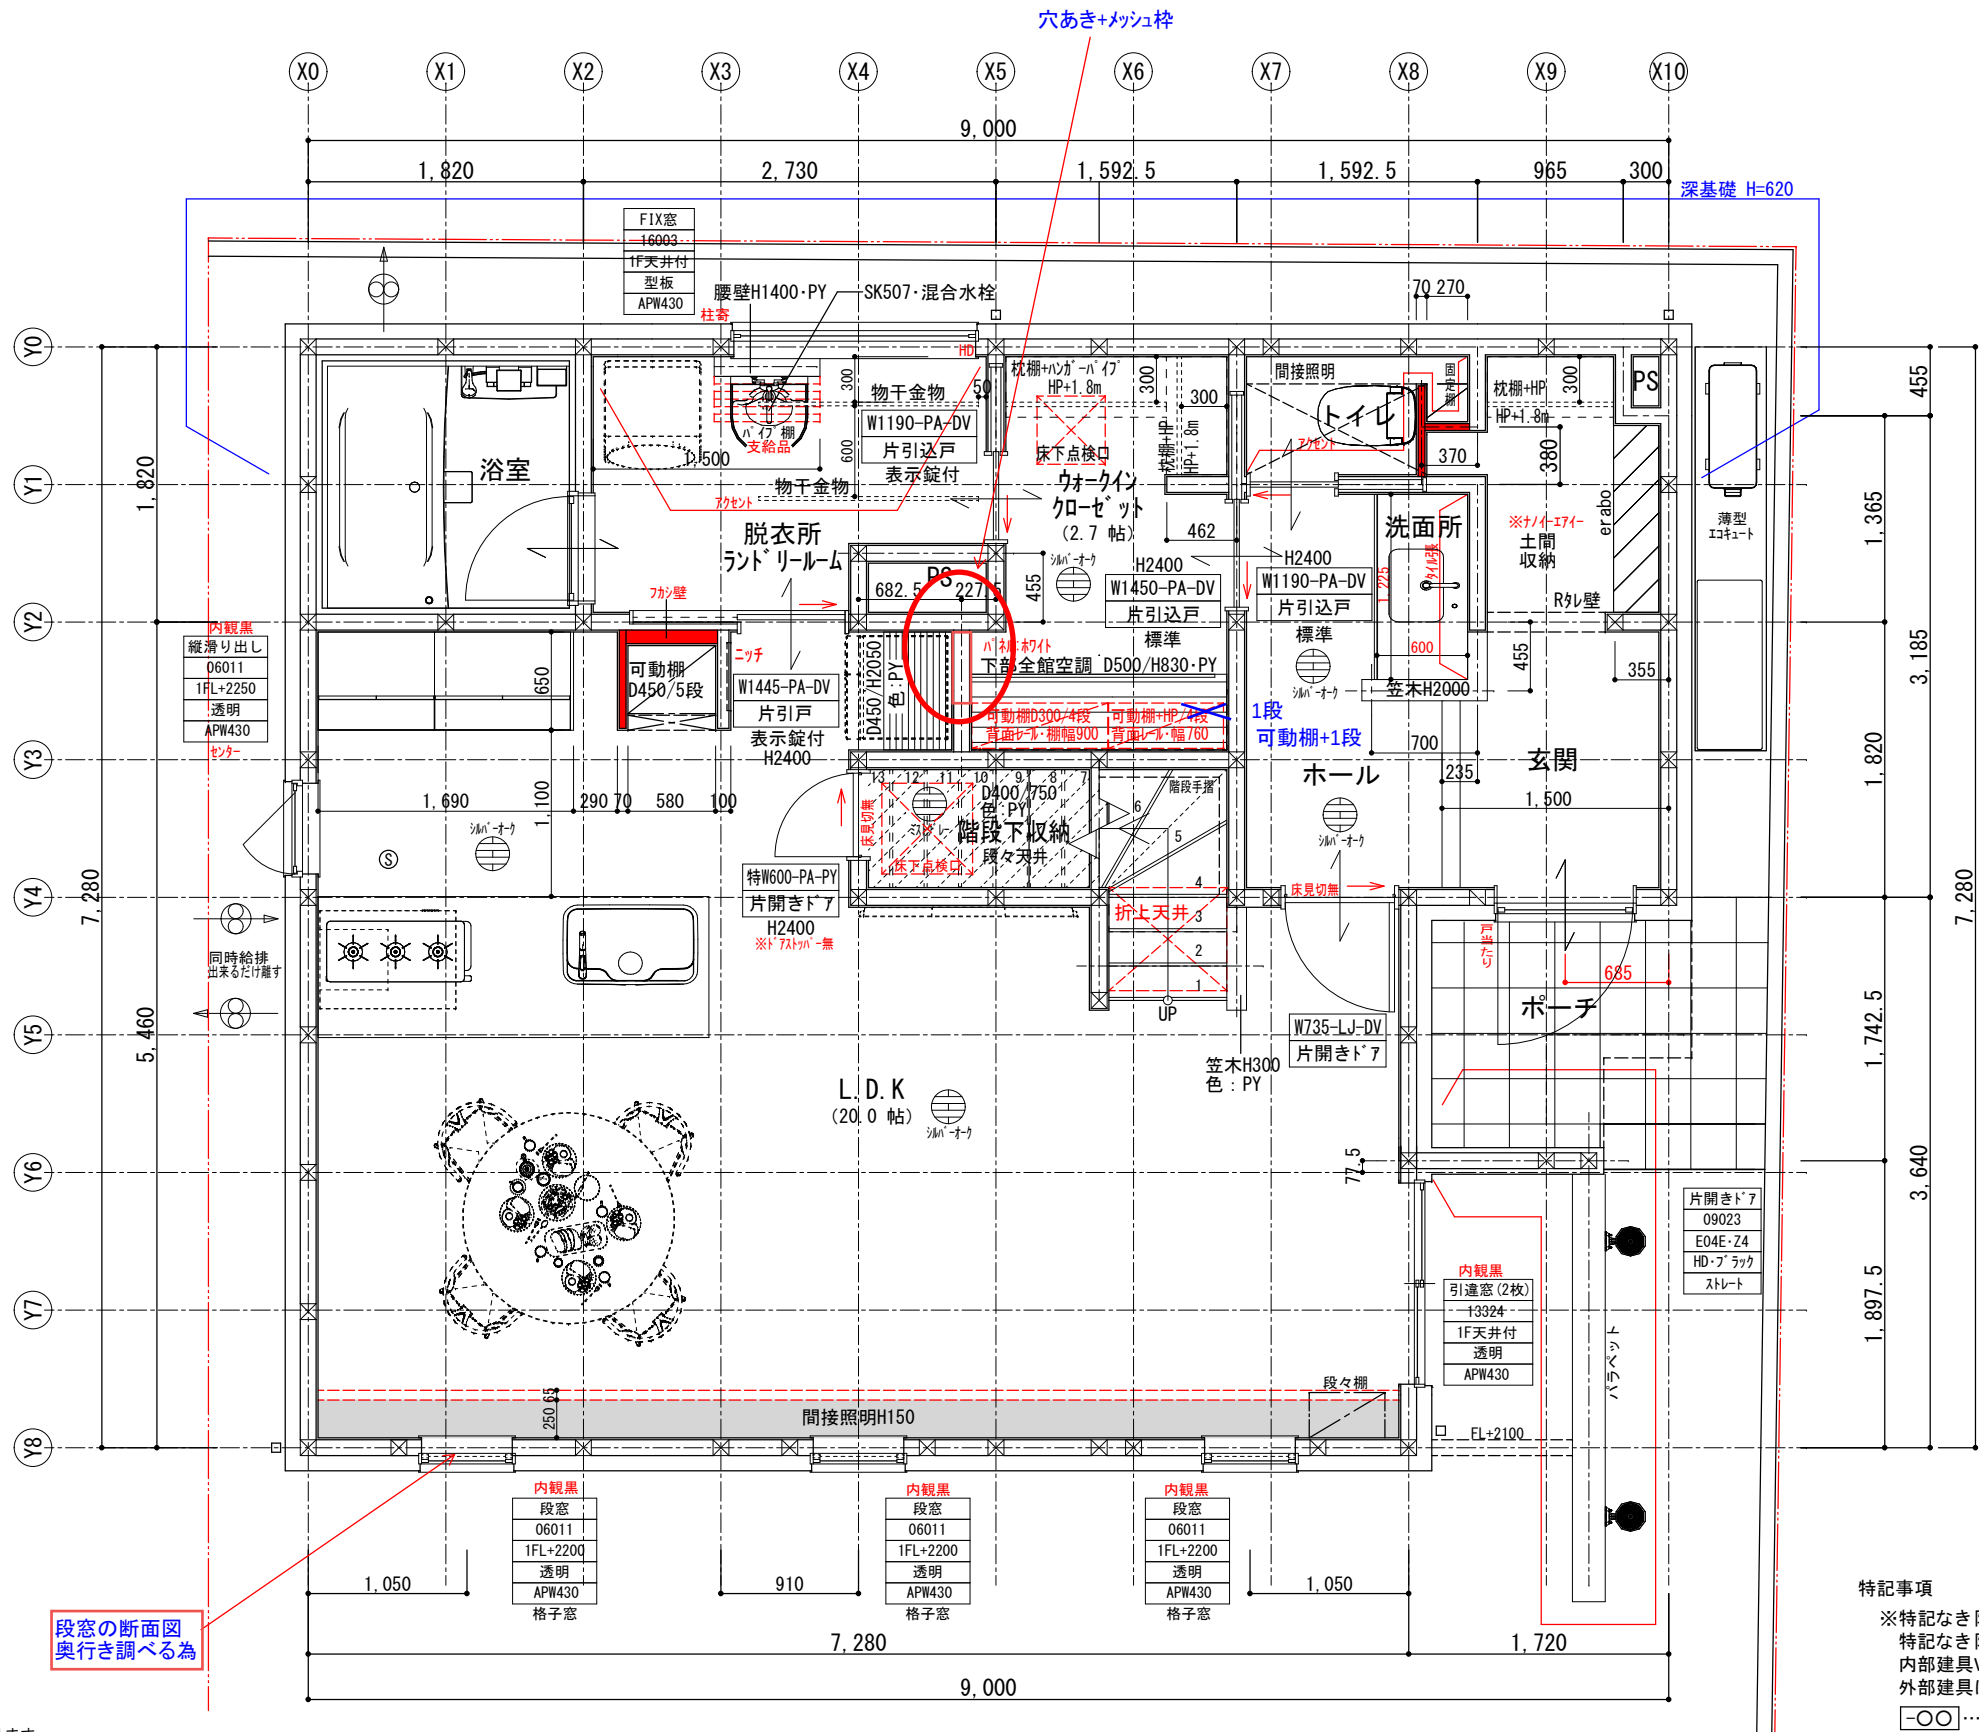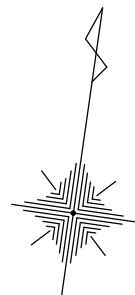

展開方向図

■ 1 階床面積	59.62 m ²
■ 2 階床面積	44.51 m ²
■ 延べ床面積	104.13 m ² (31.49 坪)
■ 施工床面積	0.00 m ² (0.00 坪)



- ・ 柱位置、耐力壁位置については構造図に準ずる
- ・ 寒冷地では玄関内部 $\times$ 10の立ち上がり部分において稀に結露することがあります
- ・ アイアン手摺の落下の恐れがあるため、転落防止ネットの設置が必要です
- ・ ポーチなどのタイル割り寸法は現場にて異なることがあります
- ・ 階段下トレなどの天井高さは現場にて異なることがあります
- ・ 棚等寸法は特記なき限り当社施工基準になります
- ・ 和室の壁は特記なき限り大壁仕上げとなります。畳厚さは1階：55mm、2階：15mmとなります
- ・ 階段の手すりの設置は外回り+高さは特記なき限り当社施工基準となります
- ・ 2Fキッチン、LB下部の1F天井に天井点検口を設置することがあります

段窓の断面図
奥行き調べる為

- 特記事項
- ※特記なき限りサッシ内寸法はH2000とする。
 - 特記なき限り床仕上げ高さは該当階FL±0とする。
 - 内部建具Wは、枠外寸法とする。
 - 外部建具は、規格寸法とする。
 - ○ …該当階FLからの高低差とする。
 - □ …下がり天井・勾配天井を示す。

	施主様	営業	工事	設計部長	設計	PROJ. NO	PROJ. TITLE 犬丸 和也様・犬丸 梨香様邸新築工事	超暖房 長期優良住宅
						DATE 2026/04/25	DWG. TITLE 1 階平面図	DWG. NO. A-05



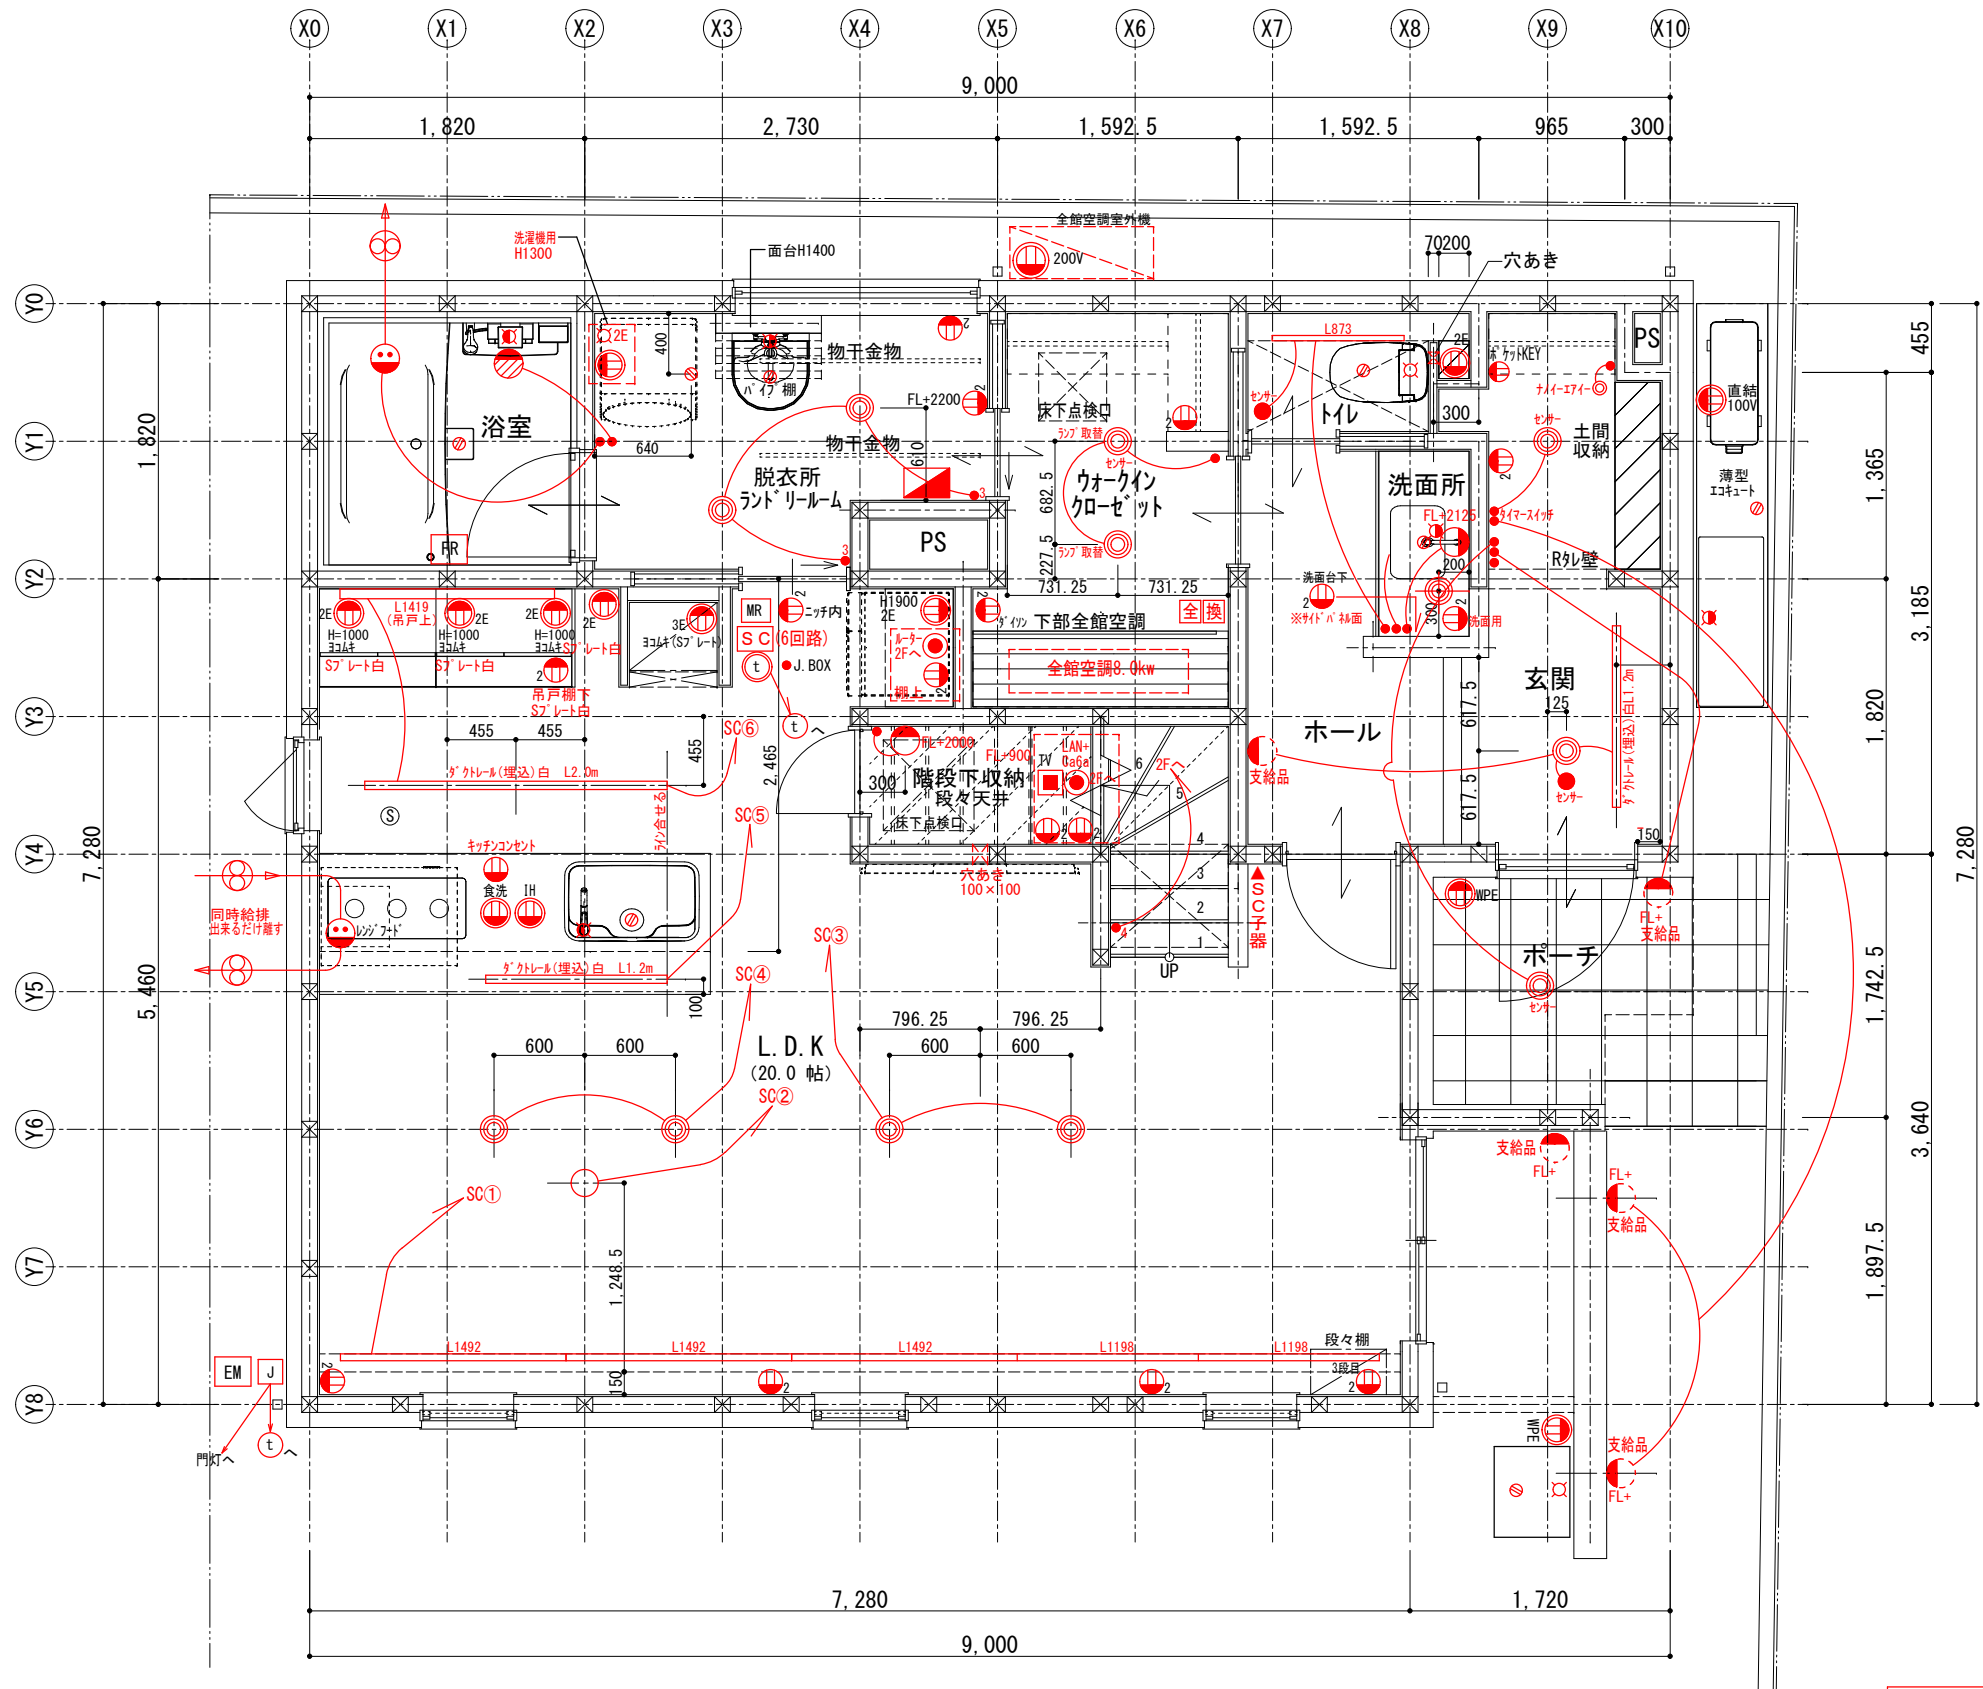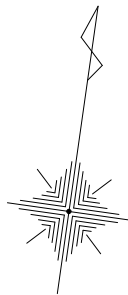

TVアンテナ：有
NET：(E0光)

凡 例


	1 ロコンセント
	2 ロコンセント
	2 ロアース付コンセント
	防水コンセント
	専用回路アース付コンセント
	直結電源
	専用回路直結電源
	T V 配線 (B S 同軸ケーブル)
	電話配管 ※入線工事は別途
	インターホン (親機)
	ドアホン
	給湯器メインリモコン
	浴室リモコン
	ジョイントBOX
	分電盤
	電気メーター
	シーリングライト
	ブラケット
	ユニット一体照明器具
	ダウンライト
	引掛シーリング (埋込丸型)
	24時間計画換気排気機
	24時間計画換気給気口
	S: 火災報知器 (煙感知)
	H: 火災報知器 (熱感知)
	スイッチ
	3 路スイッチ
	ホタルスイッチ
	パイロットスイッチ
	24時間計画換気用スイッチ
	調光付きスイッチ
	給水配管
	給湯給水配管
	排水口
■スイッチ・コンセントプレート等の取付け高さは、 特記なき限り下記の通りとする。	
各種スイッチ	FL+ドアノブセンター
一般コンセント	プレート芯=FL+200
A C 用コンセント	プレート芯(横)=FL+1900
インターホン	器具芯=FL+1450
各種コントローラー	
24時間計画給気口	器具芯=FL+1950

- ・照明、スイッチの位置は構造上、図面と多少異なる場合があります
- ・UHFアンテナ・BSアンテナ工事は別途必要です
- ・洗面脱衣室へ洗濯パンは標準設置されません
- ・2階の天井点検口は現場合わせとなります
- ・特記なき限り洗濯機の水栓は単水栓 (水のみ) だけとなります

施主様	営業	工事	設計部長	設計
	前田		石原	小林



PROJ. NO	PROJ. TITLE	犬丸和也様・犬丸梨香様邸新築工事		超暖33・全館空調 長期優良住宅
DATE	DWG. TITLE	SCALE	DWG. NO.	
2026/03/20	1 階設備図	1/50	A-09	

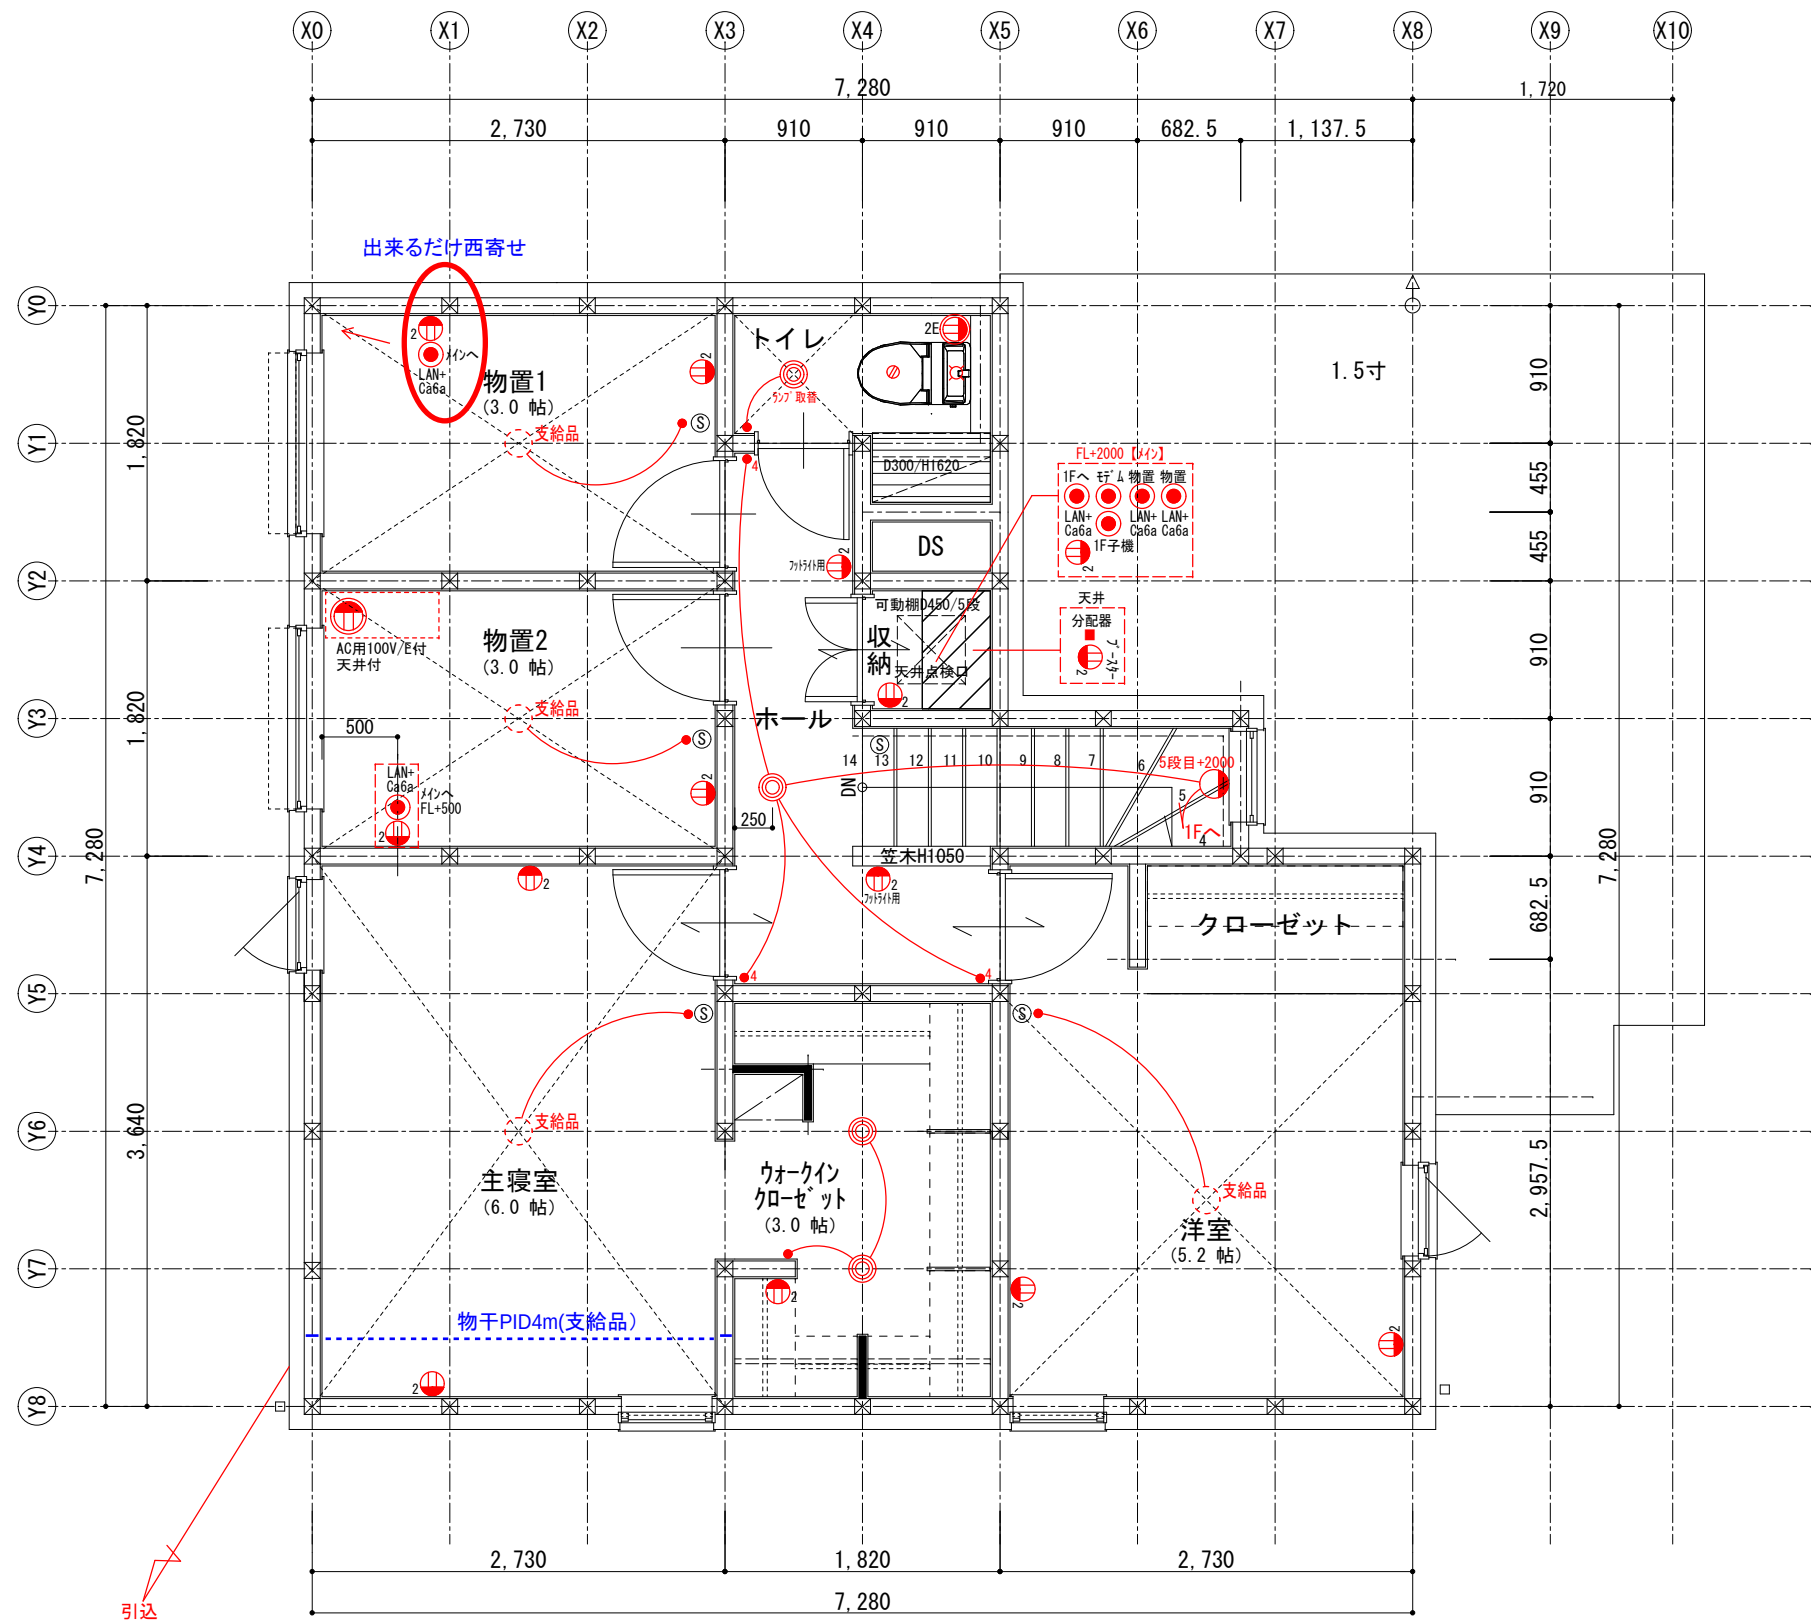

凡 例	
	1 ロコンセント
	2 ロコンセント
	2 ロアース付コンセント
	防水コンセント
	専用回路アース付コンセント
	直結電源
	専用回路直結電源
	T V 配線 (B S 同軸ケーブル)
	電話配管 ※入線工事は別途
	インターホン (親機)
	ドアホン
	給湯器メインリモコン
	浴室リモコン
	ジョイントBOX
	分電盤
	電気メーター
	シーリングライト
	ブラケット
	ユニット 一体照明器具
	ダウンライト
	引掛シーリング (埋込丸型)
	24時間計画換気排気機
	24時間計画換気給気口
	S: 火災報知器(煙感知) H: 火災報知器(熱感知)
	スイッチ
	3 路スイッチ
	ホテルスイッチ
	パイロットスイッチ
	24時間計画換気用スイッチ
	調光付きスイッチ
	給水配管
	給湯給水配管
	排水口
■スイッチ・コンセントプレート等の取付け高さは、特記なき限り下記の通りとする。	
各種スイッチ	FL+ドア7/7センター
一般コンセント	プレート芯=FL+200
A C 用コンセント	プレート 芯(横)=FL+1900
インターホン	器具芯=FL+1450
各種コントローラー	
24時間計画給気口	器具芯=FL+1950

TVアンテナ：有
NET：(E0光)

・ 照明、スイッチの位置は構造上、図面と多少異なる場合があります	施主様	営業	工事	設計部長	設計		PROJ. NO	PROJ. TITLE		超暖房・全館空調 長期優良住宅
・ UHFアンテナ・BSアンテナ工事は別途必要です							犬丸和也 様・犬丸梨香 様邸新築工事			
・ 洗面脱衣室へ洗濯パンは標準設置されません										
・ 2階の天井点検口は現場合わせとなります										
・ 特記なき限り洗濯機の水栓は単水栓（水のみ）だけとなります										
	前田			石原	小林		DATE	DWG. TITLE	SCALE	DWG. NO.
							2026/04/04	2 階設備図	1/50	A-10

<犬丸様 LINE 文面>

南側の書斎のクロスとコンセント位置は下記をお願いします

○南側の書斎について

南面と西面の2面にアクセントクロス。

・壁紙

東側 SP2502

南側 RE55621

西側 RE55621

北側 SP2502

天井 SP2502

・南側コンセント(有線 LAN セット)

位置：西の壁から+50cm

高さ：FL+50cm

・東側コンセント

変更なし

接地ダブルコンセント(簡易扉付) セット品

水の飛沫やほこりが入りにくい簡易扉付です。

●片刃挿入防止機能はありません。●はさみ金具は別売です。

●セット品


プレート



+

接地ダブルコンセント


(コンセントはマット仕上げではありません)

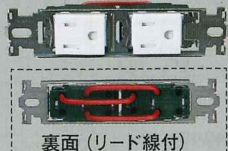

裏面 (リード線付)

プレート: マット仕上げ


コンセント: 標準仕上げ

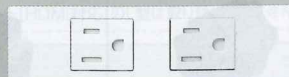

セラミックホワイト




ブラック

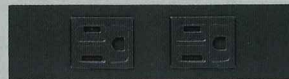

グレー

プレート: 標準仕上げ

コンセント: 標準仕上げ

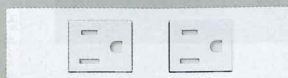

プレート: マット仕上げ コンセント: 標準仕上げ

Sプレート 埋込接地ダブルコンセントセット(簡易扉付)(マット仕上げ)

□ WN115215CW (セラミックホワイト)

■ WN115215H (グレー)

希望小売価格 2,800円(税抜)

■ WN115215B (ブラック)

希望小売価格 3,300円(税抜)

プレート: 標準仕上げ

コンセント: 標準仕上げ

Sプレート 埋込接地ダブルコンセントセット(簡易扉付)

□ WN115214CW (セラミックホワイト)

希望小売価格 2,600円(税抜)

ダブルコンセント セット品

●セット品

プレート



+

ダブルコンセント

(コンセントはマット仕上げではありません)



裏面 (リード線付)

プレート: マット仕上げ

コンセント: 標準仕上げ



セラミックホワイト




ブラック



グレー

プレート: 標準仕上げ

コンセント: 標準仕上げ

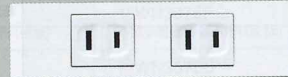

プレート: マット仕上げ コンセント: 標準仕上げ

Sプレート埋込ダブルコンセントセット(マット仕上げ)

□ WN100215CW (セラミックホワイト)

■ WN100215H (グレー)

希望小売価格 1,500円(税抜)

■ WN100215B (ブラック)

希望小売価格 2,000円(税抜)

プレート: 標準仕上げ

コンセント: 標準仕上げ


Sプレート埋込ダブルコンセントセット

□ WN100214CW (セラミックホワイト)

希望小売価格 1,300円(税抜)


寸法図

WCF8401, WCF8501

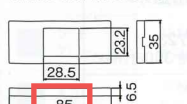


1口

WCF8402, WCF8502

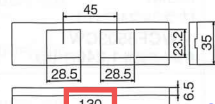


2口

WCF8403, WCF8503

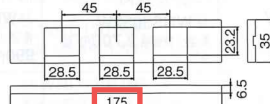


3口


WN115215, WN115214

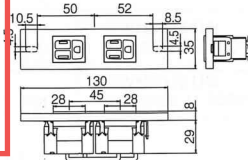


WCN3721

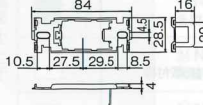


WCN3722

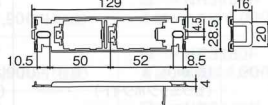

WCN3723

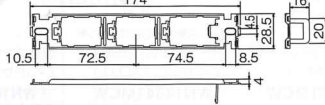

WN100215, WN100214

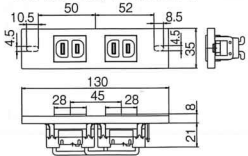

アドバンスシリーズ 配線器具

Archi Design

ADVANCE SERIES

アドバンスシリーズ

進化を続ける、くらしのスタンダード

住まいに必要なスイッチやコンセント。

身近に存在するものを上質に仕上げることで

空間はあたたかい表情を持ち、さらに心地のよい暮らしを生み出します。

親しみやすくも上質なデザイン、快適な操作性と便利な機能性。

「アドバンスシリーズ」は、配線器具のスタンダードとしてこれからも進化を続けます。



Switch



white



beige




gray




black


Outlet

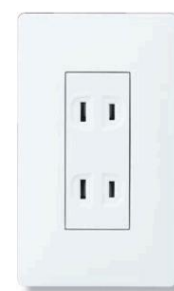

存在感を抑えながらも高い質感でインテリアに溶け込みます
操作性や汚れにくさにもこだわり、実用性も兼ね備えています

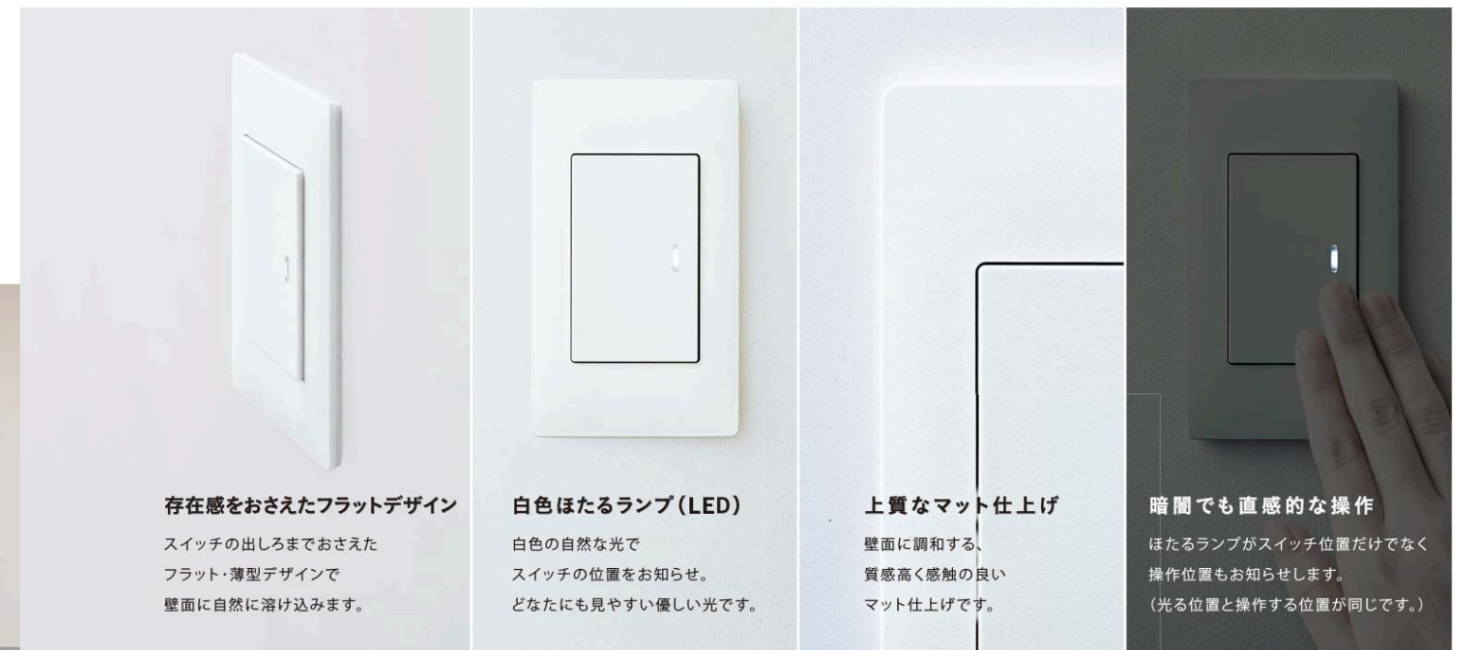

スイッチハンドルをプレートと同一質感にリニューアル

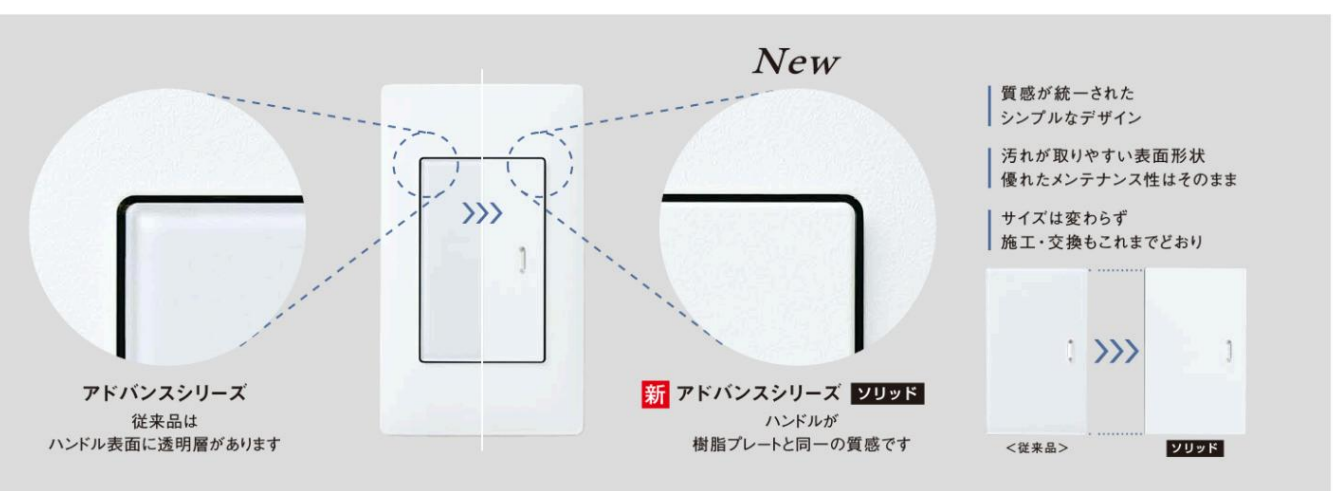

ハンドル・スイッチ (従来品対照表はこちら)

※従来品はハンドル表面に透明層があります。
※リンクプラスの[タッチ]タイプは通常のスイッチと操作感が異なるため、ソリッドタイプのご用意がございません(透明層デザインのためのラインアップとなります)

www2.panasonic.biz/jp/catalog/densetsu/haisen/ADV_solid/



プロネア
PRONAIR


■ 凡例

1F 脱衣所 ランドリールーム

 排気グリル
 換気対象外

天井 × 4 台


本体廻り詳細図

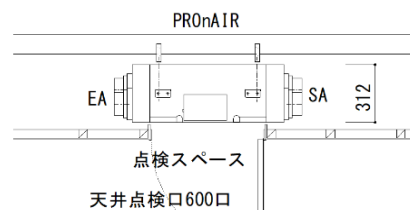

※φ50の場合ニップルで接続
ダクトテープ巻き
ダクトφ50・φ75
φ75不燃ダクト
250
10 115
ファイヤーダンパー


屋外フード詳細図

※FD付

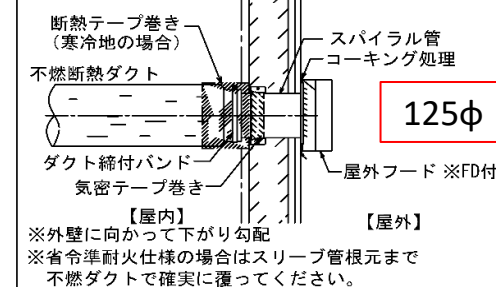

サイクロン式給気フード詳細図

✖FD付

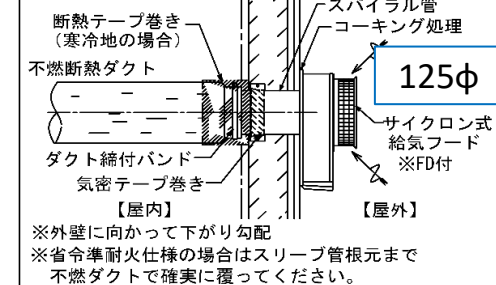

- 建築工事 天井点検口600□以上(換気本体真下)
- 電気工事 換気本体電源接続(AC100V・消費電力0.1KW)

■結露防止に関する設計・設置上についての注意事項

本体・ダクト設置は必ず断熱層の内側施工として下さい。

断熱ダクト使用の場合でも断熱層の内側施工として下さい。

屋外貫通廻りはダクト接続部根元まで断熱処理をして下さい。

本体～屋外へのダクトを延長する場合はダクト間の継手部分は必ず断熱処理をして下さい。

犬丸 和也 様 ・ 犬丸 梨香 様邸新築工事【2階換気平面図】

No. M260420B


PROnAIR

- 凡 例 (全館空調)③
- A 外気吸込 内径φ125(外径φ175)
 - E A 屋外排気 内径φ125(外径φ175)
 - S A 床下給気 内径φ125(外径φ175)
 - R A 室内吸込 内径φ125(外径φ175)
- ※チャンパー(4・6分岐) ～ グリル(ダクト先端)
- R A 室内吸込 内径φ75(外径φ125)

■ 凡 例

- 換気対象外
- 床排気グリル

床×2台

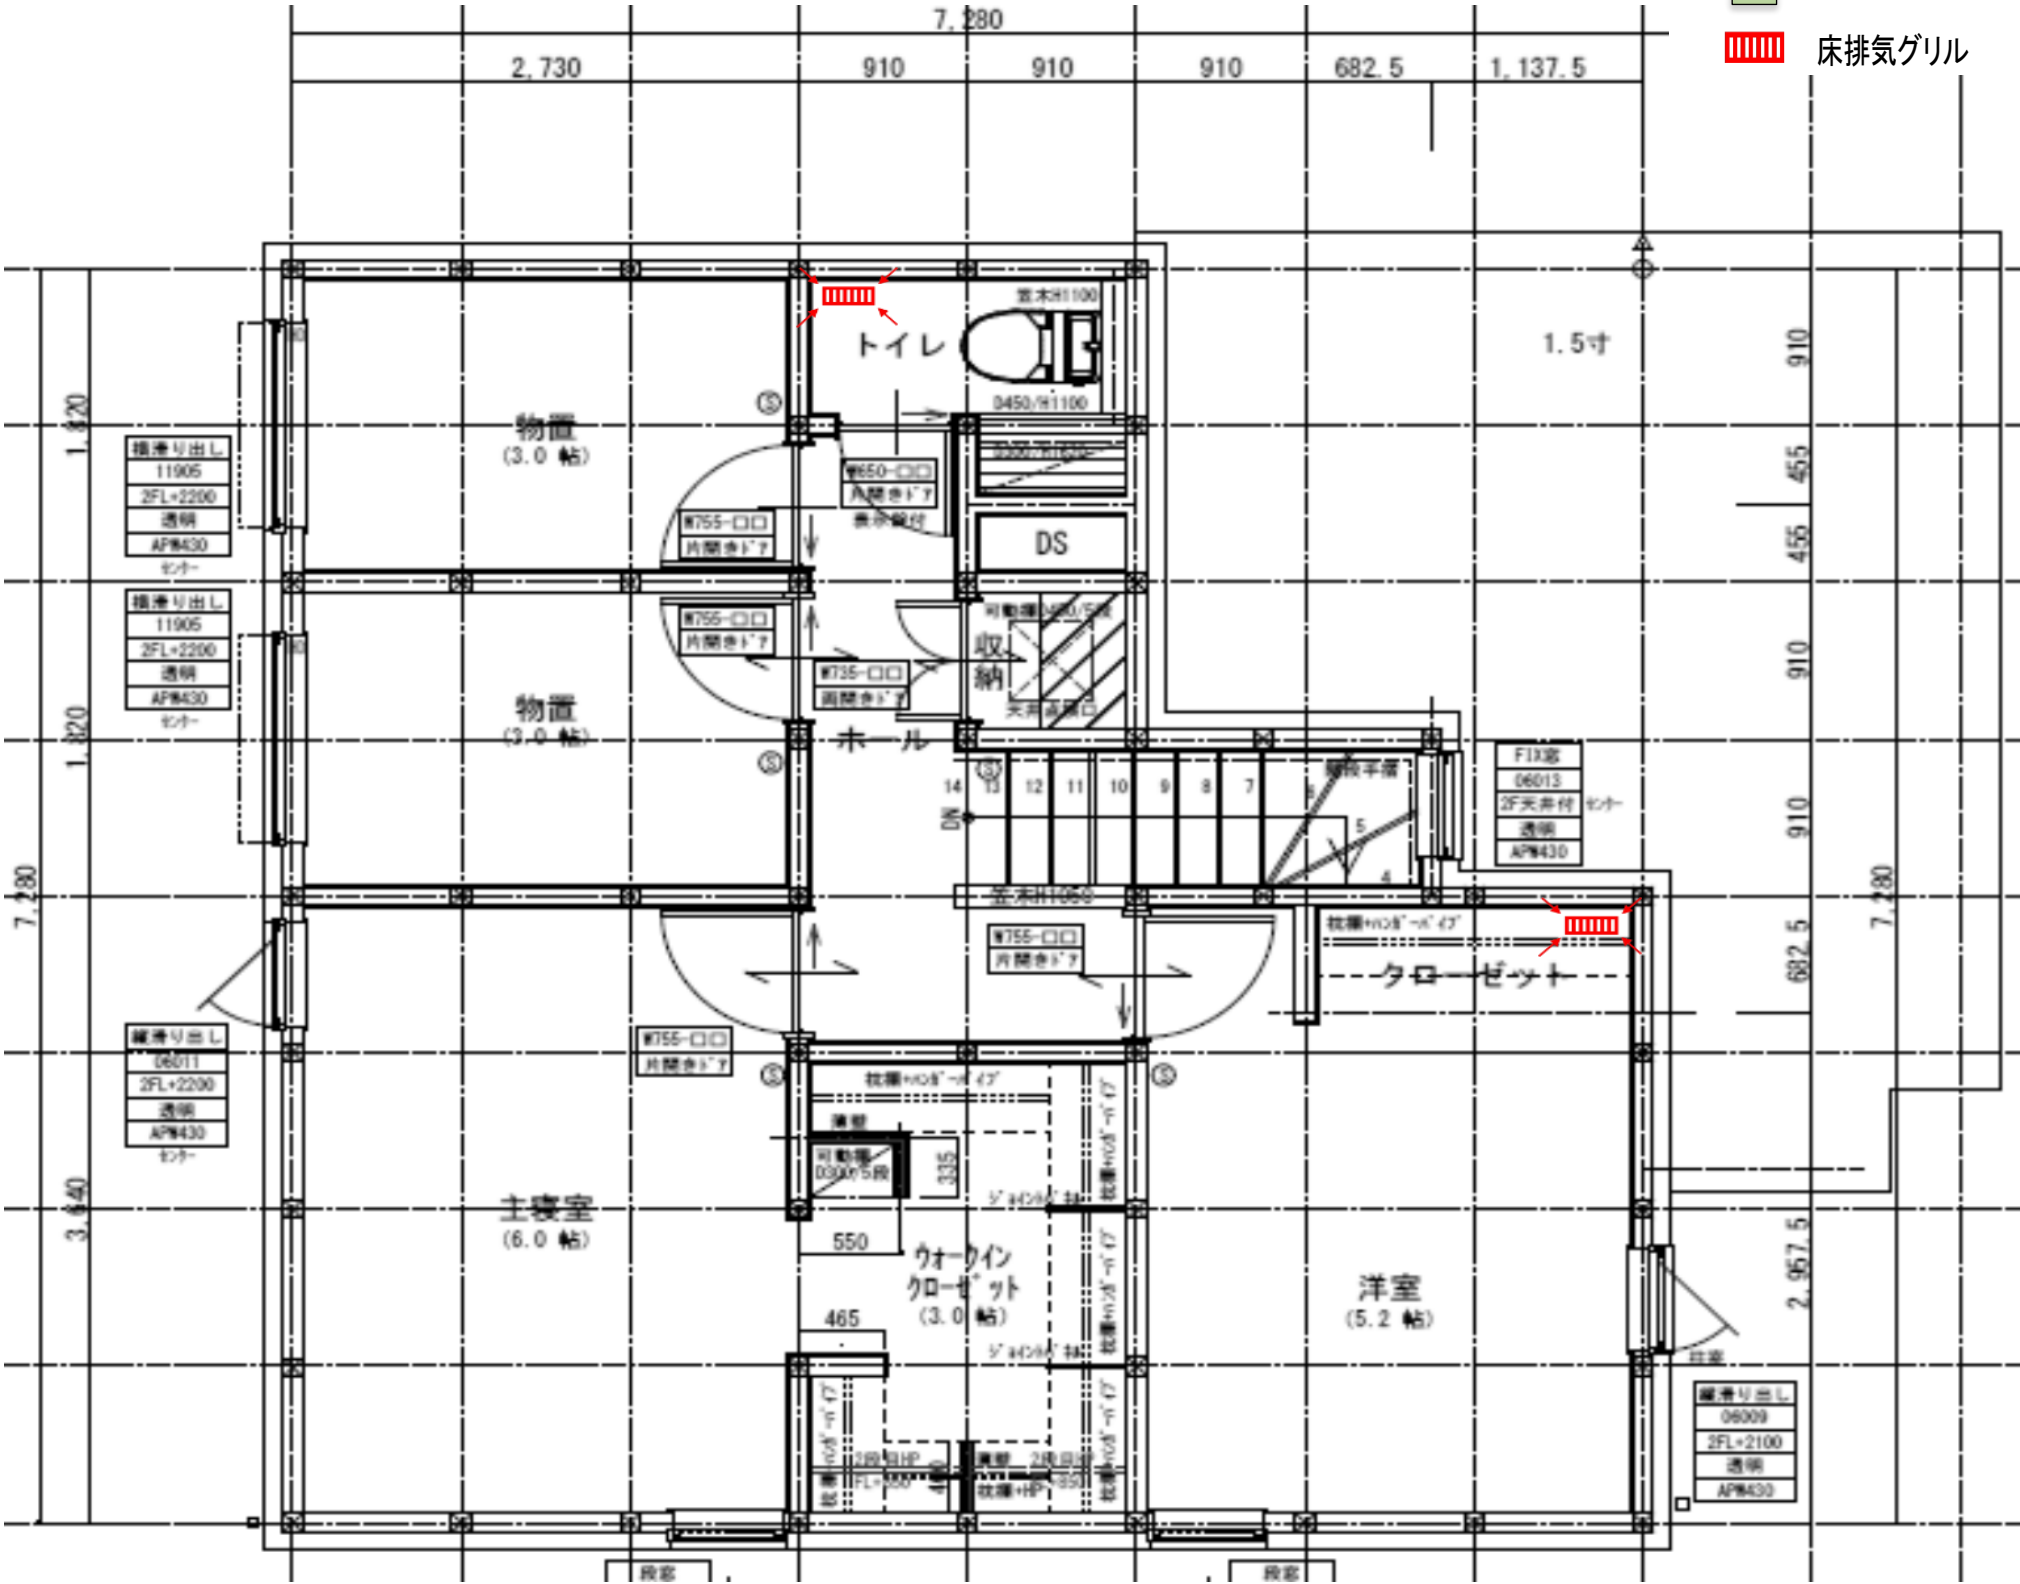

- ・寒冷地でのOA・EAダクトは断熱ダクトGWを使用。
- ・開き戸はすべてアンダーカットとする。
- ・給気フードと浴室及び、レンジフードの排気フードとの離隔距離は2M以上として下さい。
- ・燃焼機器の排気筒は別面で設置して下さい
- 結露防止に関する設計・設置上についての注意事項
- 本体・ダクト設置は必ず断熱層の内側施工として下さい。
- 断熱ダクト使用の場合でも断熱層の内側施工として下さい。
- 屋外貫通廻りはダクト接続部根元まで断熱処理をして下さい。
- 本体～屋外へのダクトを延長する場合はダクト間の継手部分は必ず断熱処理をして下さい。

2026年4月20日

担当: 西内

M260420B

※ 本資料は貴社情報による参考資料です。施工時には建築士と十分な確認を行なってください。
 ※ 本計算は建築法に基づいた計算です。実施の風量を保証するものではありません。
 ※ 確認申請の作成につきましては、書式は地域ごとに定められたものをご利用ください。

PRONAIR 圧力損失計算書

風量Qi(機械換気量)	183	m ³ /h
有効換気量(Qi×95%)	173.82	m ³ /h


①RA-EA(排気側)

日付 2026年4月20日

犬丸 和也 様・犬丸 梨香 様邸


機種 ①
担当 西内

部位	項目	値	脱衣所	2Fトイレ	1Fトイレ	土間収納	クローゼット	2F洋室	2F和室						
室内端末	風量Qi	(1)	30.5	30.5	30.5	30.5	30.5	30.5	30.5						
	有効換気量(Qi×0.95)	95%	28.97	28.97	28.97	28.97	28.97	28.97	28.97						
	ダクト径D	(2)	0.075	0.075	0.075	0.075	0.075	0.075	0.075						
	基準風量Qs	(3)	65	65	65	65	65	65	65						
	基準動圧Pv	(4)	10.1	10.1	10.1	10.1	10.1	10.1	10.1						
(イ)	室内端末と	(5)	3.27	0.89	3.27	3.27	3.27	3.27	0.89						
	= (4) × (5) × [(1)/(3)] ²		7.3	2.0	7.3	7.3	7.3	7.3	2.0						
5次ダクト	ダクト長L	(6)													
	ダクト径D	(7)	0.075												
	基準風量Qs	(8)	65												
	基準動圧Pv	(9)	10.1												
	摩擦係数λ	(10)	0.053												
(ロ)	曲がり部とB	(11)	0.85												
	曲がり係数	(12)													
分岐部	風量Qi	(13)													
	局部圧力係数と	(14)	0.12												
(ハ)	風量Qi	(15)													
	局部圧力係数と	(16)													
4次ダクト	風量Qi	(17)													
	局部圧力係数と	(18)													
(ニ)	風量Qi	(19)													
	局部圧力係数と	(20)													
4分岐 チャンバ (ホ)	風量Qi	(21)													
	局部圧力係数と	(22)													
3次ダクト	風量Qi	(23)													
	局部圧力係数と	(24)													
(ヘ)	風量Qi	(25)													
	局部圧力係数と	(26)													
分岐部	風量Qi	(27)													
	局部圧力係数と	(28)													
(ト)	風量Qi	(29)													
	局部圧力係数と	(30)													
2次ダクト	風量Qi	(31)													
	局部圧力係数と	(32)													
(チ)	風量Qi	(33)													
	局部圧力係数と	(34)													
1次ダクト	風量Qi	(35)													
	局部圧力係数と	(36)													
(リ)	風量Qi	(37)													
	局部圧力係数と	(38)													
フィルタ (ヌ)	風量Qi	(39)													
	局部圧力係数と	(40)													
屋外端末 (ル)	風量Qi	(41)													
	局部圧力係数と	(42)													
Pr=(イ)+(ロ)+(ハ)+(ニ)+(ホ)+(ト)+(チ)+(リ)+(ヌ)+(ル)			71.1	66.6	74.9	77.2	75.2	75.5							

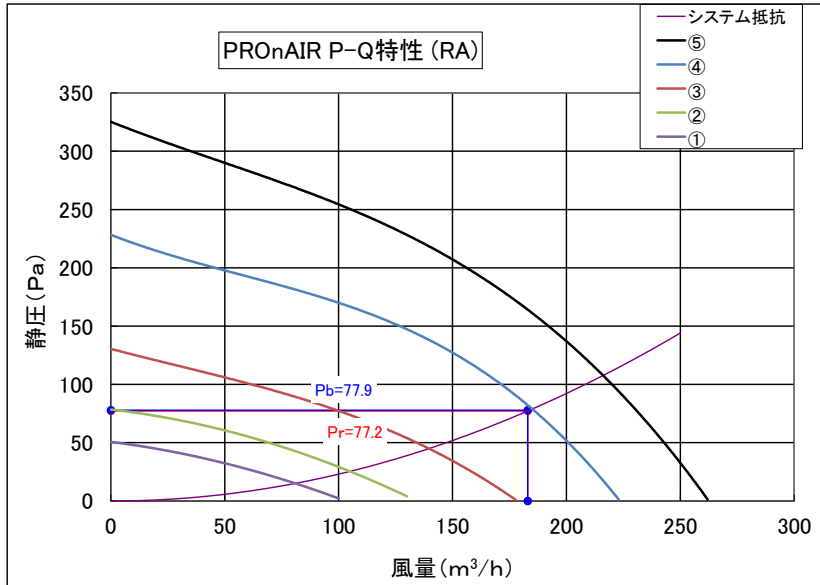

機械換気風量	183.0	m ³ /h
ファン静圧Pb	77.9	(Pa)
圧力損失の合計値Pr	77.2	(Pa)
判定	Pb>Pr	OK

ボリューム調整	4
---------	---

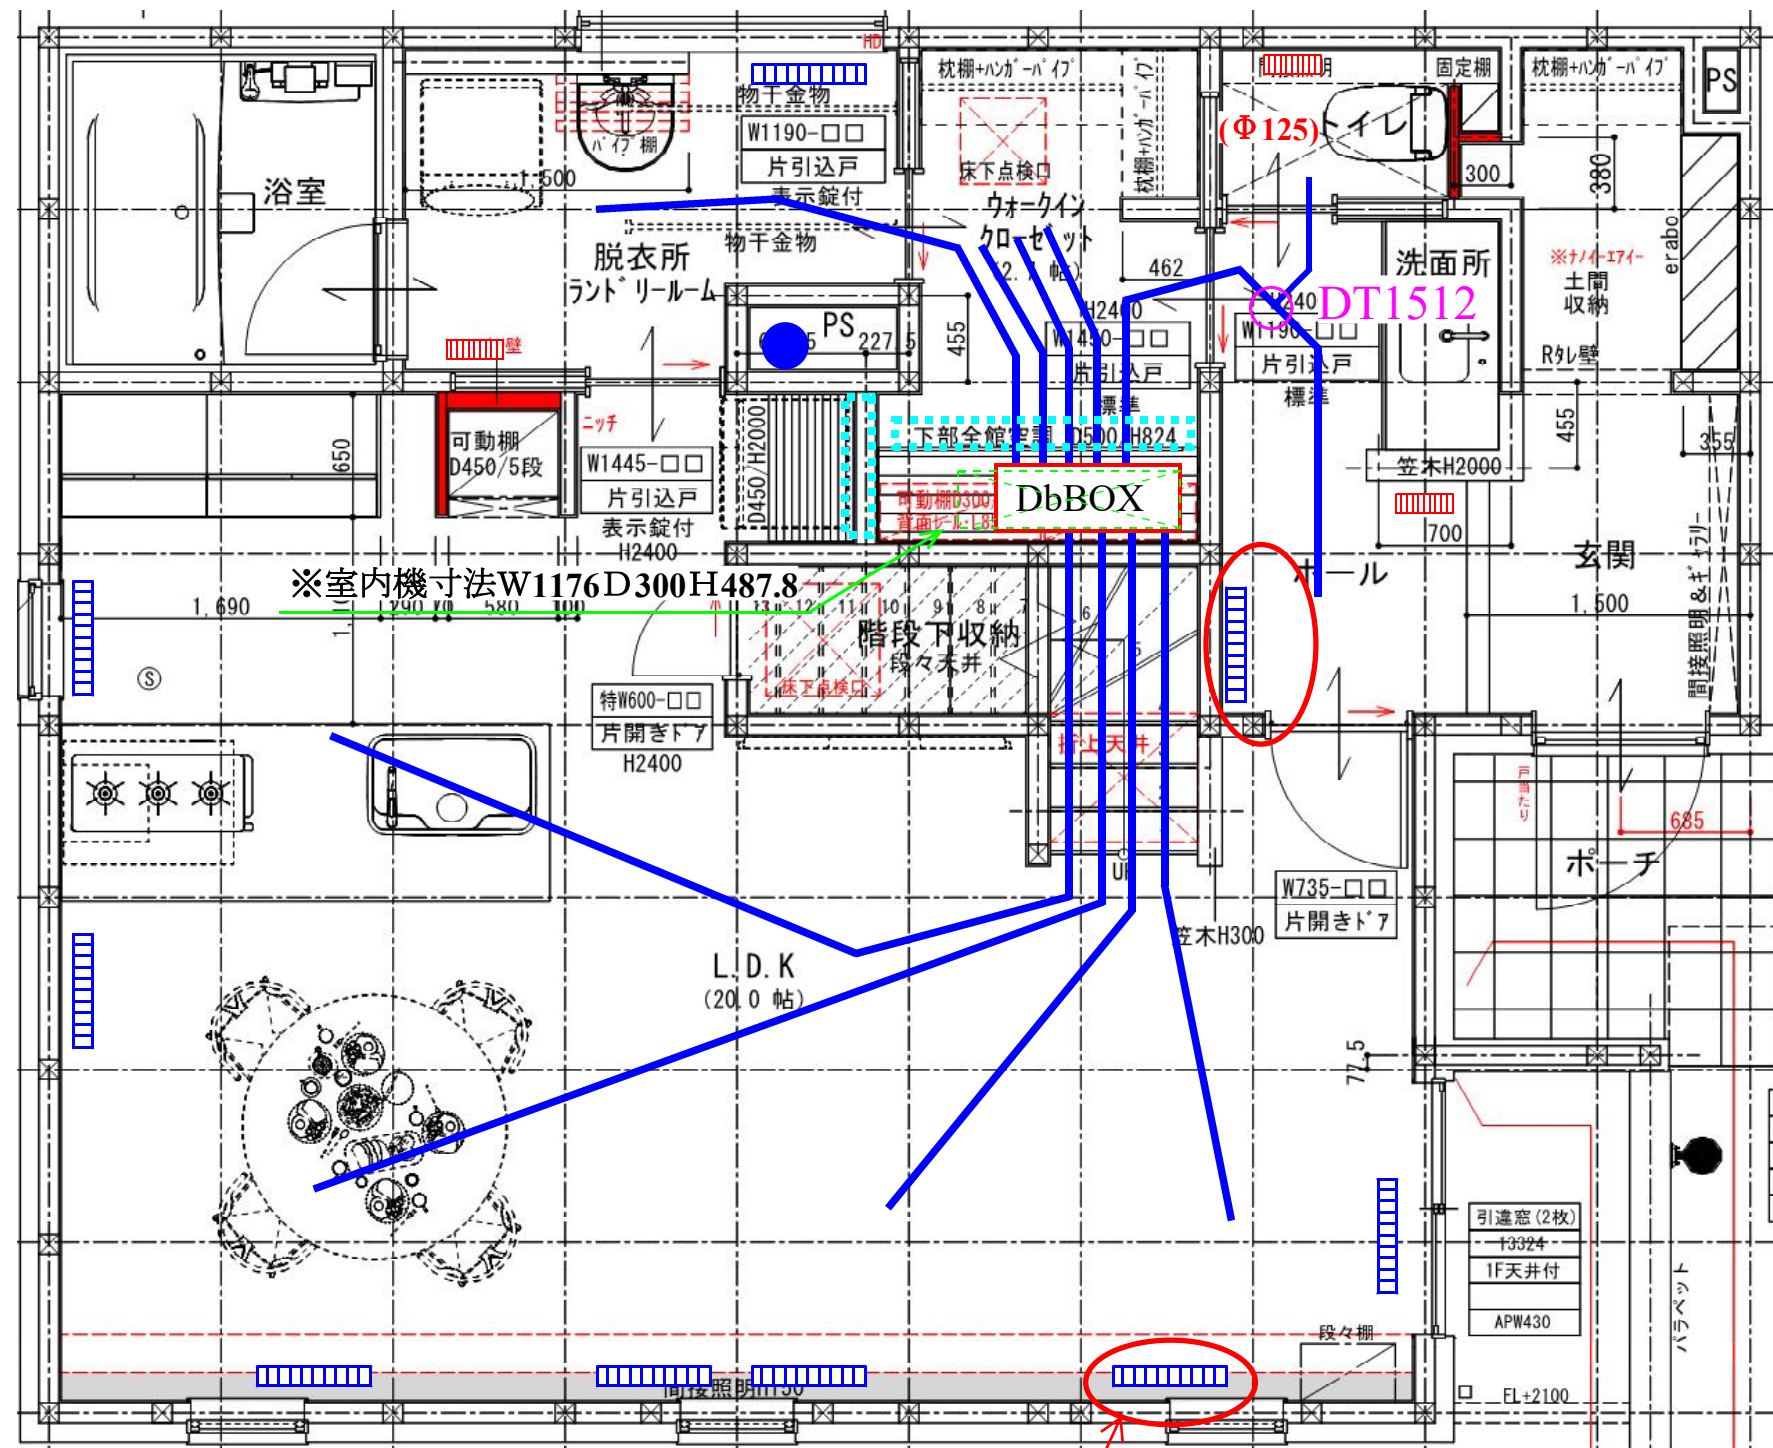

W600サイズ ×9ヶ所

ダクト 特記なきはΦ150

W300サイズ ×3ヶ所


※ダクトサイズ表記は内径寸法です(外径寸法は50mm増)

W600入らない・4/24

ガラリ等(有効開口0.2㎡)以上必要です

ガラリ等(有効開口0.1㎡)以上必要です

※各建具アンダーカット15mm以上必要です

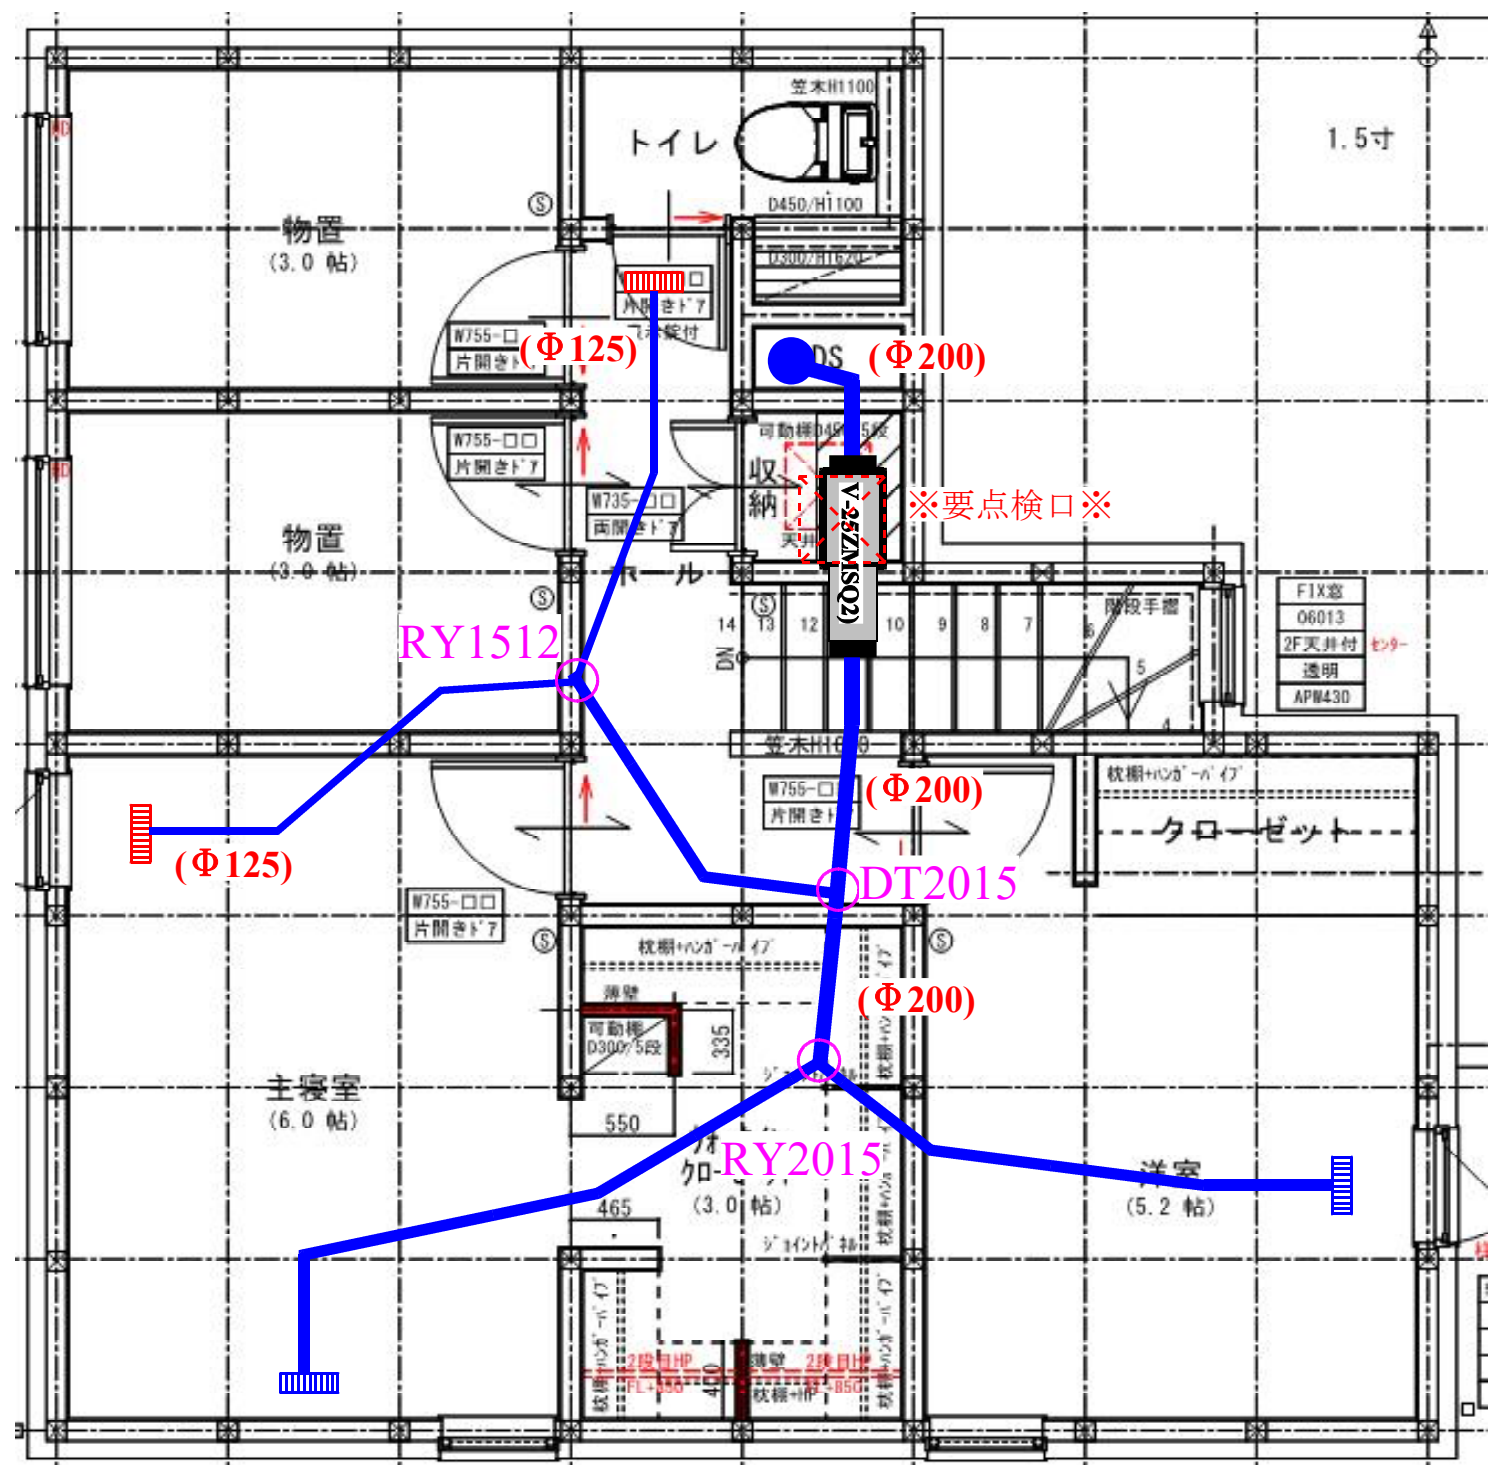

天井吹出口W300サイズ(Φ150)×2ヶ所

天井吹出口W300サイズ(Φ125)×2ヶ所

ダクト 特記なきはΦ150

※ダクトサイズ表記は内径寸法です(外径寸法は50mm増)

※各建具アンダーカット15mm以上必要です

株式会社オンレイ ONREI

現場名

犬丸和也様・梨香様邸 ・株式会社ホームライフ

タイプ

全館空調

日付

2026.04.06

図面名

2階初期プラン

型式・能力

縮尺

作成

吉原

承認

宮坂

Joto

ユニークな建材で
長持ち住まいをささえます。

高強度で素足に優しいガラリ ルームガラリ


NEW

新色登場!

※新色(ライトグレー色)はYV-7530のみ。


換気性能はもちろん、住まう人に優しいこだわりが詰まっています。

■ 素足でも優しい感触

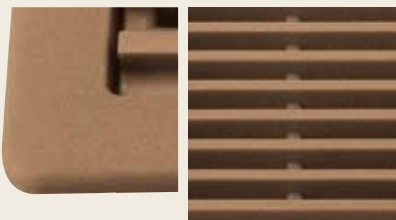


室内との温度差が少なく、素足で踏んでもヒヤッしない樹脂製。また、踏み心地にもこだわり、間隔が細かいスリットを採用。

■ 高強度な安心設計

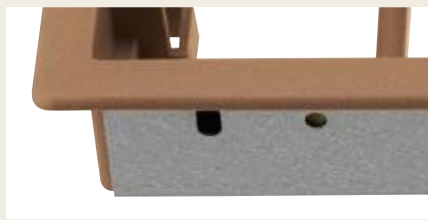


側面に補強用の鋼板を施し、100kgの荷重でもたわみは3mm以下という強度を確保。不快なキシミ音やガタツキもありません。

■ バリアフリー仕様

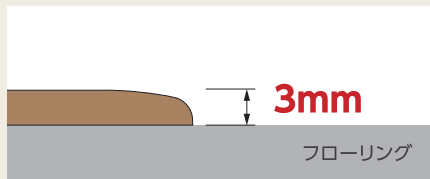

フロアとの段差もわずか3mm。ご年配の方やお子様にも安心です。

■ 優れたメンテナンス性

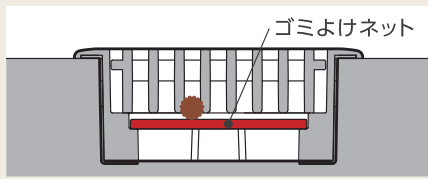

万ースリット内にゴミなどが入った場合でも、内部のゴミよけネットが床下への落下を防止。メンテナンスも簡単です。

※風量調節機能ありタイプにはゴミよけネットは付属されていません。

フタ



ゴミよけネット



受枠



※写真は一例です。品番によっては形状が異なる場合がございます。

ルームガラルの選べるバリエーション

カラー

IV

アイボリー

NL

ナチュラル

MB

ミディアムブラウン

DB

ダークブラウン

BB

ブラックブラウン

LG

ライトグレー

※LG(ライトグレー色)は、YV-7530のみ

幅サイズ

90

165

床下放熱器対応

チャンバー付タイプ

風量調節機能ありタイプ

スライドを動かすと風量調節可能。

幅サイズ 90

※想定使用温度は40℃以下です。

IV NL MB DB BB LG

アイボリー ナチュラル ミディアムブラウン ダークブラウン ブラックブラウン ライトグレー

LG色は YV-7530のみ

■ YV-7530

床開口寸法
258×75mm

※有効開口面積:αA:45cm²/コ・68cm²/コ(開口面積)

■ YV-7560

床開口寸法
609×75mm

※有効開口面積:αA:86cm²/コ・140cm²/コ(開口面積)

■ YV-7590

床開口寸法
909×75mm

※有効開口面積:αA:129cm²/コ・210cm²/コ(開口面積)

品番	YV-7530-□□	YV-7560-□□	YV-7590-□□
寸法	274×90×38.4mm	624.5×90×26.5mm	925×90×26.5mm
床開口寸法	258×75mm	609×75mm	909×75mm
材質	本体:PP 補強用銅板(GL銅板*)		
梱包	6セット/ケース	4セット/ケース	
正価	2,900円/セット	6,480円/セット	9,380円/セット
セット明細	受枠:1コ フタ:1コ ゴミよけネット:1枚 取付ビス:5本	受枠:1コ フタ:2コ ゴミよけネット:2枚 取付ビス:10本	受枠:1コ フタ:3コ ゴミよけネット:3枚 取付ビス:15本

※1200mm・1500mmタイプもご用意しております(受注生産)。詳しくは最寄りの営業所にお問い合わせください。 *JIS G3321

チャンバー付ルームガラル

24時間換気の給排気に。

床開口寸法
258×75mm

IV NL MB DB BB

アイボリー ナチュラル ミディアムブラウン ダークブラウン ブラックブラウン

品番	YV-C7530-□□
寸法	274×90×246mm
床開口寸法	258×75mm
材質	本体:PP 補強用銅板(GL銅板*) チャンバー部:EPS(発泡ポリスチレン) 継手部:PP
梱包	4セット/ケース
正価	9,380円/セット
セット明細	受枠:1コ フタ:1コ ゴミよけネット:1枚 取付ビス:5本

*JIS G3321

幅サイズ 165

※想定使用温度は60℃以下です。

IV NL MB DB BB

アイボリー ナチュラル ミディアムブラウン ダークブラウン ブラックブラウン

■ YV-15079 床下放熱器に対応

床開口寸法
790×150mm

※有効開口面積:[YV-15079] αA:350cm²/コ・510cm²/コ(開口面積)
[YV-N15079]αA:340cm²/コ・510cm²/コ(開口面積)

■ YV-150170 床下放熱器に対応

床開口寸法
1,700×150mm

※有効開口面積:[YV-150170] αA:750cm²/コ・1,100cm²/コ(開口面積)
[YV-N150170]αA:760cm²/コ・1,100cm²/コ(開口面積)

風量調節機能なし		風量調節機能あり	
品番	YV-15079-□□	YV-N15079-□□	YV-150170-□□
寸法	807×165×26.5mm		1,716×165×26.5mm
床開口寸法	790×150mm		1,700×150mm
材質	本体:PP 補強用銅板(GL銅板*)		本体:PP 補強用銅板(GL銅板*)
梱包	2セット/ケース		2セット/ケース
正価	14,500円/セット		25,550円/セット
セット明細	受枠:1コ フタ:2コ ゴミよけネット:2枚 取付ビス:10本	受枠:1コ フタ:2コ 風量調節スライド:2枚 取付ビス:10本	受枠:1コ フタ:5コ ゴミよけネット:5枚 取付ビス:25本

*JIS G3321

※有効開口面積αAは測定値であり、保証値ではありません。安全率を加味してご使用ください。
※αAとは、圧力損失を加味した有効開口面積です。

◎ご注文の際は品番の後に色型番をご記入ください。(例)YV-7530-□□Ⅴ

城東テクノ株式会社

ユニークな建材で長持ち住まいをささえます。

本製品に関するお問い合わせは

ダイヤル【J】0120-106011
受付時間(土・日・祝を除く) 9:00~12:00/13:00~16:00

城東テクノホームページ

Joto

https://www.joto.com



Information ※Joto製品は、PL法に基づく製品保証体制を取っております。※掲載の正価には、消費税は含まれておりません。※仕様・価格は予告なく変更する場合がございますので、予めご了承ください。
※写真は印刷のため、実際の色と異なる場合がございます。現物またはサンプルなどにてご確認ください。

白柱 飾縁

112
150
115

112

120.92.61.46mm



