

[illegible]

■内装仕様										■内部造作部材・備品仕様			
部屋名								備 考		部位	メーカー	仕様・品番	色柄
1階	床仕上げ		巾木・畳寄せ		壁仕上げ	天井仕上げ		廻縁	天井高さ	玄関三方枠:【ベリティス】しっくいホワイト			
玄関	【LIXIL】磁器質タイル パセオ 300□／厚9mm PSO-BR1 目地:外部ボーチに準ずる	【パナソニック】ベリティス スマート巾木(スカート無) H=30 しっくいホワイト	【サンゲツ】ビニールクロス SP-2508	【サンゲツ】ビニールクロス SP-2508	無	2565							
土間収納	【LIXIL】磁器質タイル パセオ 300□／厚9mm PSO-BR1 目地:外部ボーチに準ずる	【パナソニック】ベリティス スマート巾木(スカート無) H=30 しっくいホワイト	【サンゲツ】ビニールクロス SP-2508	【サンゲツ】ビニールクロス SP-2508	無	2400							
1階ホール	【朝日ウッドテック】エアリス-α 2Pタイプ／厚12mm ミストグレー	【パナソニック】ベリティス スマート巾木(スカート無) H=30 しっくいホワイト	【サンゲツ】ビニールクロス SP-2508	【サンゲツ】ビニールクロス SP-2508	無	2400							
LDK	【朝日ウッドテック】エアリス-α 2Pタイプ／厚12mm ミストグレー	【パナソニック】ベリティス スマート巾木(スカート無) H=30 しっくいホワイト	【サンゲツ】ビニールクロス SP-2508	【サンゲツ】ビニールクロス SP-2508	無	2400	間接照明						
洗面 コーナー	【朝日ウッドテック】エアリス-α 2Pタイプ／厚12mm ミストグレー	【パナソニック】ベリティス スマート巾木(スカート無) H=30 しっくいホワイト	【サンゲツ】ビニールクロス SP-2508	【サンゲツ】ビニールクロス SP-2508	無	2400							
1階トイレ	【サンゲツ】クッションフロア厚1.8mm HM12041	【パナソニック】ベリティス スマート巾木(スカート無) H=30 しっくいホワイト	【サンゲツ】ビニールクロス SP-2508	【サンゲツ】ビニールクロス SP-2508	無	2400	間接照明						
階段室	【朝日ウッドテック】エアリス-α 2Pタイプ／厚12mm 踏み板 ミストグレー 蹴込み板・側板 クロ、側板クロ		【サンゲツ】ビニールクロス SP-2508	【サンゲツ】ビニールクロス SP-2508	無	—							
脱衣所 ランドリールーム	【サンゲツ】クッションフロア厚1.8mm	【パナソニック】ベリティス スマート巾木(スカート無) H=30 しっくいホワイト	【サンゲツ】ビニールクロス SP-2508	【サンゲツ】ビニールクロス SP-2508	無	2400	浴室三方枠:ホワイト JOTO 開戸SP-8003						
WIC	【朝日ウッドテック】エアリス-α 2Pタイプ／厚12mm ミストグレー	【パナソニック】ベリティス スマート巾木(スカート無) H=30 しっくいホワイト	【サンゲツ】ビニールクロス SP-2508	【サンゲツ】ビニールクロス SP-2508	無	2400	下部全館空調						
階段下 収納	【朝日ウッドテック】エアリス-α 2Pタイプ／厚12mm ミストグレー	【パナソニック】ベリティス スマート巾木(スカート無) H=30 しっくいホワイト	【サンゲツ】ビニールクロス SP-2508	【サンゲツ】ビニールクロス SP-2508	無	2400							

■住設仕様

部位	メーカー	仕様・品番	色柄
キッチン			
システムキッチン	タカスタンダード	※PB参照とする	
食器棚		別途	
浴室			
システムバス	タカスタンダード	※PB参照とする	
洗面脱衣室			
洗面化粧台	タカスタンダード	※PB参照とする	
洗濯機用水栓	タブチ	SP1100N 単水栓／水道用コンセント	
1階トイレ			
便器	TOTO	ペーシアPita(フチレス)／(ECO5・床排水) 壁リモコン付	ビュアホワイト
便器	TOTO	キャビネットタンク(ECO5)	
紙巻器	KAWAJUN	ペーパーホルダー	SC-043-XC
タオル掛け	KAWAJUN	タオルリング	SC-040-XC
2階トイレ			
便器	LIXIL	ペーシア(フチレス)／(床排水) 手洗付 壁リモコン付	ビュアホワイト
紙巻器	KAWAJUN	ペーパーホルダー	SC-043-XC
タオル掛け	KAWAJUN	タオルリング	SC-040-XC

■電気設備仕様

分電盤			
分電盤	24回路／75A ※オール電化の場合等、プランにより異なります		
主要配線 ※位置・数量は、設備図によります			
幹線	14スケア ※幹線の径は、主幹容量によります		
TV配線	BS同軸ケーブル(標準2箇所) 分配器 4K・8K対応 ブースターなし		
電話配管	空配管／6極2芯対応(標準1箇所) ※入線工事は、お客様手配となります		
LAN配線	別途		
インターネット用配管	空配管／光対応 別途 ※入線工事は、お客様手配となります		
電設資材 ※位置・数量は、設備図によります			
スイッチ	パナソニック ワイド21シリーズ スクエアプレート (ホテル トイレのみ) ※簡易耐火用プレート・耐火フランクチップ・防気カバー付き ホワイト		
コンセント (2口)	パナソニック ワイド21シリーズ スクエアプレート ※簡易耐火用プレート・防気カバー付き (LDK 標準7箇所/居室 標準2箇所) ホワイト		
メーターボックス	河村電機産業 MXO 131D 口口 (WN:ホワイト/BRN:ブラウン/BN:ブラック) ブラック		
入線カバー/ジョイントボックス	パナソニック WP9631/WJ4611もしくはWJ4613 ブラック		
防水コンセント	パナソニック WK4602 ブラック		
24時間計画換気システム／全館空調 第1種換気システム			
ECO床暖システム	オンレイ 床下型全館空調システム+高性能熱交換システム PM2.5対応フィルター付き		
24h換気排気口	更科製作所 外部フード(防虫網付) TR-125-KT ブラック		
24h換気給気口	ケイ・マック サイクロン式給気フード メタリックグレー		
空調給気口	城東テクノ 1階床 W300(YV-7530)及びW600(YV-7560) 図面参照		
空調給気口	オンレイ 2階天井 TC-150(ホワイト) ホワイト		
室内排気口	ケイ・マック 1階天井 ファイヤーダンパー付排気グリル(ホワイト/ベージュ) ブラック		
室内排気口	城東テクノ 2階床 排気グリル YV-C7530 図面参照		
※建物規模・形状によっては上記以外の部材構成の場合もあります。			
意匠パネル		室内機エコパネル(大または小) ※無塗装品もありますが、塗装費用が掛かります。	ホワイト
24時間換気以外			
排気口	更科製作所 外部フード(防虫網付) TR-100-KT		
排気口(キッチン)	更科製作所 外部フード TR-150-KT		
インターホン			
カラーモニター ドアホン	パナソニック VL-SE35XLA(録画機能付) ドアホン+親機1台		1台
住宅用防火設備 ※プランにより、位置・数量は異なります			
煙式火災報知器	能美防災 まもるくん FSKJ225-B-N	単独電池式(光電式・2種)	ホワイト
専用回路			
エアコン	—	図面参照 ※LDKIにサブエアコン用に専用コンセント1か所設置	
IH	—		
電気温水器	—		
電子レンジ	—		
衣類乾燥機	—		
洗浄暖房便座	—		
食洗機	—		
アンテナ工事			
あり	※アンテナ取付位置・向き・個数は現場立ち合いにて確認します。 ※ドコモ光でTVをご視聴される場合、LAN端子が必要になることがあります。		

■インテリア工事

カーテン工事			
別途工事			
照明工事 ※プランにより、位置・数量は異なります			
※PB参照とする			

施主様

営業

工事

設計部長

設計

ARCHI homelife KYOTO

PROJ. NO

PROJ. TITLE

犬丸和也様・犬丸梨香 様邸新築工事

超暖G3
全館空調
長期優良住宅

DATE

DWG. TTITLE

2026.04.04



仕様書-3

SCALE

DWG. NO.

—

A-03

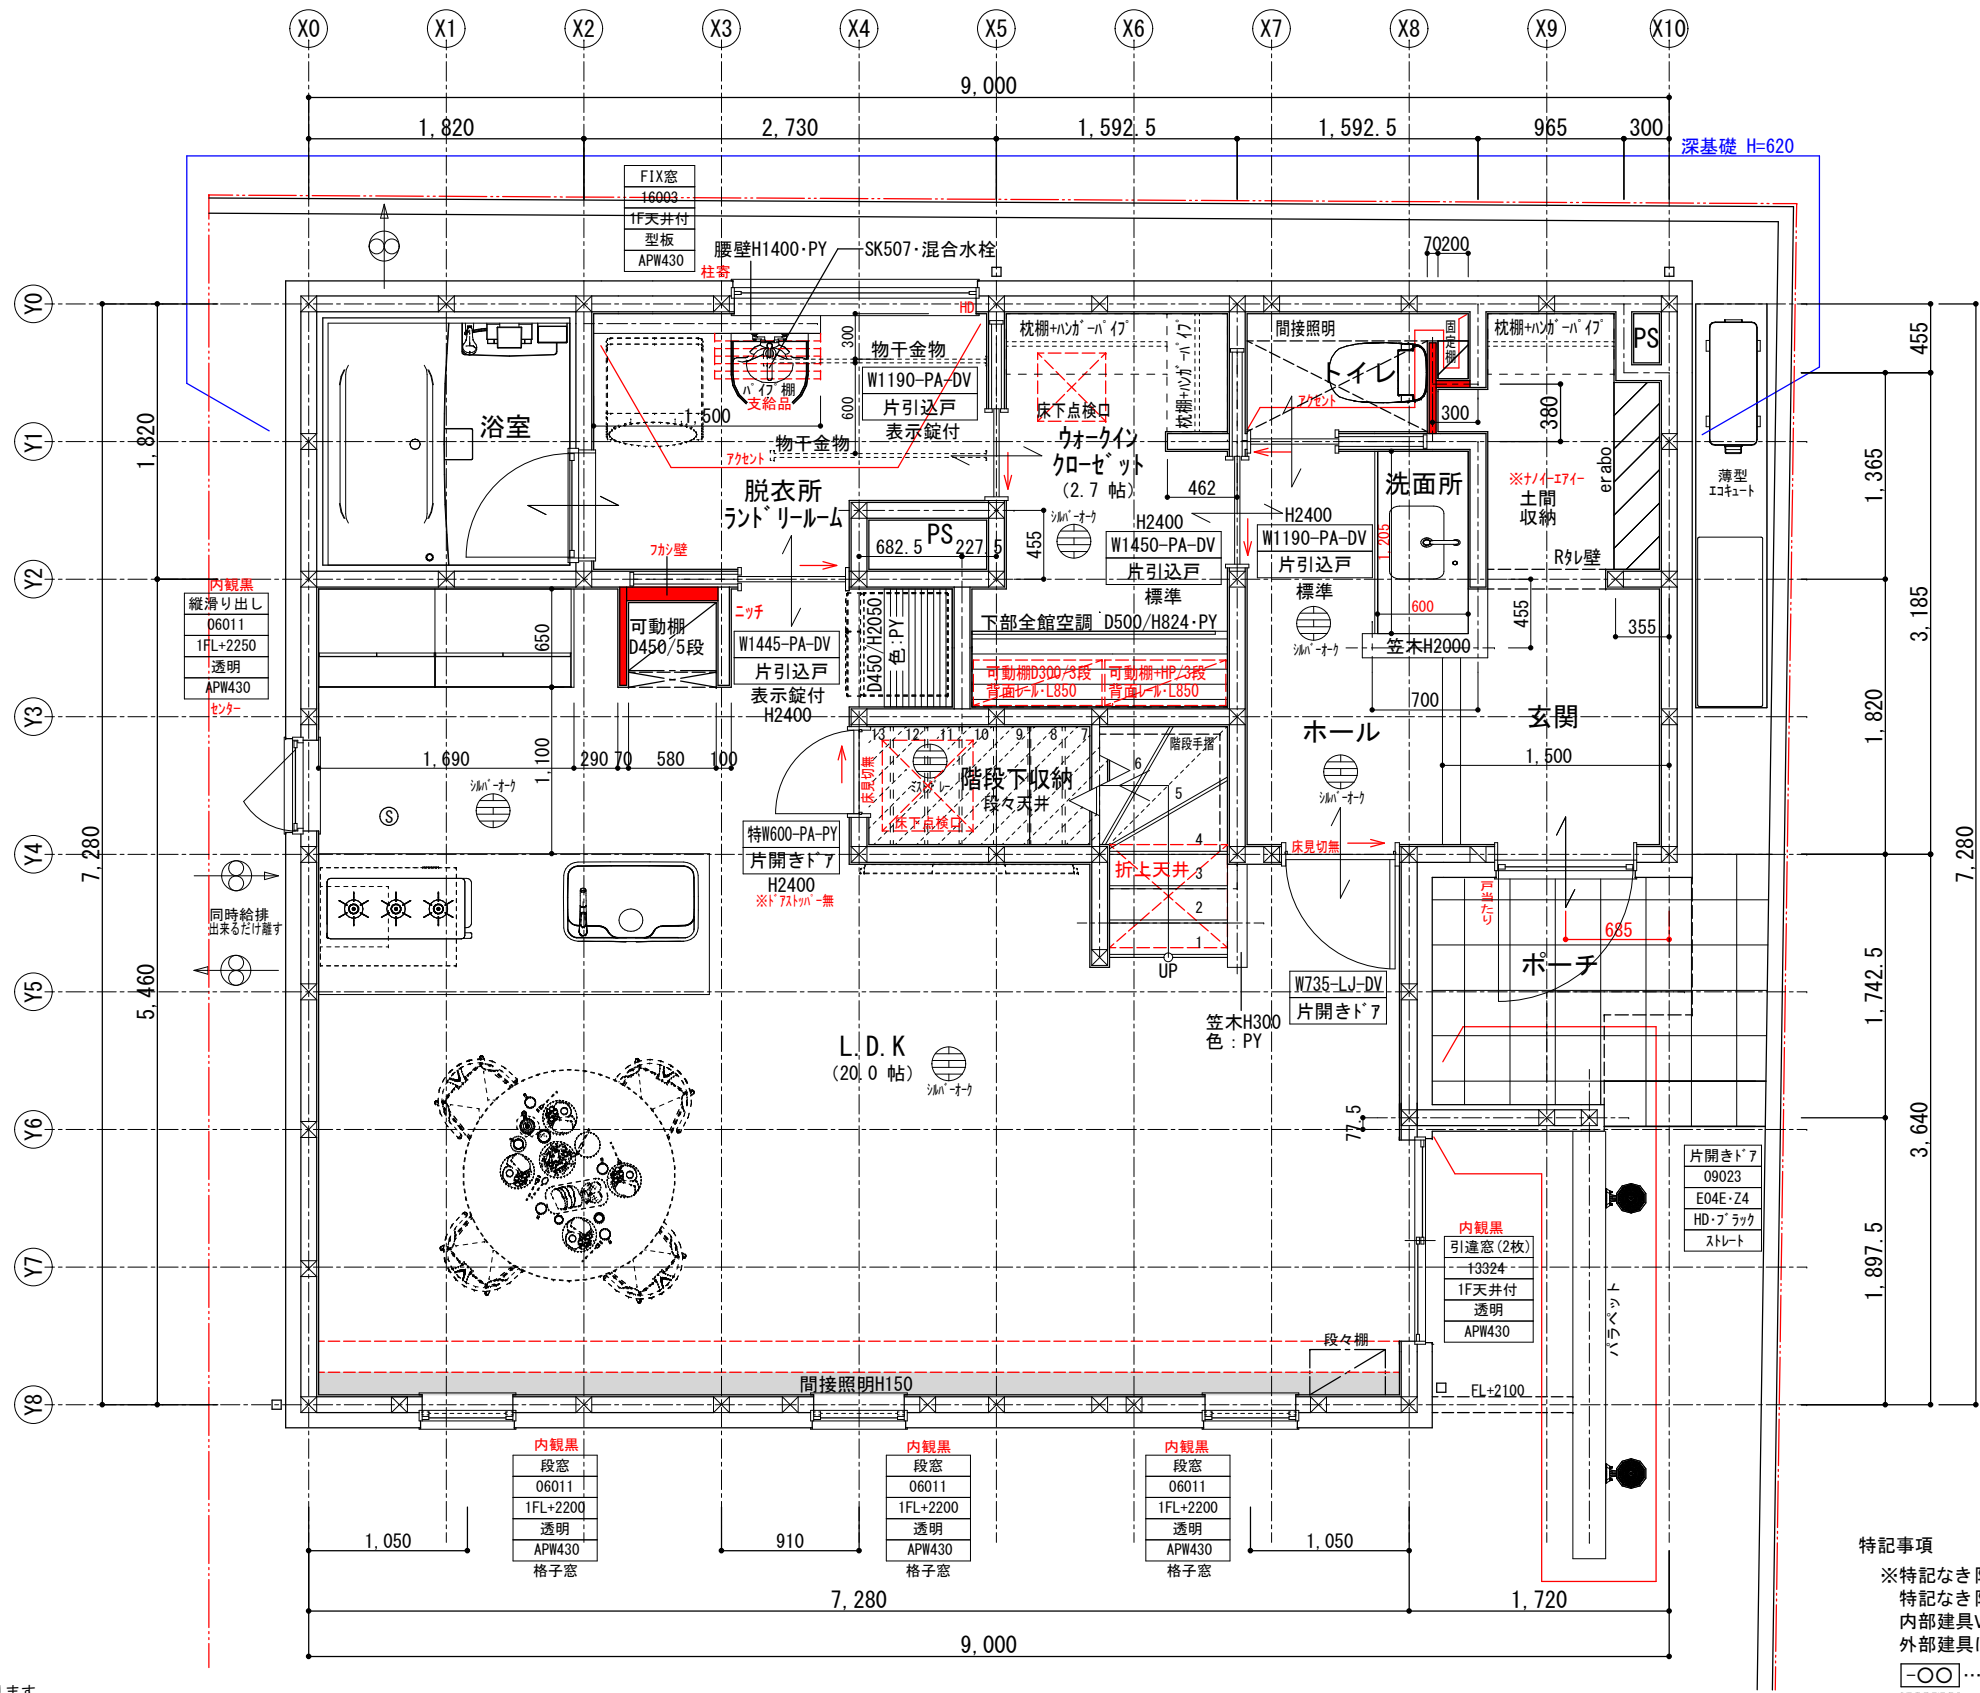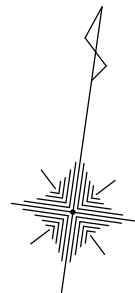


- 1 階床面積 59.62 m²
- 2 階床面積 44.51 m²
- 延べ床面積 104.13m² (31.49坪)
- 施工床面積 0.00 m² (0.00 坪)

- ・柱位置、耐力壁位置については構造図に準ずる
- ・寒冷地では玄関内部の立ち上がり部分において稀に結露することがあります
- ・アイアン手摺の落下の恐れがあるため、転落防止ネットの設置が必要です
- ・ポーチなどのタイル割寸法は現場にて異なることがあります
- ・階段下トレイなどの天井高さは現場にて異なることがあります
- ・柵等寸法は特記なき限り当社施工基準になります
- ・和室の壁は特記なき限り大壁仕上げとなります。畳厚さは1階：55mm、2階：15mmとなります
- ・階段の手すりの設置は外回り+高さは特記なき限り当社施工基準となります
- ・2Fキッチン、LB下部の1F天井に天井点検口を設置することがあります

- 特記事項
- ※特記なき限りサッシ内法寸法はH2000とする。
 - 特記なき限り床仕上げ高さは該当階FL±0とする。
 - 内部建具Wは、枠外寸法とする。
 - 外部建具は、規格寸法とする。
 - …該当階FLからの高低差とする。
 - 斜線 …下がり天井・勾配天井を示す。

	施主様	営業	工事	設計部長	設計	ARCHI homelife KYOTO	PROJ. NO	PROJ. TITLE 犬丸 和也様・犬丸 梨香様邸新築工事		超暖G3 長期優良住宅
							DATE	DWG. TITLE	SCALE	DWG. NO.
							2026/03/20	1 階平面図	1/50	A-05

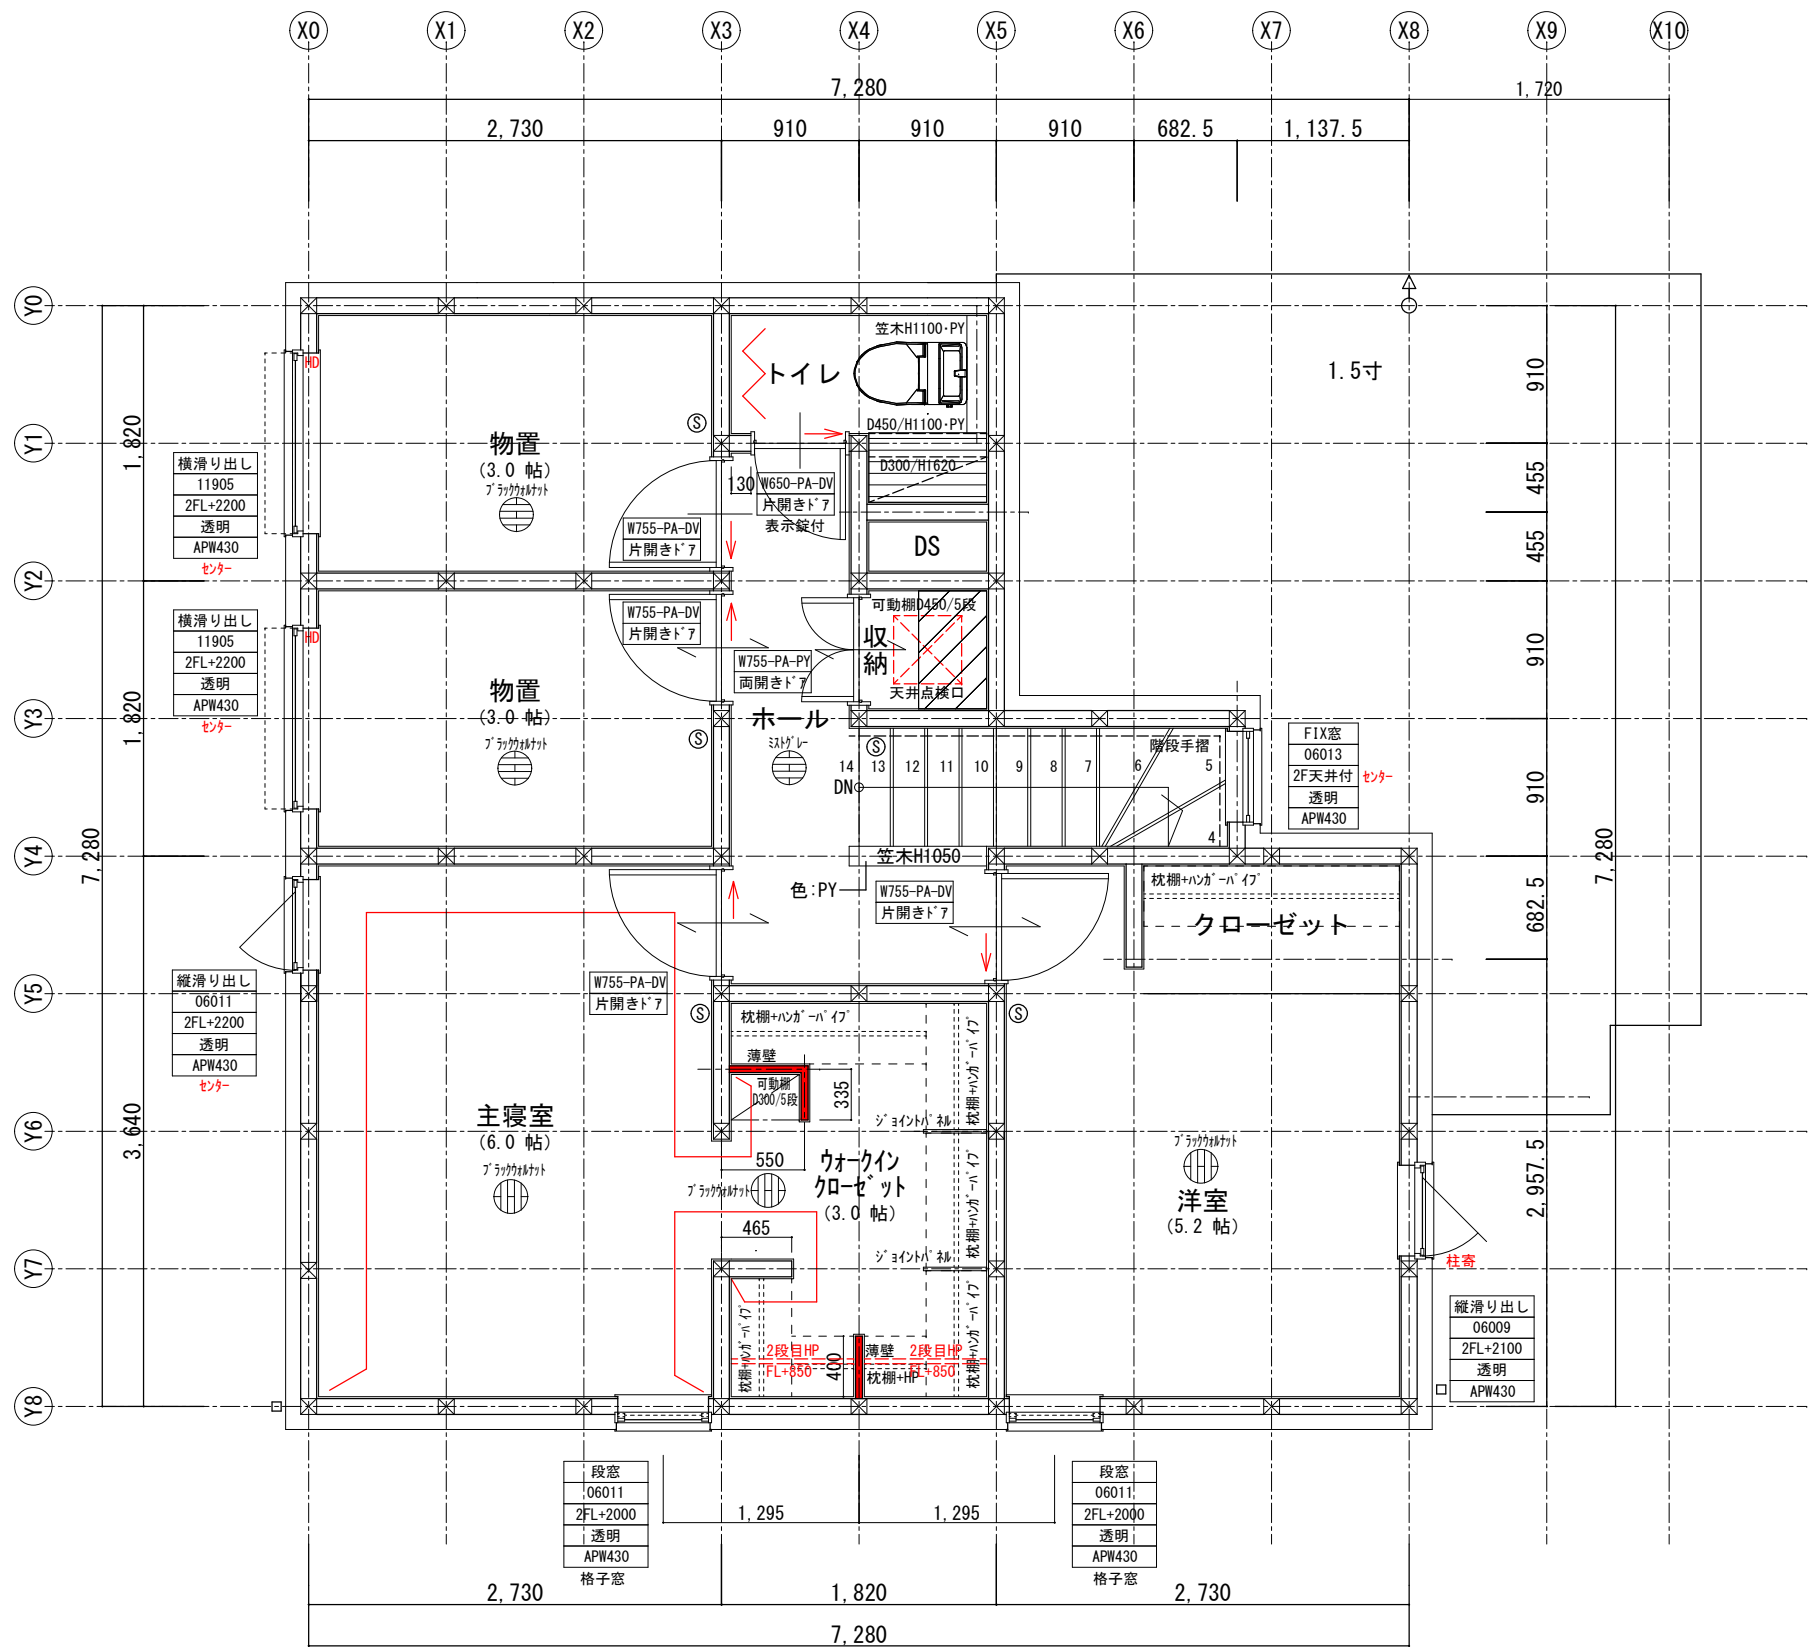


特記事項


※特記なき限りサッシ内法寸法はH2000とする。
特記なき限り床仕上げ高さは該当階FL±0とする。
内部建具Wは、枠外寸法とする。
外部建具は、規格寸法とする。

□○○…該当階FLからの高低差とする。
▨…下がり天井・勾配天井を示す。

	施主様	営業	工事	設計部長	設計	ARCHI homelife KYOTO	PROJ. NO	PROJ. TITLE 犬丸 和也様・犬丸 梨香様邸新築工事		超暖G3 長期優良住宅
							DATE	DWG. TITLE 2階平面図	SCALE 1/50	DWG. NO. A-06
							2026/04/04			

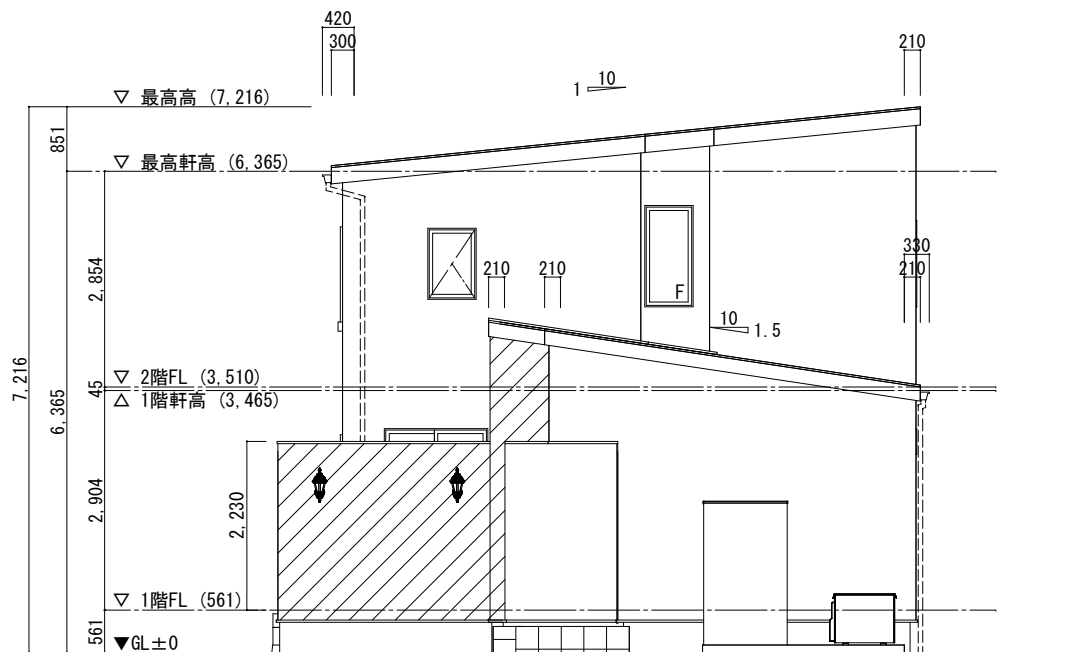


東側立面図

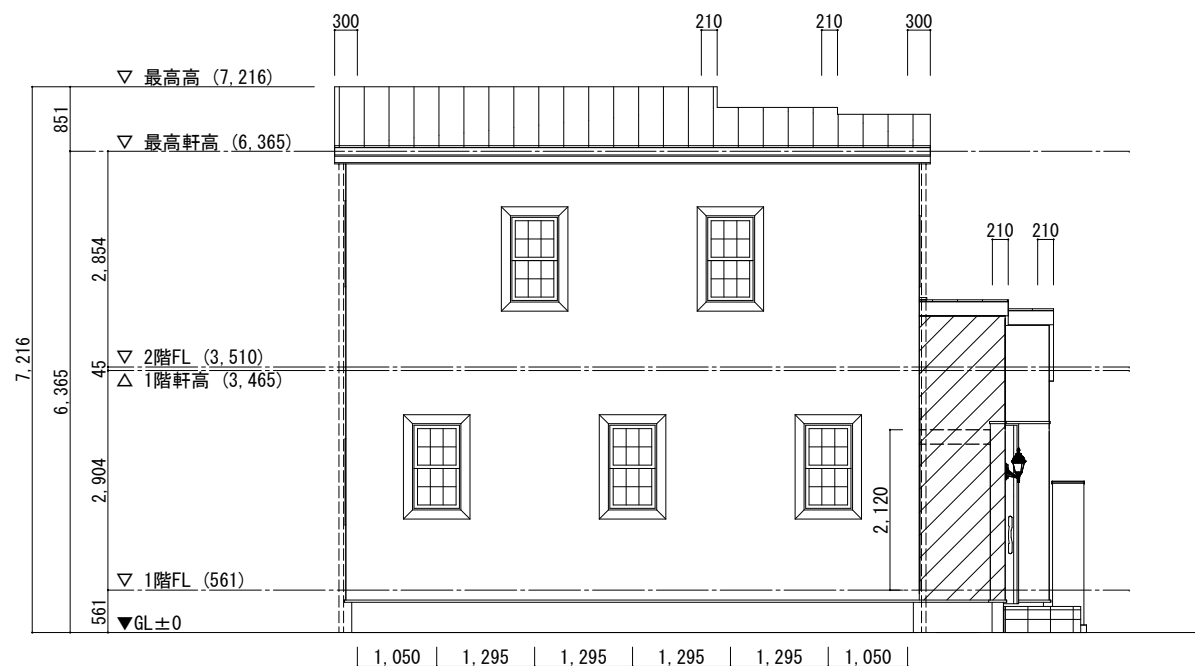


南側立面図

7セプトを示す

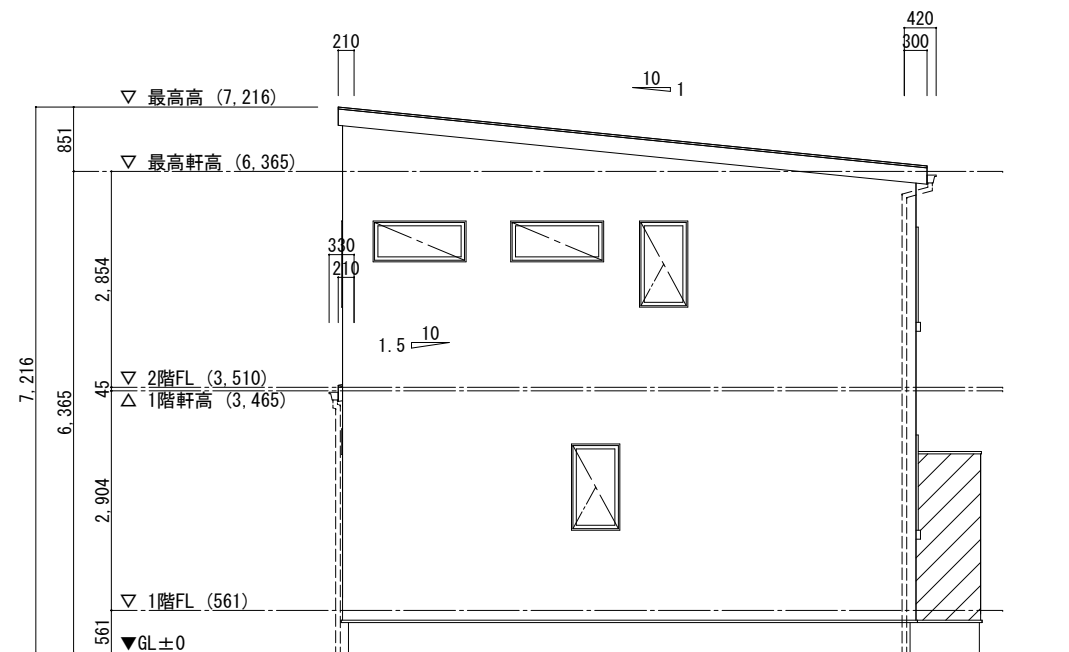


西側立面図

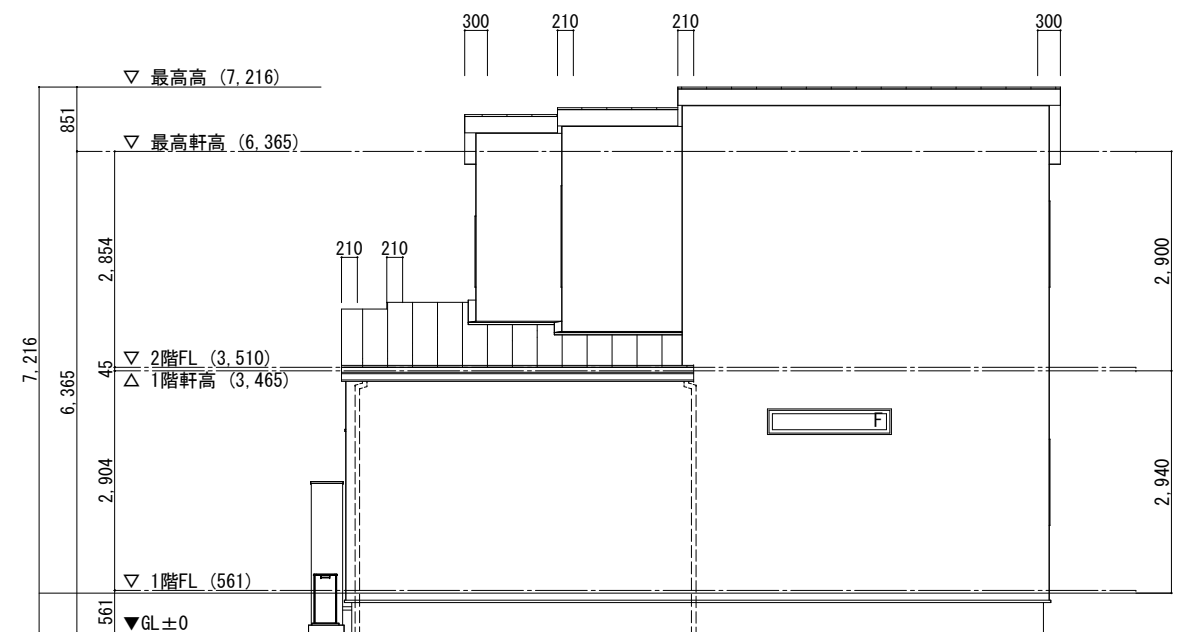

北側立面図


- ・ 軒位置、形状については現場状況により変更することがあります
- ・ 軒先の納まり等はあくまでイメージであり立面図と異なる場合があります
- ・ 外部7-7壁は、現場と図面で異なる場合があります

	施主様	営業	工事	設計部長	設計		PROJ. NO	PROJ. TITLE 犬丸 和也様・犬丸 梨香様邸新築工事		超暖G3 長期優良住宅
							DATE	DWG. TITLE	SCALE	DWG. NO.
							2026/04/04	立面図	1/100	A-07

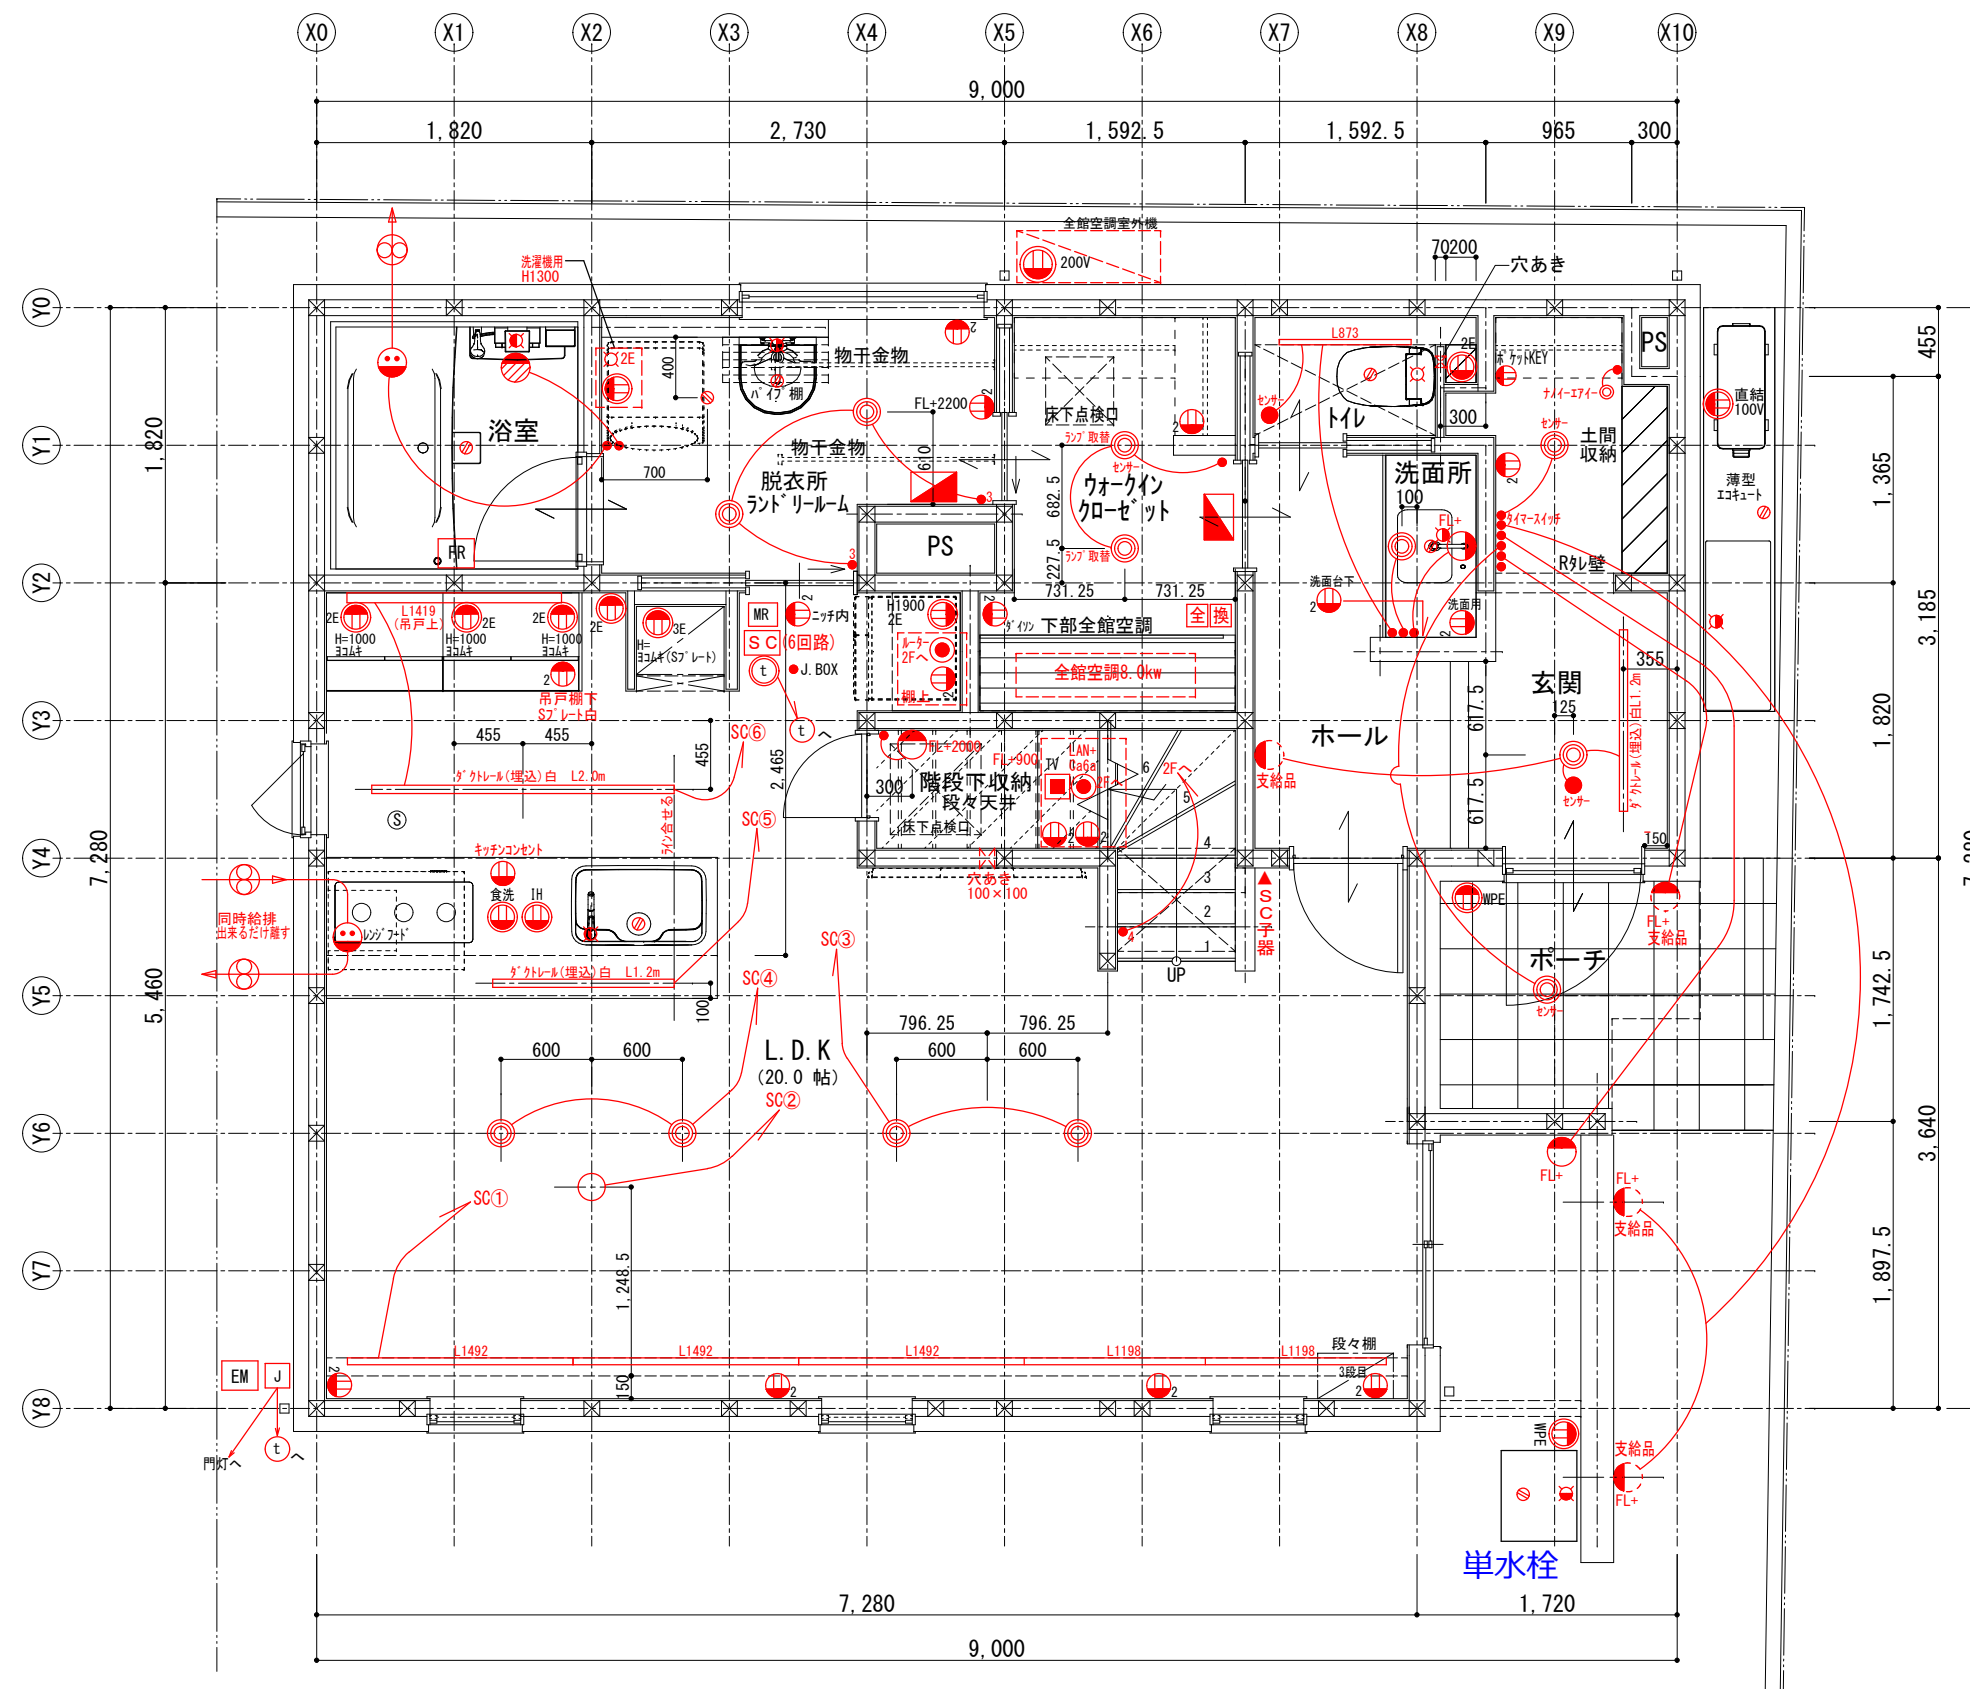

TVアンテナ：有
NET：（E0光）

・照明、スイッチの位置は構造上、図面と多少異なる場合があります	施主様	営業	工事	設計部長	設計		PROJ. NO	PROJ. TITLE		超暖G3・全館空調 長期優良住宅
・UHFアンテナ・BSアンテナ工事は別途必要です	前田			石原	小林		DATE	DWG. TITLE	SCALE	DWG. NO.
・洗面脱衣室へ洗濯パンは標準設置されません							2026/03/20	1 階設備図	1/50	A-09
・2階の天井点検口は現場合わせとなります										
・特記なき限り洗濯機の水栓は単水栓（水のみ）だけとなります										

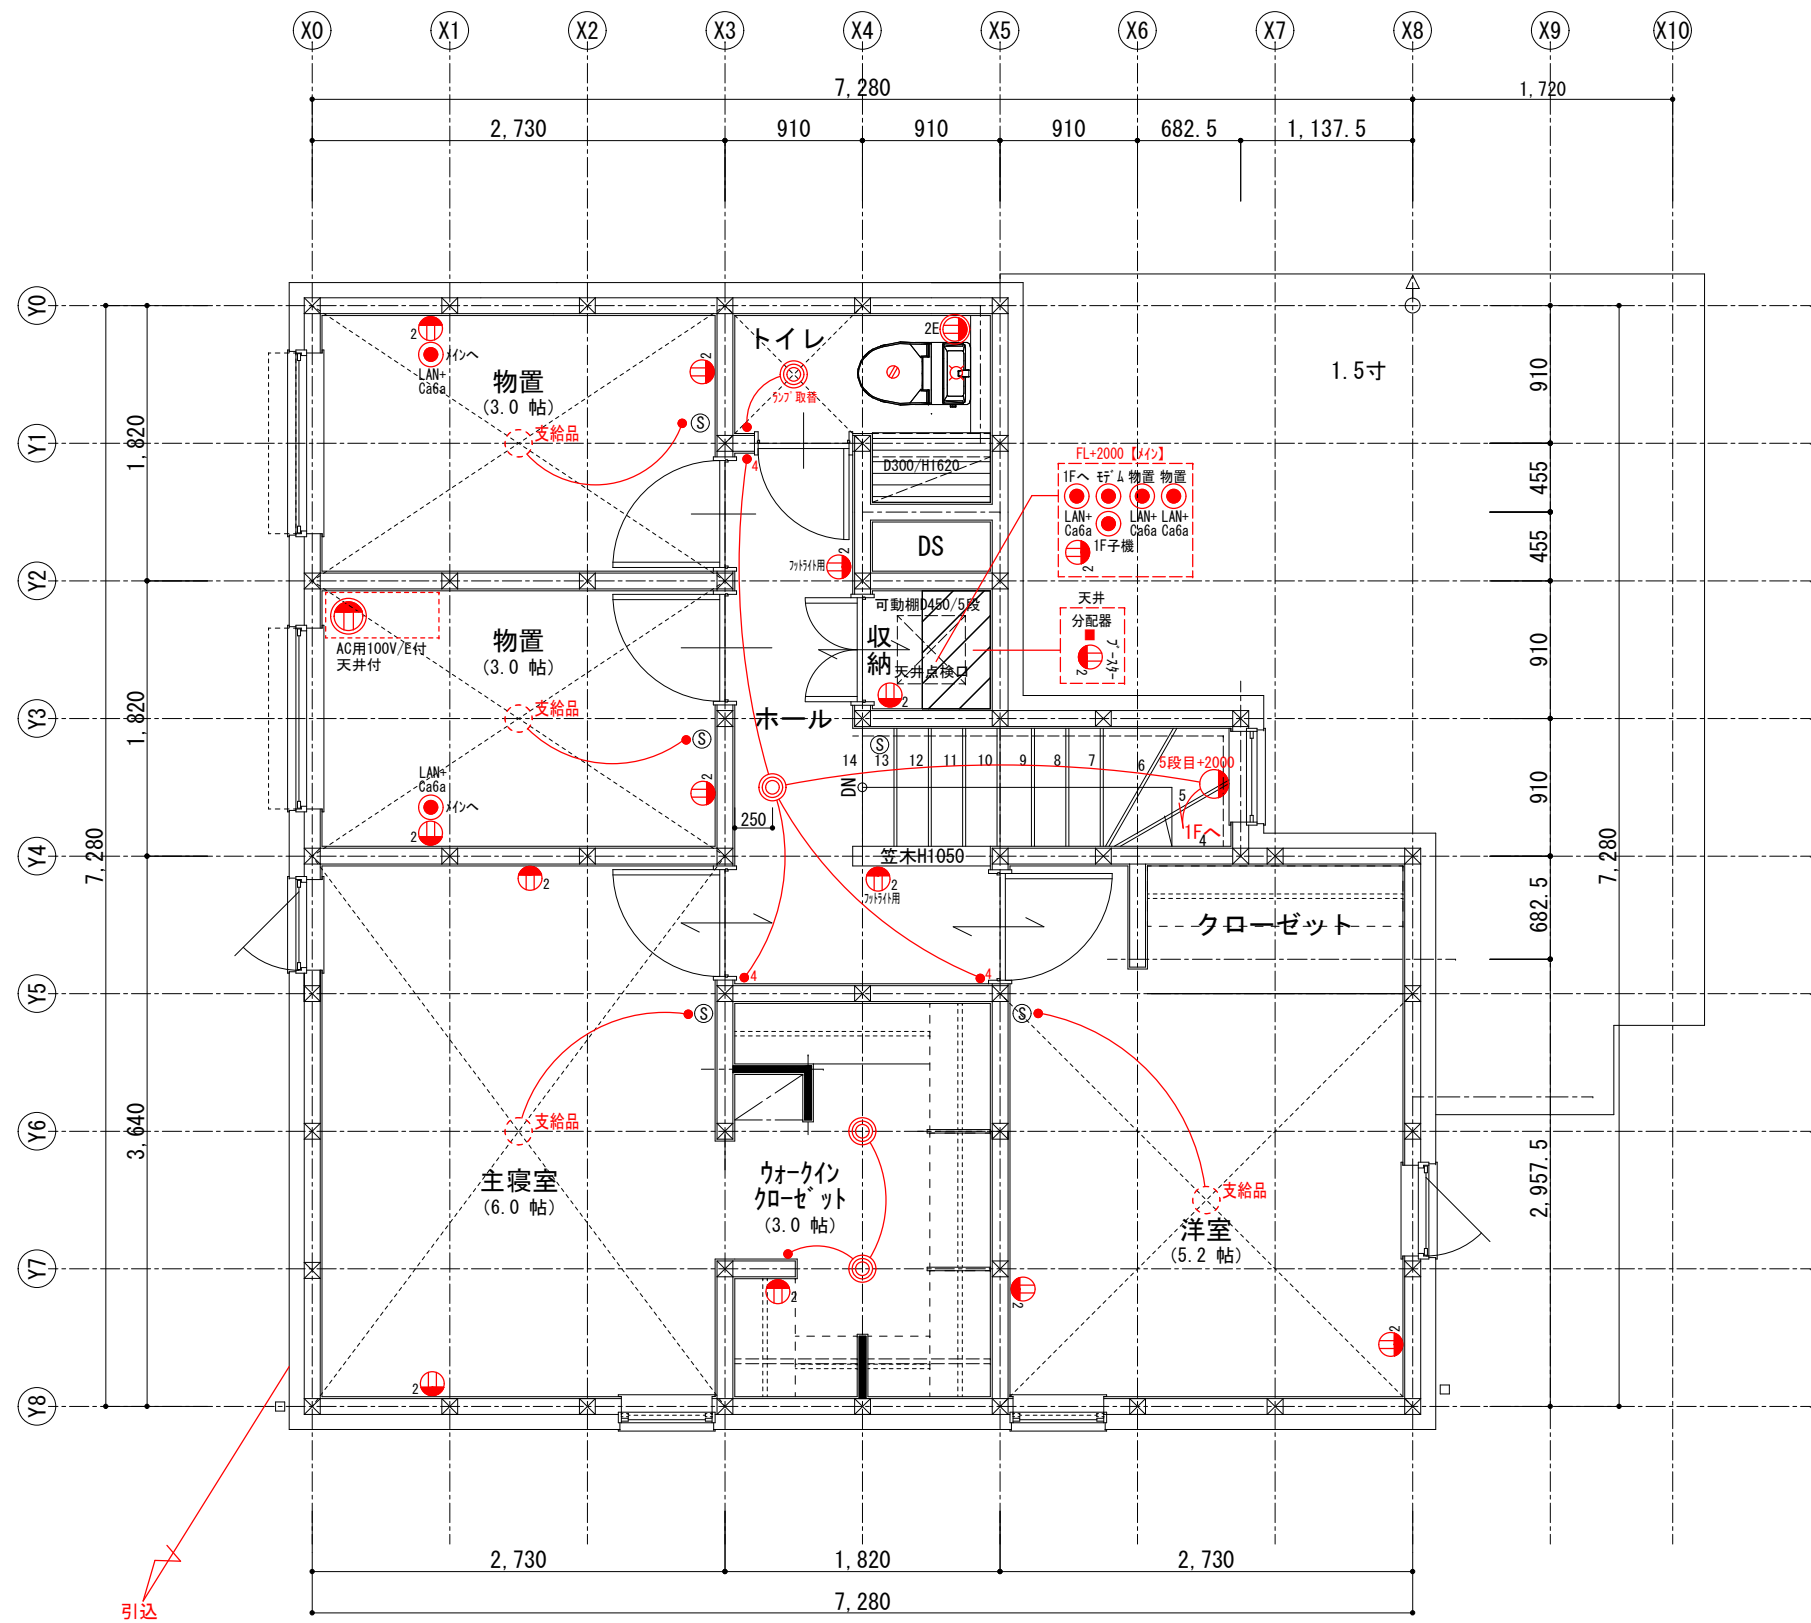

凡 例	
	1 ロコンセント
	2 ロコンセント
	2 ロアース付コンセント
	防水コンセント
	専用回路アース付コンセント
	直結電源
	専用回路直結電源
	T V 配線 (B S 同軸ケーブル)
	電話配管 ※入線工事は別途
	インターホン (親機)
	ドアホン
	給湯器メインリモコン
	浴室リモコン
	ジョイントBOX
	分電盤
	電気メーター
	シーリングライト
	ブラケット
	ユニット一体照明器具
	ダウンライト
	引掛シーリング (埋込丸型)
	24時間計画換気排気機
	24時間計画換気給気口
	S: 火災報知器 (煙感知)
	H: 火災報知器 (熱感知)
	スイッチ
	3 路スイッチ
	ホテルスイッチ
	パイロットスイッチ
	24時間計画換気用スイッチ
	調光付きスイッチ
	給水配管
	給湯給水配管
	排水口
■スイッチ・コンセントプレート等の取付け高さは、特記なき限り下記の通りとする。	
各種スイッチ	FL+ドア7/7センター
一般コンセント	プレート芯=FL+200
A C 用コンセント	プレート 芯 (横) =FL+1900
インターホン	器具芯=FL+1450
各種コントローラー	
24時間計画給気口	器具芯=FL+1950

TVアンテナ：有
NET：(E0光)

・ 照明、スイッチの位置は構造上、図面と多少異なる場合があります	施主様	営業	工事	設計部長	設計	 ARCHI homelife KYOTO	PROJ. NO	PROJ. TITLE		超暖房・全館空調 長期優良住宅
・ UHFアンテナ・BSアンテナ工事は別途必要です								犬丸和也 様・犬丸梨香 様邸新築工事		
・ 洗面脱衣室へ洗濯パンは標準設置されません							DATE	DWG. TITLE	SCALE	
・ 2階の天井点検口は現場合わせとなります		前田		石原	小林		2026/04/04	2 階設備図	1/50	
・ 特記なき限り洗濯機の水栓は単水栓（水のみ）だけとなります										DWG. NO. A-10